
MAINTENANCE STOPPER

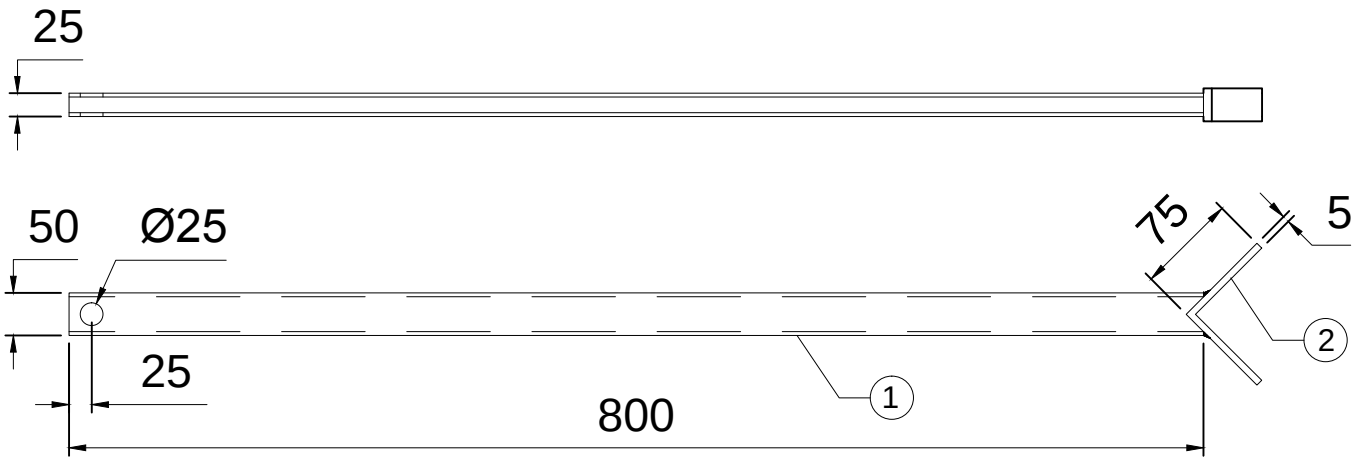

1. SQ .TUBE 50 X 25 X 3 THK X 800L = 2 NOS
2. ISA 75 X 75 X 5 X 35L = 2 NOS

TOLERANCE - ±5mm

This drawing & design is the property of NIHVA TECHNOLOGIES. Not to be sold or copied to any other concern.

TITLE				
MAINTENANCE STOPPER DRG				NIHVA TECHNOLOGIES PVT. LTD. PUNE Tel : 020 66304033 Email:- info@nihva.com Website:- www.nihva.com
	NAME	SIGN	DATE	
DRAWN	PRADEEP		05.09.2018	CLIENT -
CHECK	PRADEEP		05.09.2018	PROJECT - DLSD1010
APPRD.	PRADEEP		05.09.2018	SITE LOCATION -
If any queries contact : design@nihva.com				DWG. NO. : NIHVA/18-19/MFG/DLSD1010/009
ALL DIMENSION ARE IN mm				SCALE: NTS / WT: / REV- 0