




SIDE VIEW

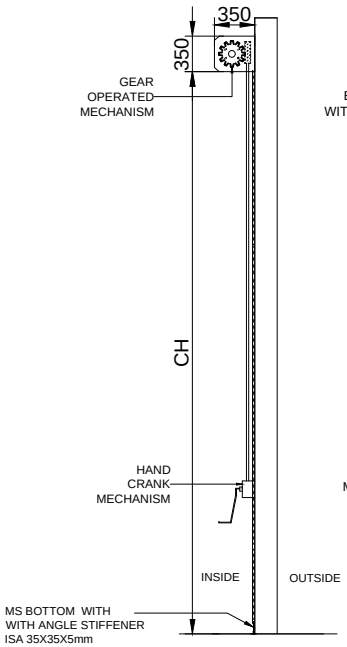


INSIDE ELEVATION

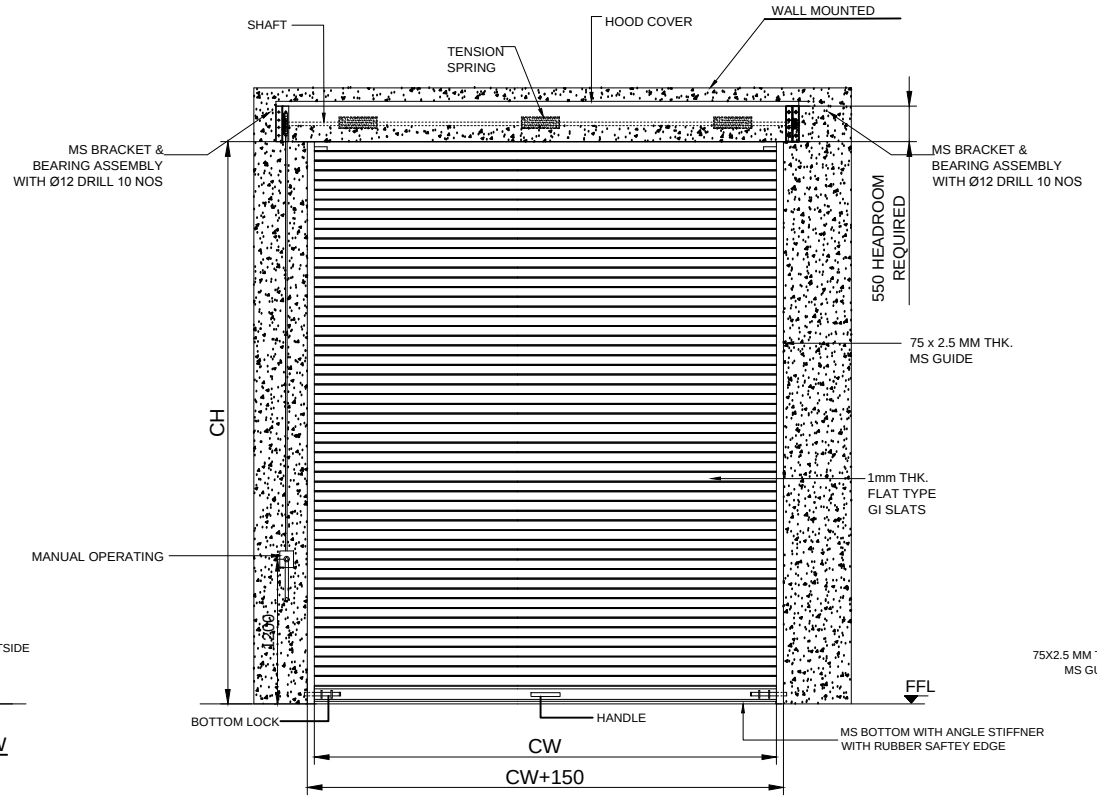

PLAN

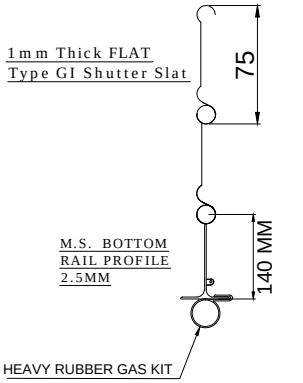

M.S. BOTTOM RAIL PROFILE 2.5MM

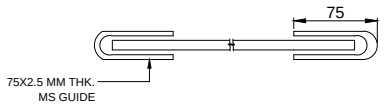

NOTE-
1. ALL CIVIL WORK WILL BE CLIENT'S SCOPE.

TOLERANCE - ±10mm

SR.NO.	RAL COLOR	SR.NO.	SIZE	QUANTITY	MOUNTING
01	RAL 9002 (WHITE GREY)	01	2000(W) X 3000(H)	05 NOS	WALL MOUNT

This drawing & design is the property of NIHVA TECHNOLOGIES. Not to be sold or copied to any other concern.

TITLE
GEAR OPERATED ROLLING SHUTTER

	NAME	SIGN	DATE
DRAWN	P.A		07.01.2020
CHECK	G.J		07.01.2020
APPRD.			

If any queries contact : design@nihva.com

ALL DIMENSION ARE IN mm

NIHVA TECHNOLOGIES PVT. LTD.
NIHVA TECHNOLOGIES PVT. LTD. PUNE
Tel : 020 66304033
Email:- info@nihva.com
Website:- www.nihva.com

CLIENT -
PROJECT-
SITE LOCATION -
DWG. NO. : NIHVA/19-20/274 | REV- 0
SCALE: NTS | WT: | SHEET: 01 OF 01