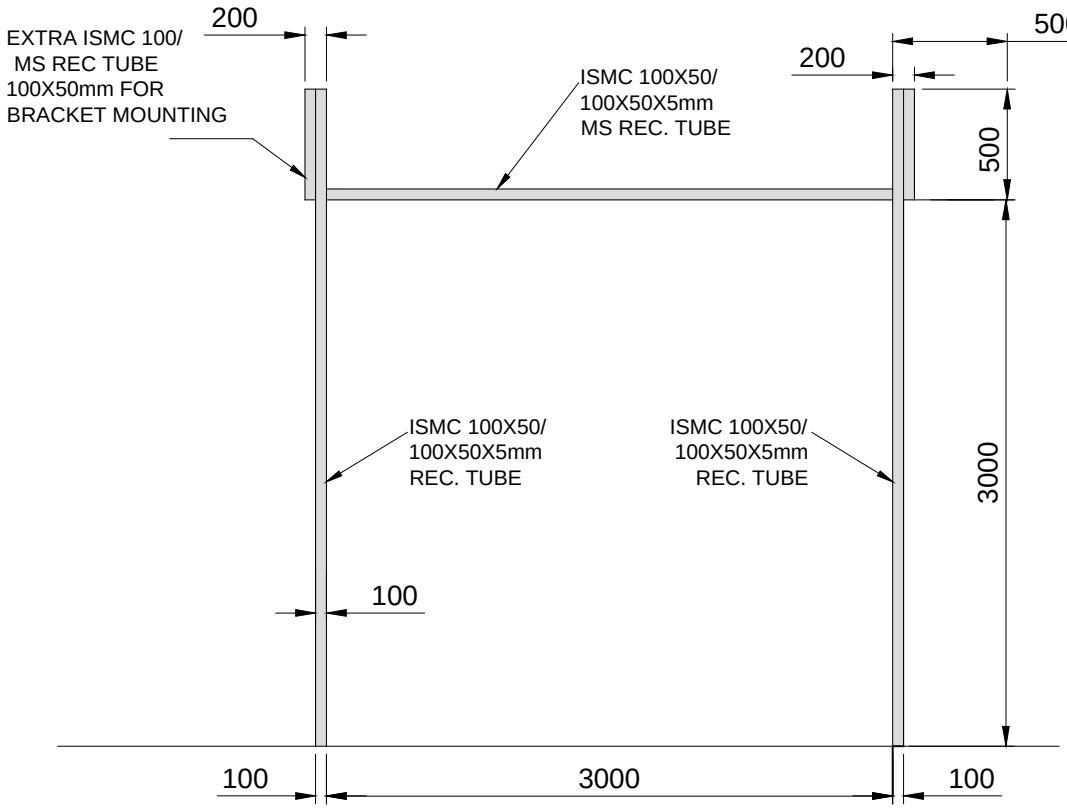

MS STRUCTURE

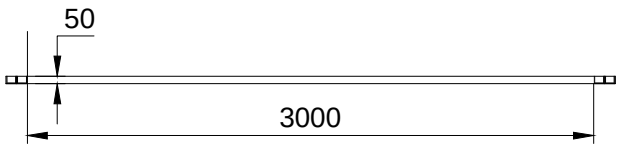

CLEAR WIDTH (CW)	CLEAR HEIGHT (CH)	QUANTITY
3000 mm	3000 mm	2 NOS

This drawing & designing is the property of NIHVA TECHNOLOGIES. Not be sold or copy to any other concern.

TITLE: DOUBLE WALL ROLLING SHUTTER STRUCTURE

NIHVA TECHNOLOGY PVT. LTD. PUNE
Tel : 020 66304033
Email:- info@nihva.com
Website:- www.nihva.com

	NAME	SIGN	DATE
DRAWN	SURAJ		30/01/18
CHECK	OMKAR		30/01/18
APPRD.	SHEKHAR		30/01/18

CLIENT -DHOOT BUILDERS

PROJECT -SKODA AUTO IND. PVT LTD.

SITE - AURANGABAD

ALL DIMENSION ARE IN mm

DWG. NO. -NIHVA/17-18/0344

REV. : 0

If any queries contact : design@nihva.com

SCALE: NTS | WT: | SHEET: 01 OF 01