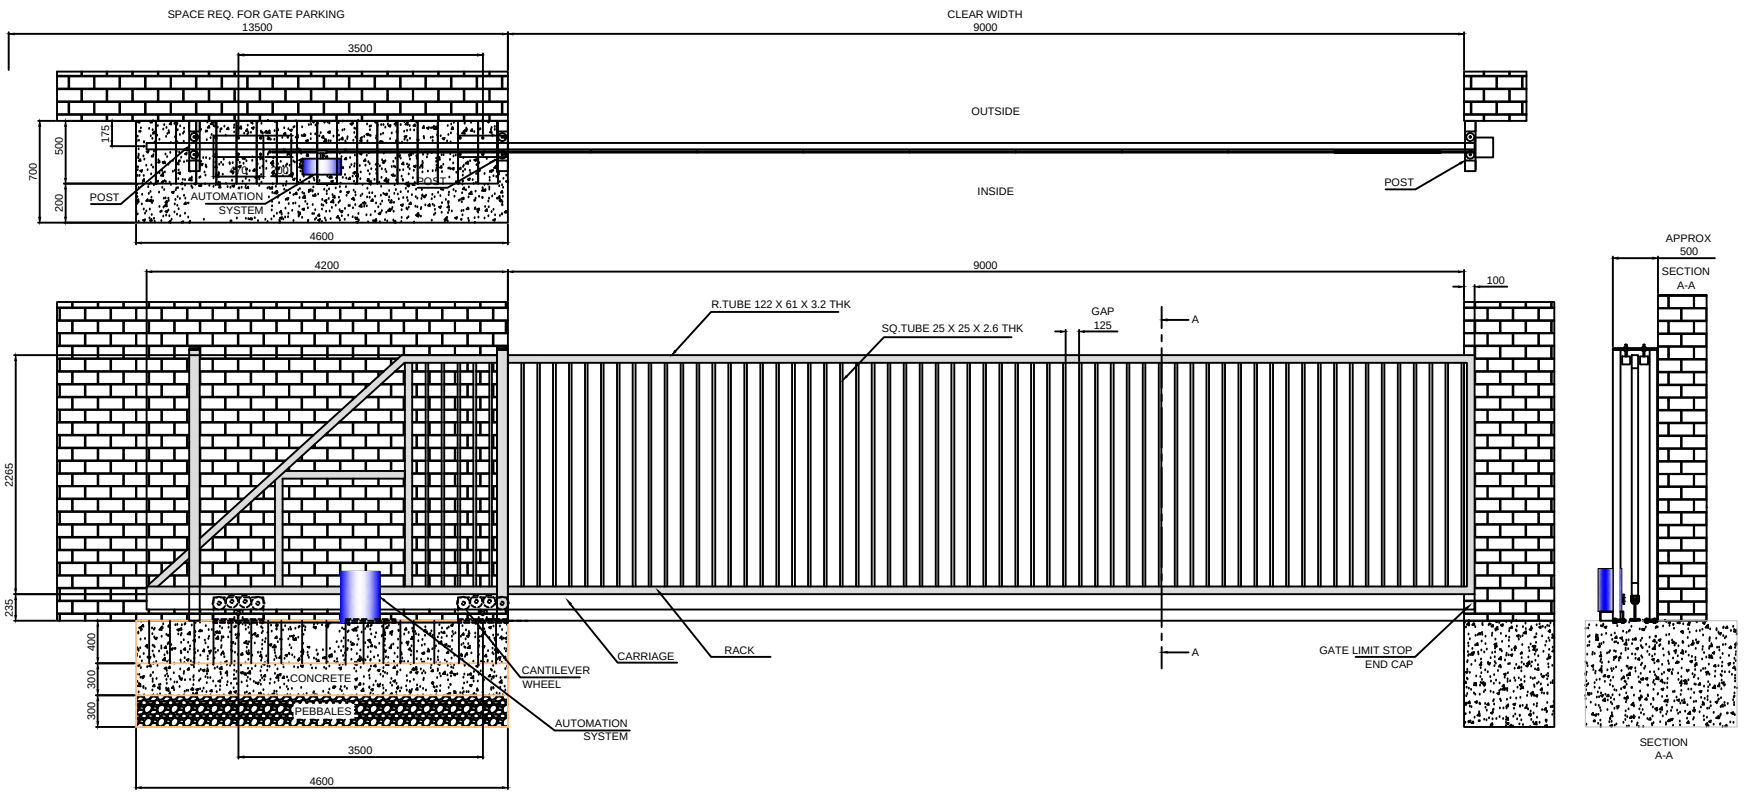


NOTE-

1. ALL REQUIRED CIVIL WORK WILL BE IN CLIENTS SCOPE.
2. ONE COAT OF RED OXIDE & TWO COAT OF APPROVED RAL SHADE WILL BE GIVEN TO THE GATE.
3. GATE LEAF WILL BE IN TWO/THREE PARTS FOR TRANSPORTATION & WILL BE WELD TOGETHER ON SITE.

QTY : 2 NOS

RAL 1003
RAL 2004
RAL 3000
RAL 5002
RAL 6005
RAL 7035
RAL 9005
RAL 9010

TOLERANCE - ±10mm

REV NO	DATE	DRAWN	REMARK
R02	05.02.2020	P.A	1. FOUNDATION DETAILS ADD
R01	07.01.2020	P.A	1. SIZE & DESIGN CHANGE

This drawing & design is the property of NIHVA TECHNOLOGIES. Not to be sold or copied to any other concern.

TITLE
AUTOMATIC CANTILEVER GATE

	NAME	SIGN	DATE
DRAWN	P.A		18.12.2019
CHECK	G.J		18.12.2019
APPRD.			

If any queries contact : design@nihva.com

ALL DIMENSION ARE IN mm

NIHVA
NIHVA TECHNOLOGIES PVT. LTD.
NIHVA TECHNOLOGIES PVT. LTD. PUNE
Tel : 020 66304033
Email:- info@nihva.com
Website:- www.nihva.com

CLIENT - SCON
PROJECT - INNOVATEC
SITE LOCATION - SANAND
DWG. NO. : NIHVA/19-20/0176/R02 | REV- R02
SCALE: NTS | WT: | SHEET: 01 OF 01