
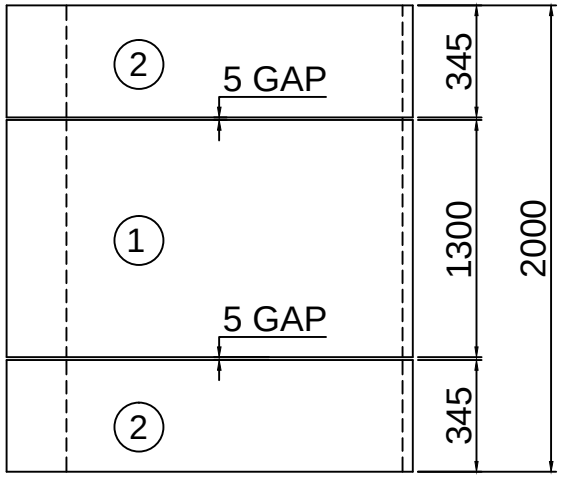


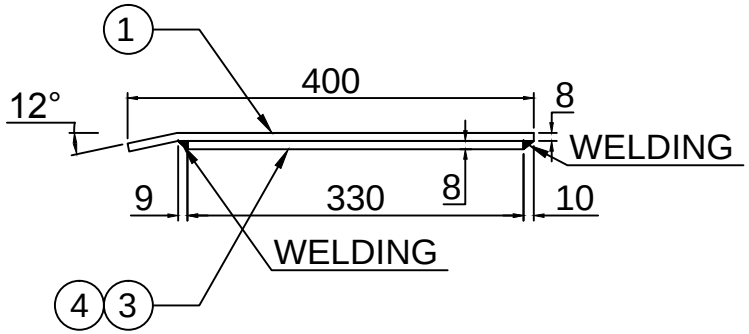

1. CHEQ. SHEET 400 X 8 THK X 1300L = 3 NOS
2. CHEQ. SHEET 400 X 8 THK X 345L = 6 NOS
3. CHEQ. SHEET 330 X 8 THK X 1280L = 3 NOS
4. CHEQ. SHEET 330 X 8 THK X 335L = 6 NOS

REV NO	DRAWN	DATE	DESCRIPTION
R 01	PRADEEP	15.09.18	LIP PLATE DESIGN CHANGE

This drawing & design is the property of NIHVA TECHNOLOGIES. Not to be sold or copied to any other concern.

TITLE: LIP PLATE DRG

	NAME	SIGN	DATE
DRAWN	PRADEEP		05.09.2018
CHECK	PRADEEP		05.09.2018
APPRD.	PRADEEP		05.09.2018

If any queries contact : design@nihva.com

ALL DIMENSION ARE IN mm

NIHVA TECHNOLOGIES PVT. LTD.
NIHVA TECHNOLOGIES PVT. LTD. PUNE
Tel : 020 66304033
Email:- info@nihva.com
Website:- www.nihva.com

CLIENT -

PROJECT - DLSD1009

SITE LOCATION -

DWG. NO. : NIHVA/18-19/MFG/DLSD1009/007/R01

SCALE: NTS | WT: | REV- 01