



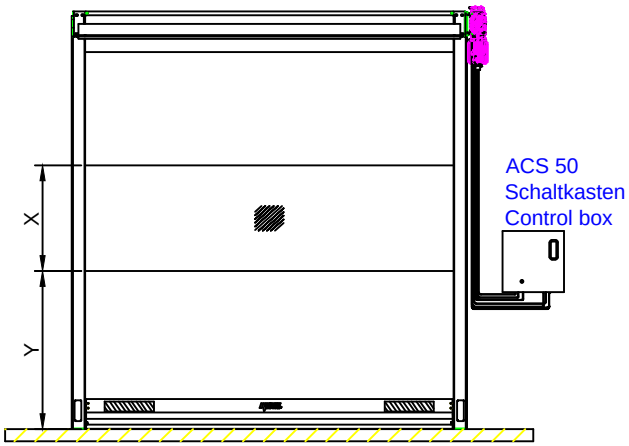


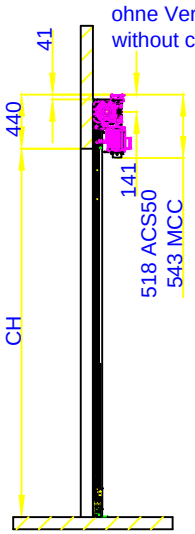


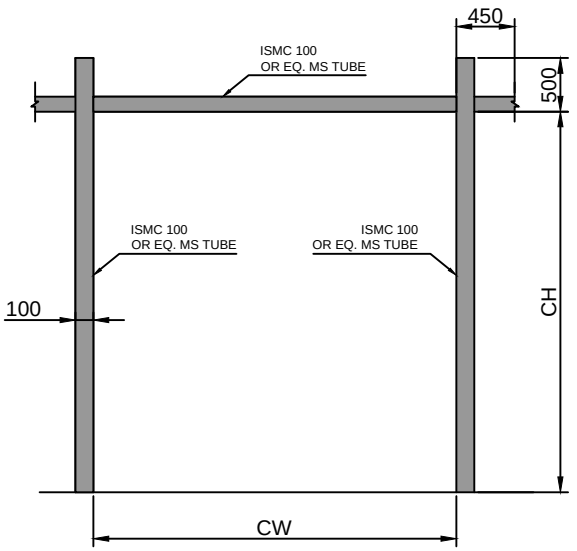


MS STRUCTURE

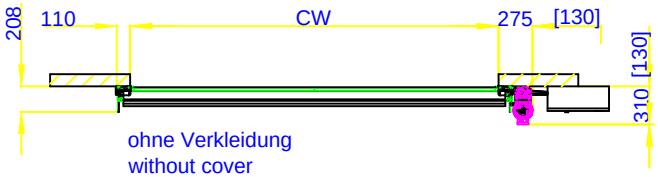

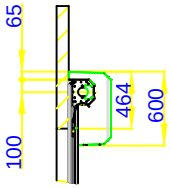

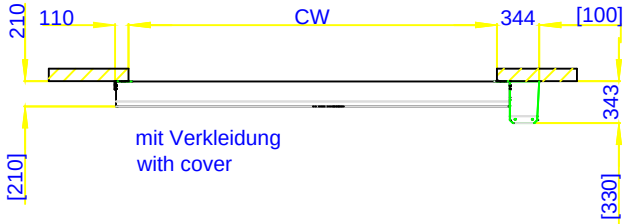

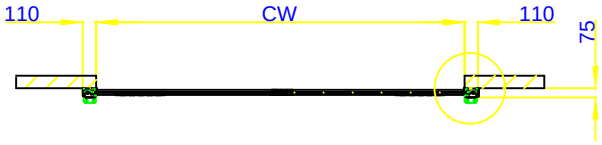

Color- Blue(RAL 5002)/ Red(3002)

Note- Client should mention X(700mm max height available) & Y values.

CLEAR WIDTH	CLEAR HEIGHT	QUANTITY
2900 mm	4400 mm	7 NOS

Tolerance ±3 mm (for all dimensions)

Dimensions in [ ] ==> clearance for installation

DIMENSION :

CLEAR WIDTH	CLEAR HEIGHT	QUANTITY
2900 mm	4400 mm	7 NOS

MATERIAL :

THICKNESS :

Note- Required structure for door will be in clients scope.

NIHVA TECHNOLOGIES PVT. LTD.
NIHVA TECHNOLOGIES PVT. LTD. PUNE
Email:- info@nihva.com
Website:- www.nihva.com

TITLE:

MACHINE PROTECTION DOOR

CLIENT'S APPROVAL :

CLIENT - KALD ON DESIGN PVT. LTD.

PROJECT - JBM

SITE LOCATION - GURGAON

DWG. NO. : NIHVA/15-16/191/R01

SCALE: NTS	WT:	SHEET:1 OF 1
DRAWN BY: SURAJ		DATE: 27-03-2017
CHECK BY: SAGAR		DATE: 27-03-2017
APPROVED BY : R.K.		DATE: 27-03-2017

If any queries contact : projects@nihva.com

NOTE: ALL DIMENSIONS ARE IN mm

THIS DRAWING & DESIGNING IS THE PROPERTY OF NIHVA TECHNOLOGIES. NOT TO BE SOLD OR COPIED TO ANY OTHER CONCERN.