
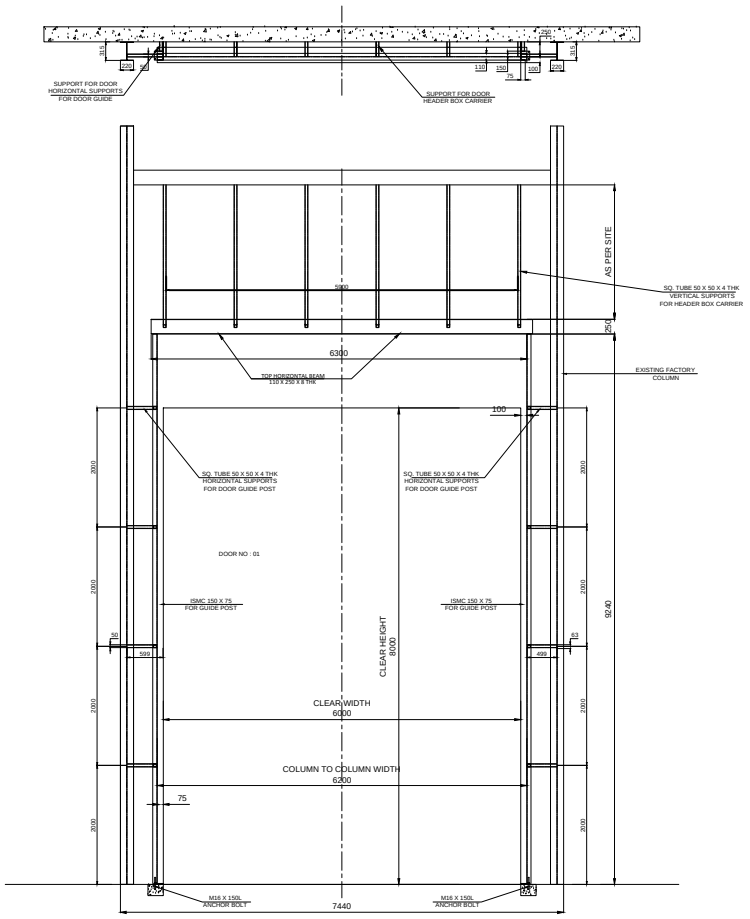


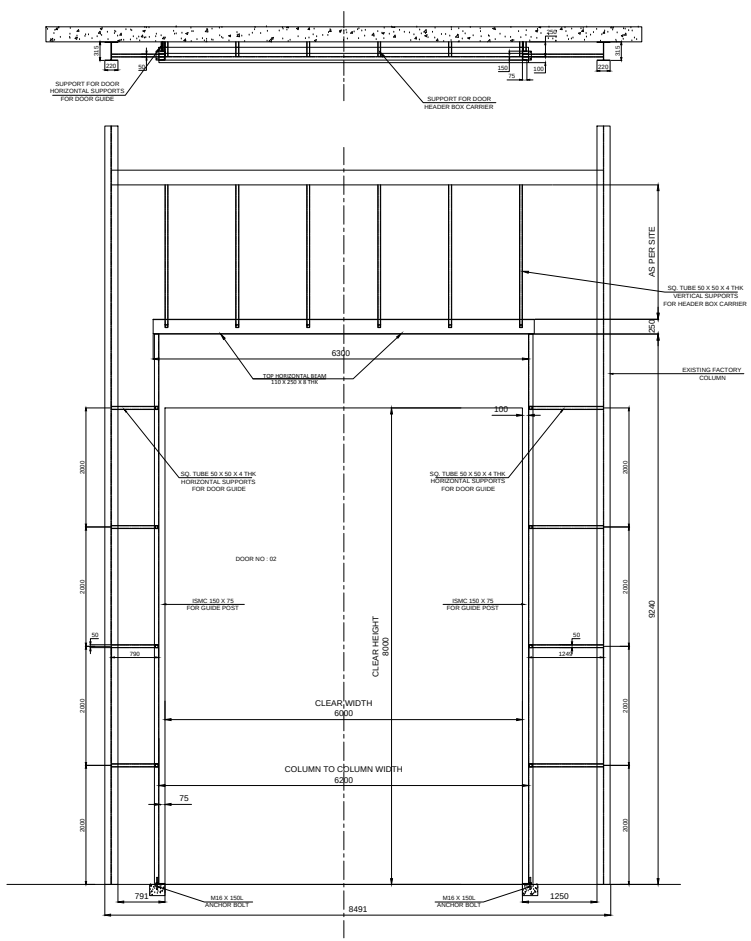

6000	8000	6200	9240
CLEAR WIDTH	CLEAR HEIGHT	TOTAL WIDTH	TOTAL HEIGHT

REV NO	REV DATE	DRAWN	REMARK
R02	03.06.19	P.V.A	1. TOP BEAM DETAILS ADDED.
R01	01.06.19	P.V.A	1. NO. OF VERTICAL & HORIZONTAL SUPPORTS FOR HEADER BOX CARRIER INCREASES. 2. ALSO ADDING VERTICAL COLUMN SUPPORT.

This drawing & designing is the property of NIHVA TECHNOLOGIES. Not to be sold or copied to any other concern.

TITLE: STRUCTURE DRAWING

NIHVA TECHNOLOGIES PVT. LTD.

NIHVA TECHNOLOGIES PVT. LTD. PUNE
Tel : 020 66304033
Website:- www.nihva.com
Email:- info@nihva.com

	NAME	SIGN	DATE
DRAWN	P.A		31.05.19
CHECK	S.P		31.05.19
APPROVAL	V.T		31.05.19

If any queries contact : design@nihva.com

ALL DIMENSION ARE IN mm

CLIENT - LMWP

PROJECT - LMWP

SITE LOCATION - BANGALORE

DWG. NO. : NIHVA/19-20/0025/R02 REV.:- R02

SCALE: NTS WT: SHEET: 01 OF 01