




ELEVATION

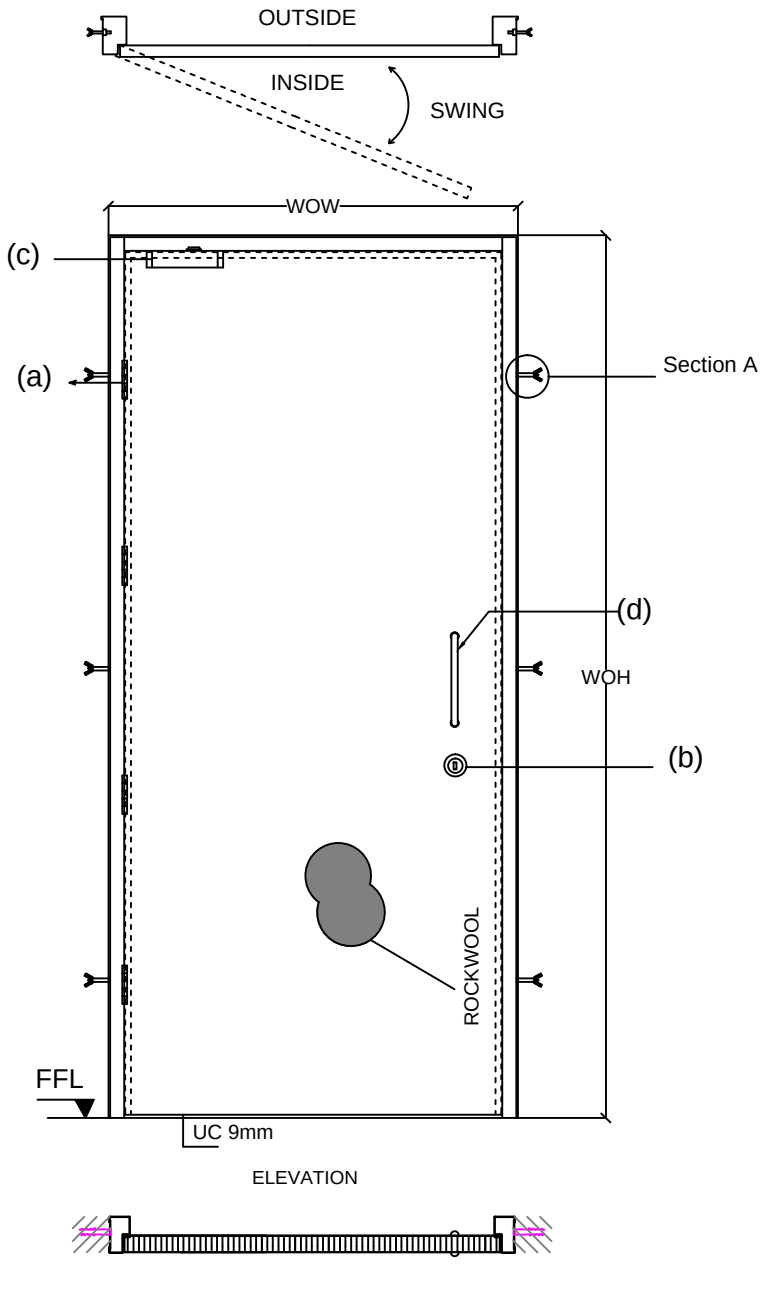

TOP VIEW

Abbrevation's:
WOW-Wall Opening Width
WOH-Wall Opening Height
UC-Under Cut
FFL-Finished Floor Level

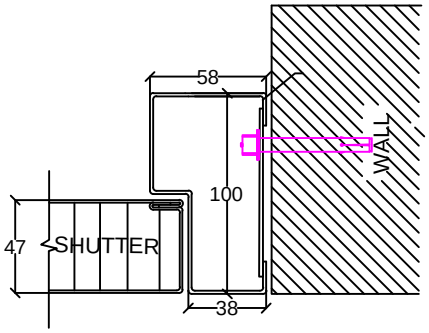


Section A

## ASSESORIES DETALES

(a) HINGES: SS Ball bearing butt hinges size 100x75x3mm

(b) LOCK : Mortise Dead lock,Cylinder(Both side key) with Escutcheon

(c) DOOR CLOSER

(d) HANDLE : SS D HANDLE

Shutter thickness : 47 mm
Frame Sheet thick : 1.20mm
Shutter sheet thick : 0.80mm
Fixing : On Soliid Brick plasterd wall with Anchors

NOTE:- *All Dimensions are in mm.
*Tolerance:-All Linear Dimensions ±3mm,Others ±0.5mm.
*The Drawing Is For Location of Hardware only. Drawing Does Not Represent The Hardware For More Clarity, Please Go Through Hardware Broucher.

## Steel door size

| WOW | WOH | TYPE 1 | TYPE 2 | TYPE 3 | TYPE 4 | QUANTITY |
|---|---|---|---|---|---|---|
| 900 | 2200 | | | | | 1 |

NOTE- 1. CLIENT SHOULD SELECT DOOR TYPE FROM DOOR HANDLING SHEET.
2. CLIENT SHOULD MENTION COLOR FOR DOOR.

COLOR
1.TRAFFIC WHITE (RAL 9016)
2.LIGHT GREY (RAL 7035)
3.GENTION BLUE (RAL 5010)
4.SIGNAL RED (RAL 3001)

This drawing & designing is the property of NIHVA TECHNOLOGIES. Not be sold or copy to any other concern.

STEEL DOOR (SINGLE LEAF)

CLIENT APPROVAL

ALL DIMENSION ARE IN mm

| | NAME | DATE | SIGN. |
|---|---|---|---|
| DRAWN | OMKAR | 29/12/16 | |
| CHECK | SAGAR P. | 29/12/16 | |
| REV. | | | |
| APPRD. | R.K. | | |
| MFG | | | |

NIHVA TECHNOLOGIES PVT. LTD.
NIHVA TECHNOLOGY PVT. LTD. PUNE
Tel : 020 66304033
Email:- info@nihva.com
Website:-www.nihva.com

CLIENT - ZAMIL STEEL BUILDINGS INDIA PVT.LTD.
PROJECT -
SITE -
DWG. NO. - NIHVA/16-17/0120
SCALE: NTS | WT: | SHEET: 01 OF 01
If any queries contact : projects@nihva.com