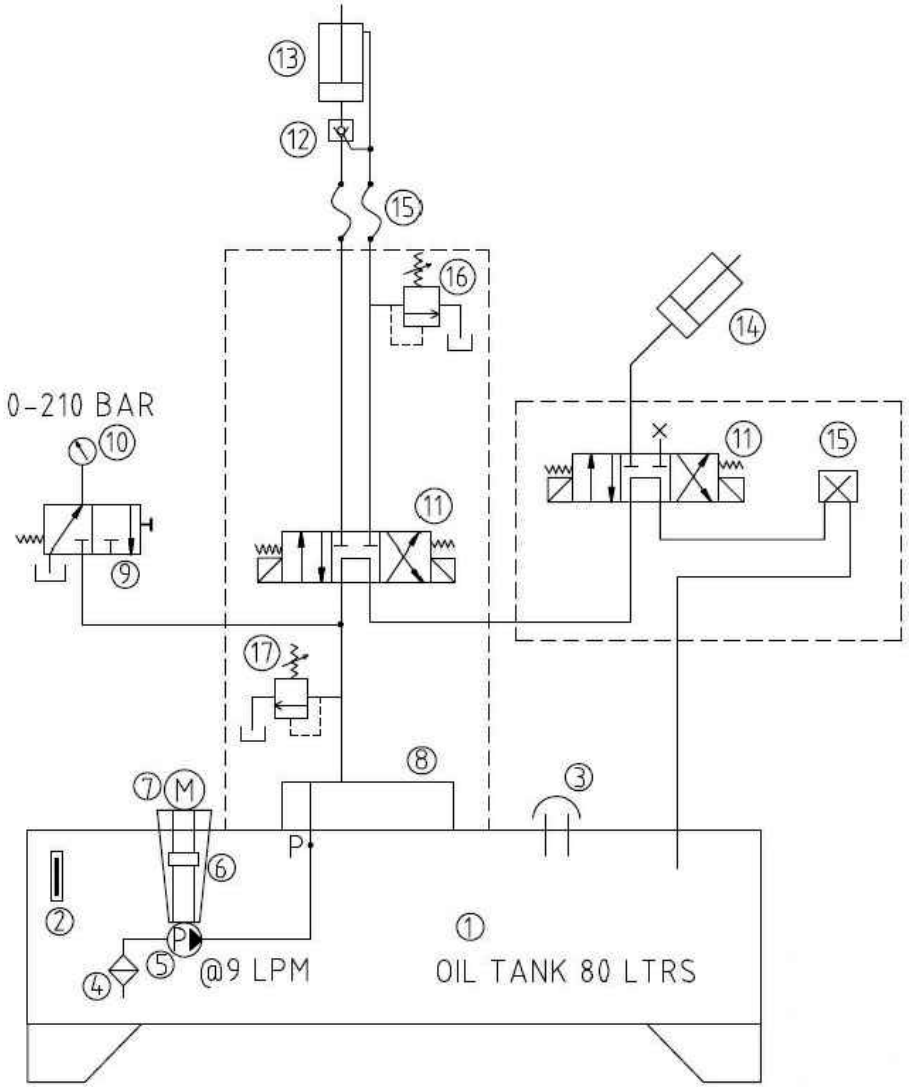


NO.	DESCRIPTION	MAKE	QTY.
17	PRESSURE RELIEF VALVE DPRH06S	POLYHYDRON	1
16	PRESSURE RELIEF VALVE MBA-01	YUKEN	1
15	BLANKING PLATE NG6	NIHVA	1
14	SINGLE ACTING CYLINDER	NIHVA	1
13	HYDRAULIC CYLINDER DA 125 BORE (NOT IN OUR SCOPE OF SUPPLY)	NIHVA	1
12	PILOT OPERATED CHECK VALVE CI 10 T	POLYHYDRN	1
11	DIRECTION CONTROL VALVE DSG 3C60 D24	YUKEN	2
10	PRESSURE GUAGE 63MM DIAL 0-210 BAR	WIKA	1
9	PRESSURE GUAGE ISOLATOR	FENNER	1
8	MANIFOLD BLOCK 3 STATION	NIHVA	1
7	ELECTRIC MOTOR 5HP/1440/FLANGE	SIEMENS	1
6	BELL HOUSING AND COUPLING	JACKTECH	1
5	GEAR PUMP AZPW21005	REXROTH	1
4	SUCTION STRAINER SC3 005	HYDROLINE	1
3	FILLER BREATHER FSB 25	HYDROLINE	1
2	OIL LEVEL GUAGE LG3	HYDROLINE	1
1	OIL RESRVIOR 80 LITERS	NIHVA	1

BILL OF MATERIAL

This drawing & design is the property of NIHVA TECHNOLOGIES. Not to be sold or copied to any other concern.

TITLE: HYDRAULIC CIRCUIT

NIHVA TECHNOLOGIES PVT. LTD.
NIHVA TECHNOLOGIES PVT. LTD. PUNE
Tel : 020 66304033
Email:- info@nihva.com
Website:- www.nihva.com

	NAME	SIGN	DATE
DRAWN	P.A		07.01.2019
CHECK	G.J		07.01.2019
APPRD.			

CLIENT - IKEA
PROJECT - IKEA
SITE LOCATION - CHAKAN PHASE III
If any queries contact : design@nihva.com
DWG. NO. :NIHVA/19-20/0193
REV- R00
ALL DIMENSION ARE IN mm
SCALE: NTS
WT:
SHEET: 01 OF 01