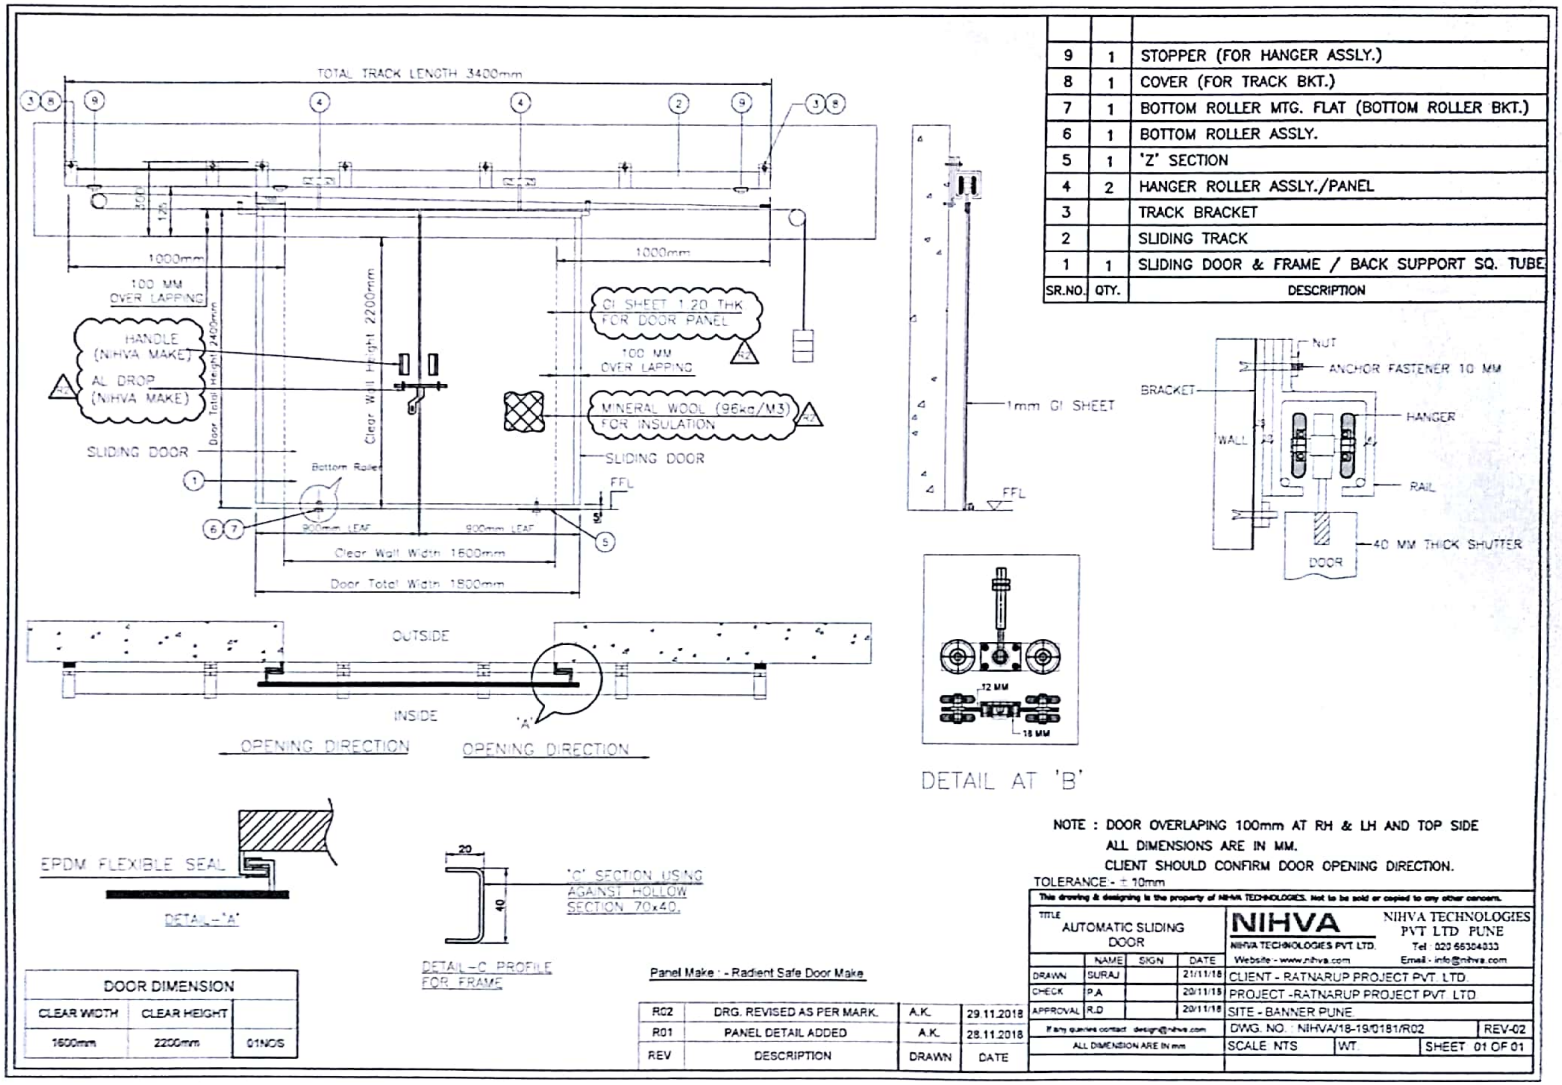


SR.NO.	QTY.	DESCRIPTION
9	1	STOPPER (FOR HANGER ASSLY.)
8	1	COVER (FOR TRACK BKT.)
7	1	BOTTOM ROLLER MTG. FLAT (BOTTOM ROLLER BKT.)
6	1	BOTTOM ROLLER ASSLY.
5	1	'Z' SECTION
4	2	HANGER ROLLER ASSLY./PANEL
3		TRACK BRACKET
2		SLIDING TRACK
1	1	SLIDING DOOR & FRAME / BACK SUPPORT SQ. TUBE

DOOR DIMENSION		
CLEAR WIDTH	CLEAR HEIGHT	
1600mm	2200mm	01NOS

REV	DESCRIPTION	DRAWN	DATE
R02	DRG. REVISED AS PER MARK.	A.K.	29.11.2018
R01	PANEL DETAIL ADDED	A.K.	28.11.2018

Panel Make : - Radient Safe Door Make

NOTE : DOOR OVERLAPING 100mm AT RH & LH AND TOP SIDE
ALL DIMENSIONS ARE IN MM.
CLIENT SHOULD CONFIRM DOOR OPENING DIRECTION.
TOLERANCE - ± 10mm

This drawing & designing is the property of NIHVA TECHNOLOGIES. Not to be sold or copied to any other concern.

TITLE	NIHVA	NIHVA TECHNOLOGIES PVT LTD PUNE
AUTOMATIC SLIDING DOOR	NIHVA TECHNOLOGIES PVT. LTD.	Tel 020 66304033
	Website - www.nihva.com	Email - info@nihva.com

	NAME	SIGN	DATE
DRAWN	SURAJ		21/11/18
CHECK	P.A		20/11/18
APPROVAL	R.D		20/11/18

CLIENT - RATNARUP PROJECT PVT. LTD.	
PROJECT -RATNARUP PROJECT PVT. LTD.	
SITE - BANNER PUNE	
DWG. NO. NIHVA/18-19/0191/R02	REV-02
SCALE NTS WT.	SHEET 01 OF 01

If any queries contact design@nihva.com
ALL DIMENSION ARE IN mm

* Drawing Approved w.r.t. Subject

Note → * Note :- Fire Rated automatic sliding door must be functional & it with stand ~~to ours~~ 2 Hrs fire ∞ without affecting any defects/stoppages

Prabhakar
(HMS)

RATNARUP DEVELOPERS PVT. LTD.

Vivek Tiwale
for (Kingfa)

Scanned by CamScanner