



SHUTTER TYPE	SKB 2 HOURS FIRE RATED ROLLER SHUTTER (BS 476)
SHUTTER SLATS	SKB–F7D DOUBLE WALLED STEEL WITH ROCKWOOL INFILL
SLATS FINISHING	POWDER COATED TO SKB STANDARD RAL COLOR
GUIDE RAIL	GALVANIZED STEEL SKB–G70
GUIDE RAIL FINISHING	POWDER COATED TO SKB STANDARD RAL COLOR
BOTTOM BAR	STEEL INSULATED F7D WITH L–ANGLE BOTTOM BAR
BOTTOM BAR FINISHING	POWDER COATED TO SKB STANDARD RAL COLOR
BOX DESIGN	MILD STEEL SECTION FRAME DESIGN
BOX & CASING COVER	0.8MM GALVANIZED STEEL
FINISHING OF COVER	POWDER COATED TO SKB STANDARD RAL COLOR
OPERATION	SKB–500KG MOTORISED WITH MANUAL OVERRIDE CHAIN
MOTOR POWER SOURCE	230 VOLTS, 1 PHASE, 50 Hz.
FIRE MODE	EMERGENCY RELEASE SYSTEM READY TO RECEIVED 24VDC FIRE SIGNAL
	FROM THE CONTROL ROOM AND SHUTTER–ER–A(AUTO RESET)
	THERMAL FUSSIBLE LINK WILL AUTO CLOSE BY GRAVITY FORCE
	WHEN ROOM TEMPERATURE RISES UP TO 71 C
	FIRE SIGNAL 24VDC 400mA ARE REQUIRED BY CONTRACTOR
ADDITIONAL ITEM	–


SHUTTER NO.	LOCATION	CLEAR WIDTH	CLEAR HEIGHT	MOTOR POSITION	QTY
FRS–01	–	3050mm	2550 mm	RIGHT	1

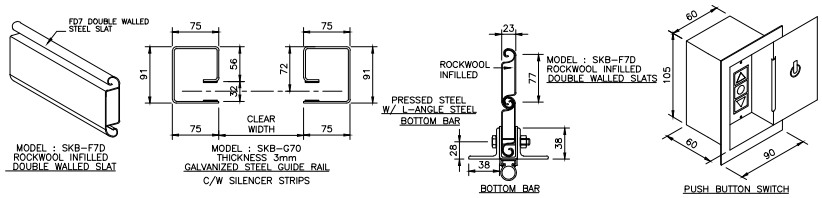


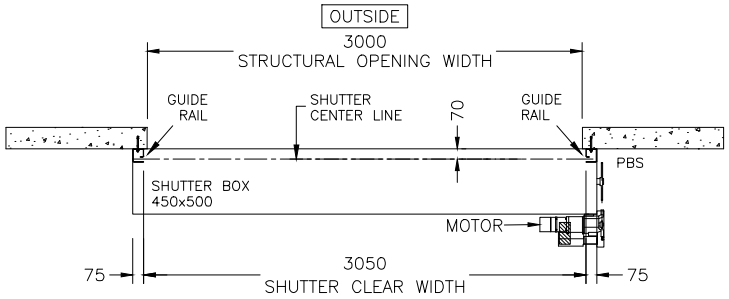

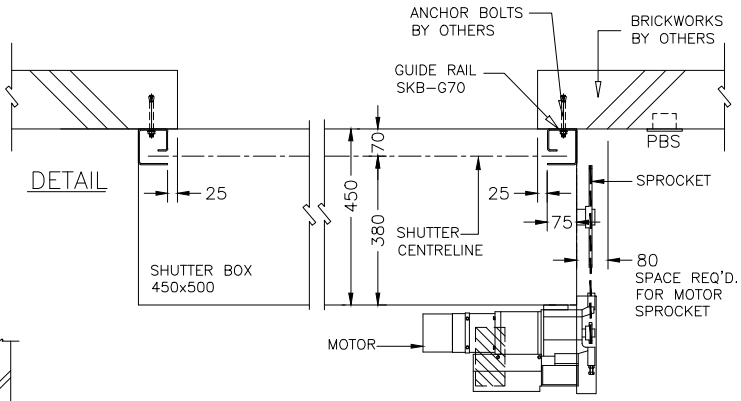

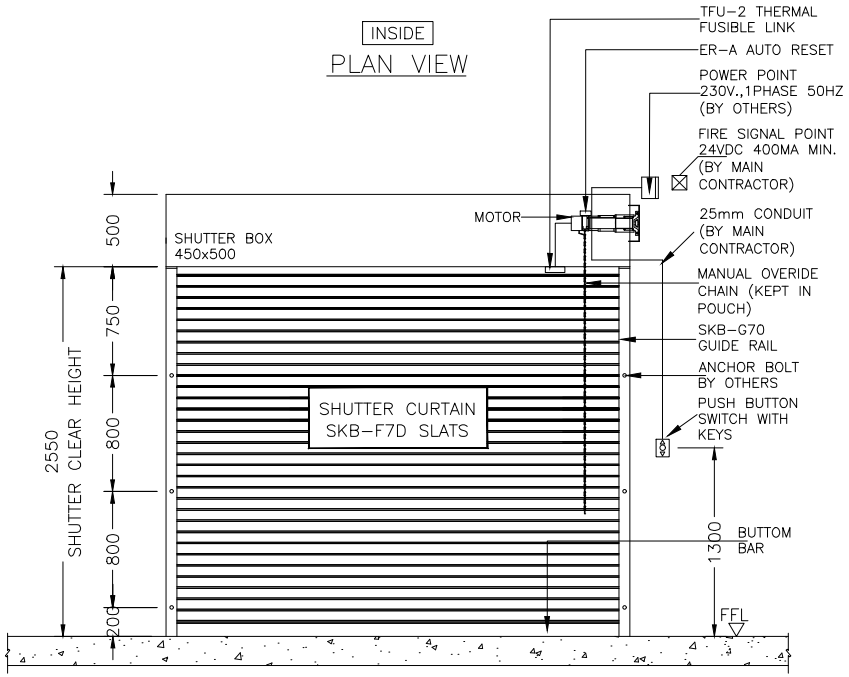

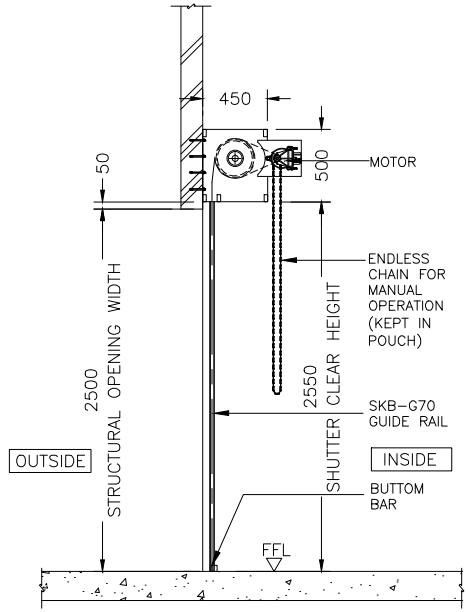

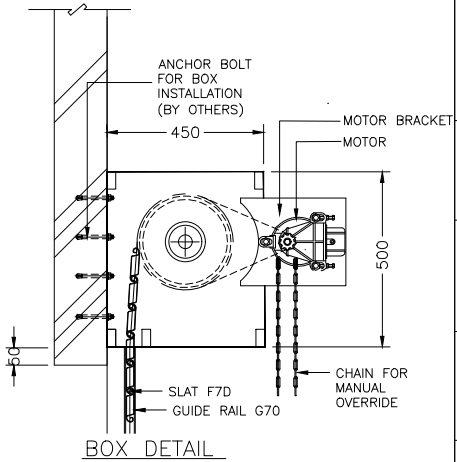

SHOP DRAWING

NO. | DATE: | AMENDMENTS:

DEVELOPER / LANDOWNER:

REV.

ARCHITECTURAL:

CONSULTANT :

MAIN CONTRACTOR :

INSTALLER :

MANUFACTURER:

SKB STORAGE INDUSTRIES SDN.BHD
Lot 22 Jalan Teknologi, Taman Sains Selangor,Kota Damansara
47810 Petaling Jaya,Selangor Darul Ehsan
Tel:(60) 3 6157 2277 Fax:(60) 3 6157 2211

PROJECT TITLE:

DRAWING TITLE:

SKB–A7 2HRS FIRE RATED ROLLER SHUTTER

DRAWN : ZUL	CHECKED : TM	DRAWING NO. :	REV :
SCALE : N.T.S	DATE : 03/10/2019	FRS/NIHVA/12/19/001	0