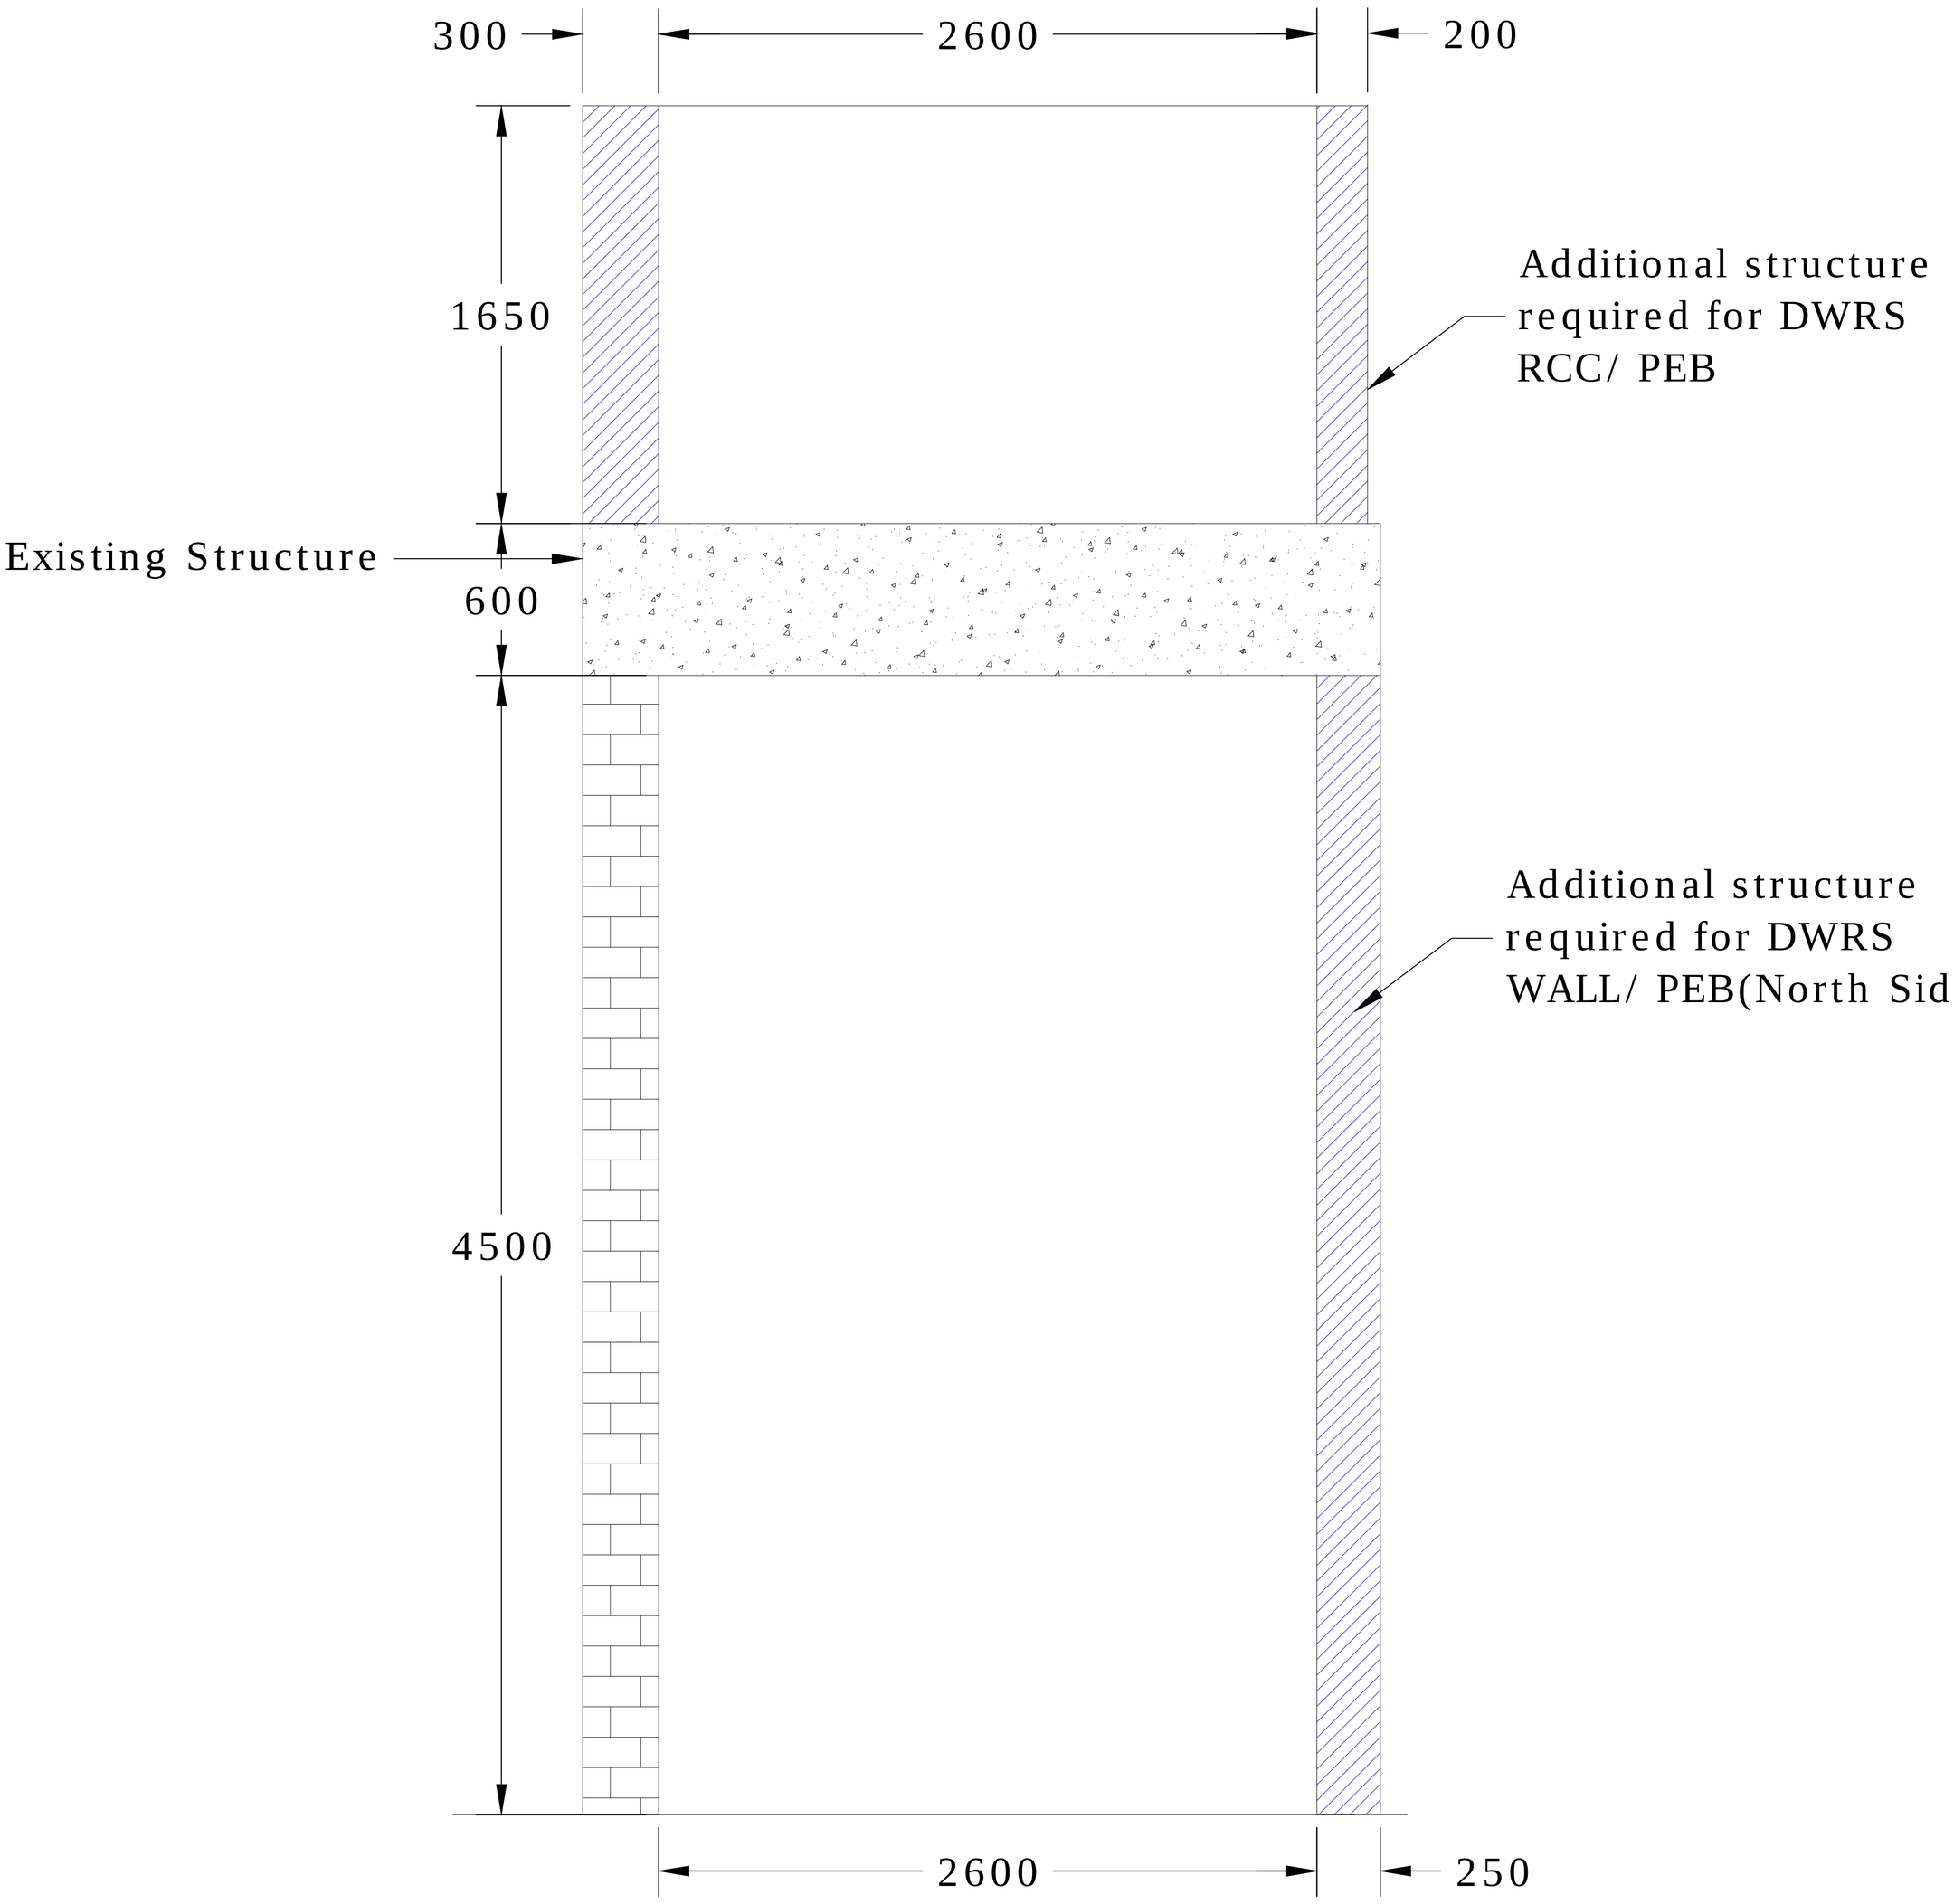

Inside Elevation

Additional Structure required at site for DWRS

Note- 1.Motor mounting will be at right side.
2.Need to construct additional structure as per drawing.

SHUTTER LOCATION- SHUTTER 4 STARTS FROM NORTH SIDE.

This drawing & design is the property of NIHVA TECHNOLOGIES. Not to be sold or copied to any other concern.

TITLE

STRUCTURE FOR DWRS 4

CLIENT APPROVAL

ALL DIMENSION ARE IN mm

	SIGN	DATE
DRAWN	OMKAR	30/05/17
CHECK	SAGAR P.	30/05/17
REV.		
APPRD.	R.K.	30/05/17
MFG		
Ref. No.		

NIHVA TECHNOLOGIES PVT. LTD.

NIHVA TECHNOLOGIES PVT. LTD. PUNE
Tel : 020 66304033
Email:- info@nihva.com
Website:- www.nihva.com

CLIENT - LUPIN

PROJECT - LUPIN

SITE - NAGPUR

DWG. NO. - NIHVA/17-18/0031/R01/4

SCALE: NTS | WT: | SHEET: 01 OF 01

If any queries contact : projects@nihva.com