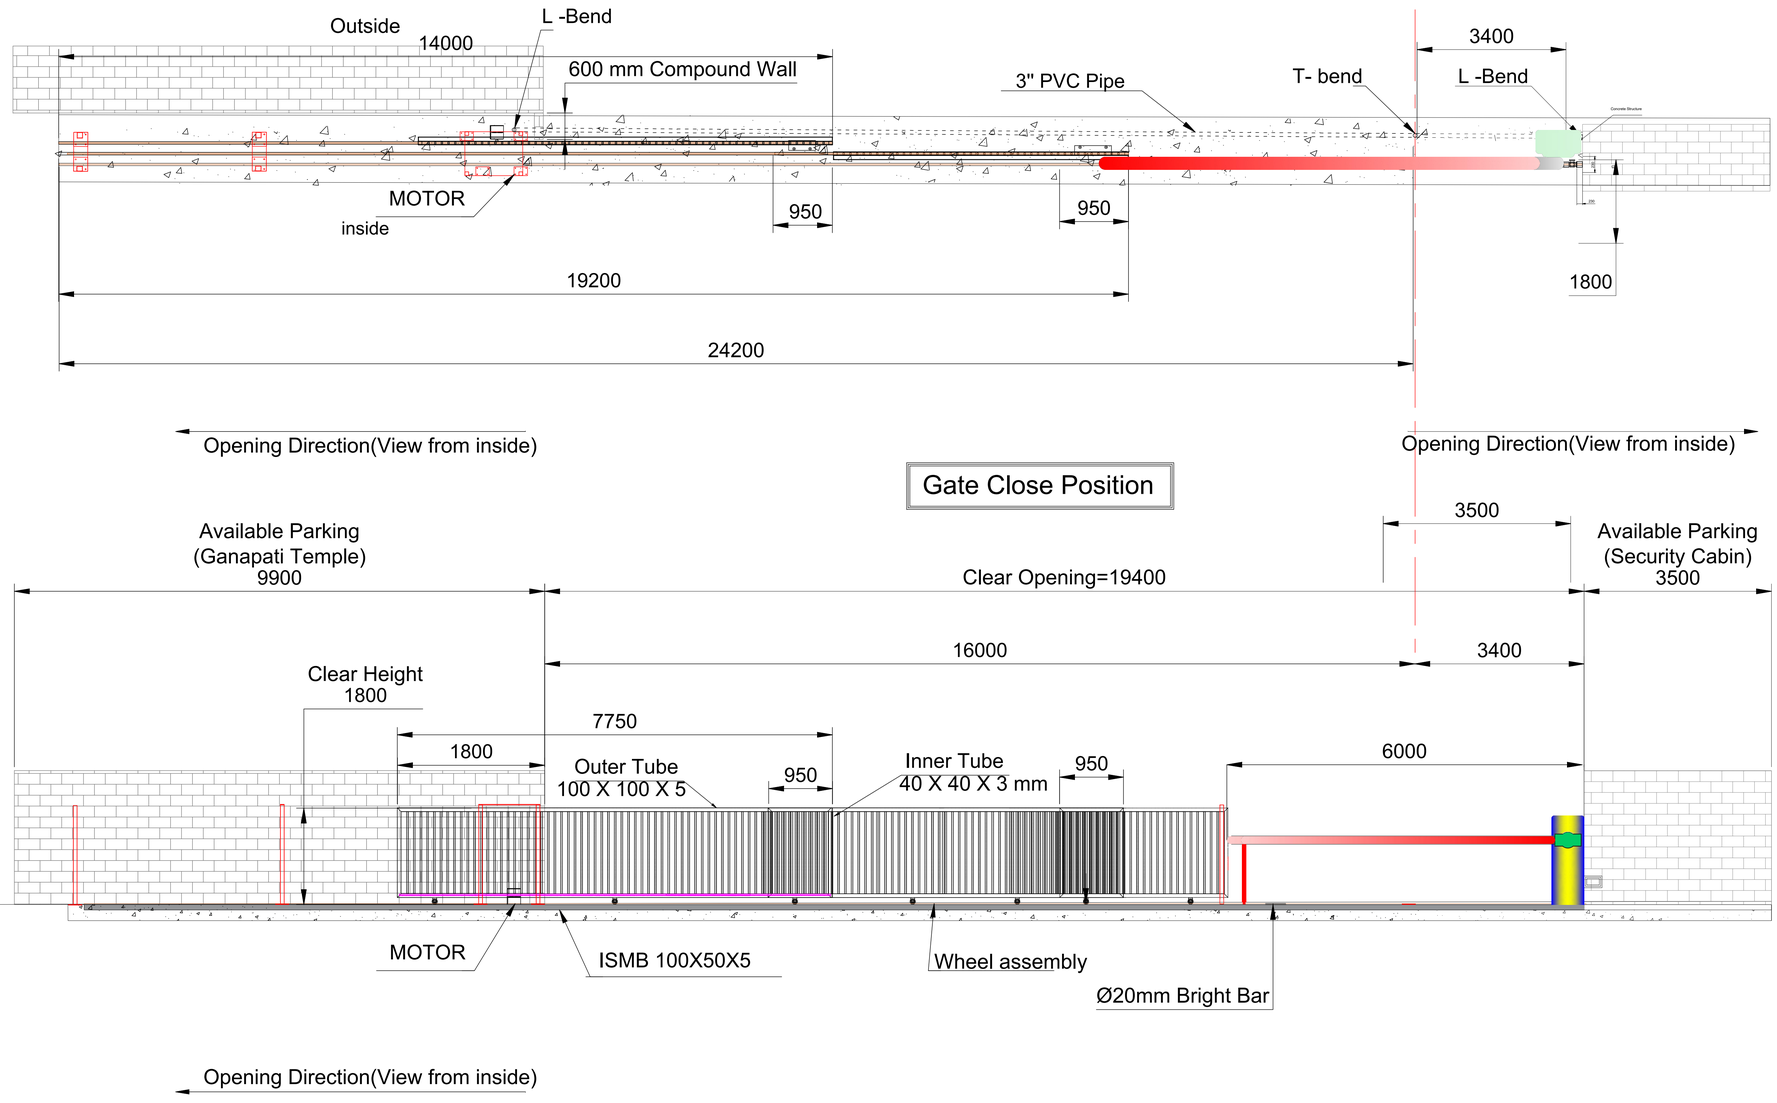

Outside
14000
L -Bend
600 mm Compound Wall
3" PVC Pipe
T- bend
3400
L -Bend
MOTOR
inside
950
950
19200
1800
24200
Opening Direction(View from inside)
Opening Direction(View from inside)
Gate Close Position
Available Parking
(Ganapati Temple)
9900
Clear Opening=19400
3500
Available Parking
(Security Cabin)
3500
16000
3400
Clear Height
1800
7750
1800
Outer Tube
100 X 100 X 5
950
Inner Tube
40 X 40 X 3 mm
950
6000
FFL
MOTOR
ISMB 100X50X5
Wheel assembly
Ø20mm Bright Bar
Opening Direction(View from inside)