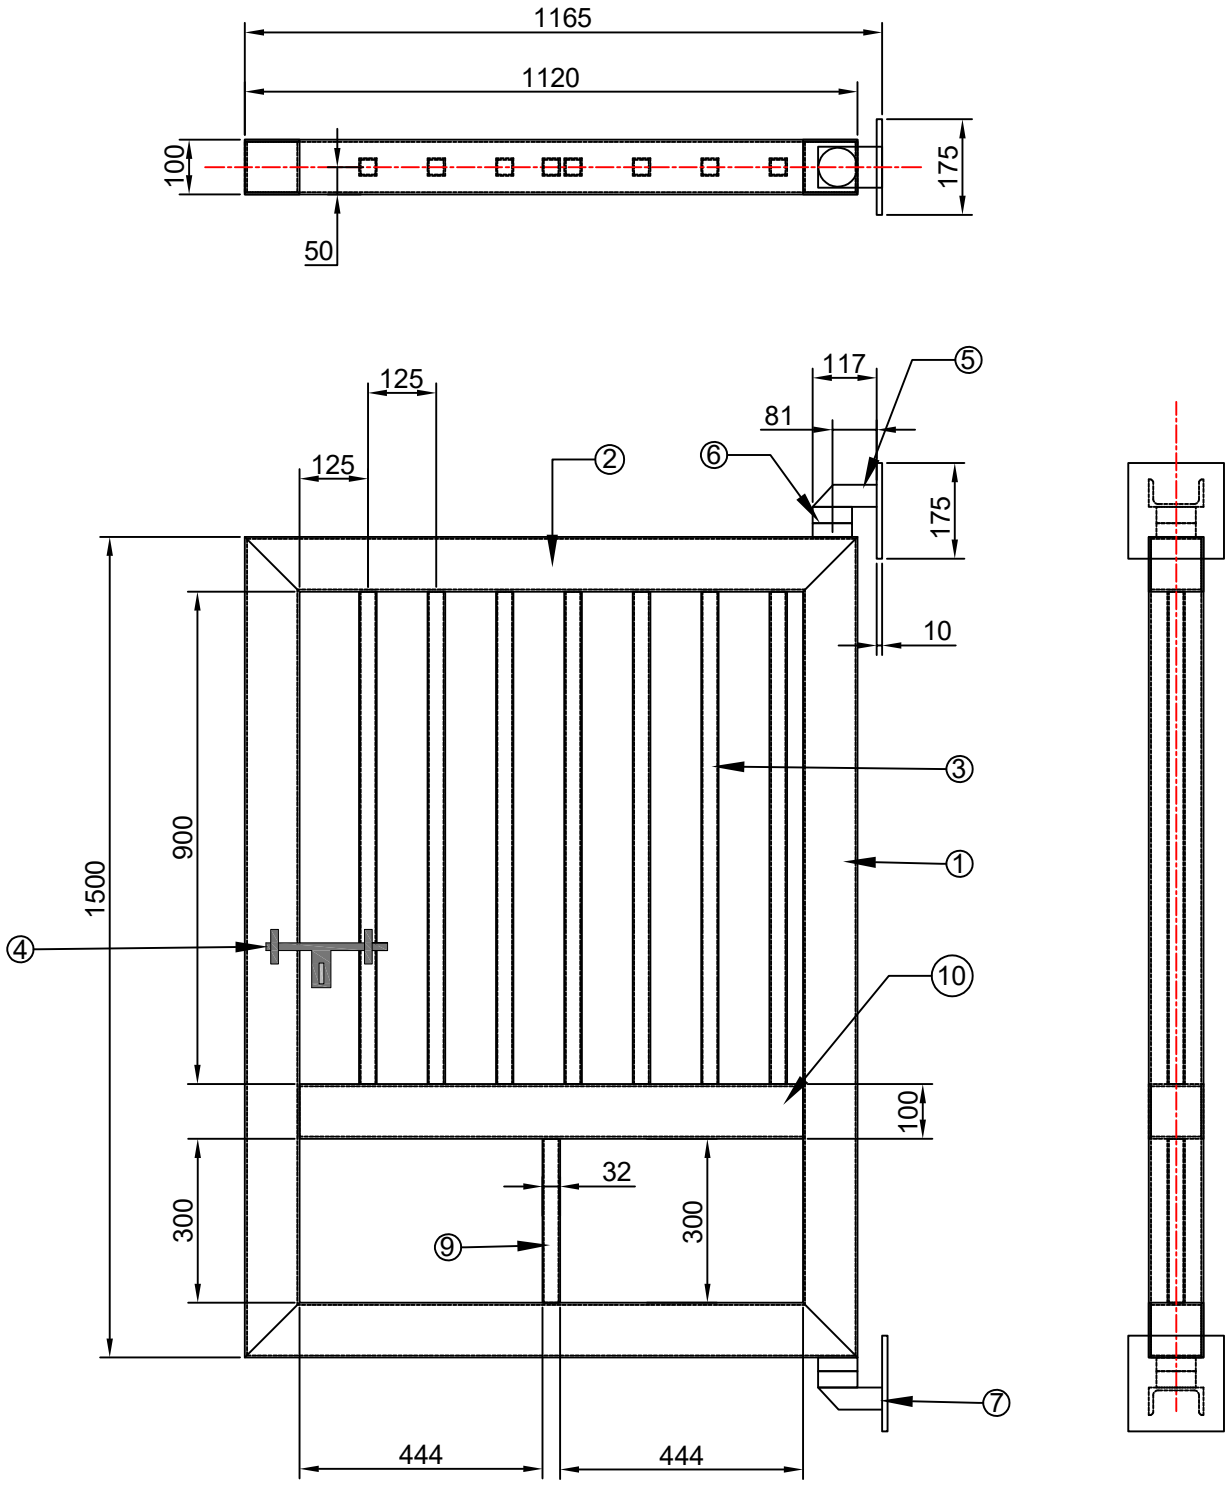


BOM			
SL NO.	DESCRIPTION	SPECIFICATION	QTY
1	MS SQ. TUBE	100X100X4X1500L	2NOS
2	MS SQ. TUBE	100X100X4X1120L	2NOS
3	MS SQ. TUBE	32X32X2.6X900L	7NOS
4	LOCK	ALDROP	1NO
5	SUPPORT CHANNEL	ISMC 100 X 50, 117L	2NOS
6	HINGE BEARING	3" MANUAL HINGE	2NOS
7	HINGE SUPPORT PLATE	175X175X10THK	2NOS
8	CLADDING	494X350X1.5	2NOS
9	MS SQ.TUBE	32X32X2.6X300L	1NO
10	MS SQ.TUBE	100X100X4X920L	1NO

This drawing & design is the property of NIHVA TECHNOLOGIES. Not to be sold or copied to any other concern.

TITLE:- WICKET GATE

NIHVA TECHNOLOGIES PVT. LTD. PUNE
Tel : 020 66304033
Email:- info@nihva.com
Website:- www.nihva.com

	NAME	DATE	SIGN
DRAWN	SUJATA	03/02/2022	
CHECK	G.PATIL	03/02/2022	
APPRD.	A.K	03/02/2022	

If any queries contact : design@nihva.com

ALL DIMENSION ARE IN mm

CLIENT -

LOCATION -

PRODUCT -WICKET GATE | QTY:-01NO

DWG NO:-NIHVA/21-22/MFG/019 | REV- 0

SCALE: NTS | SCALE:-- 1:1 | SHEET: 01 OF 01

Rev No.	Revision	Date	Revised By