

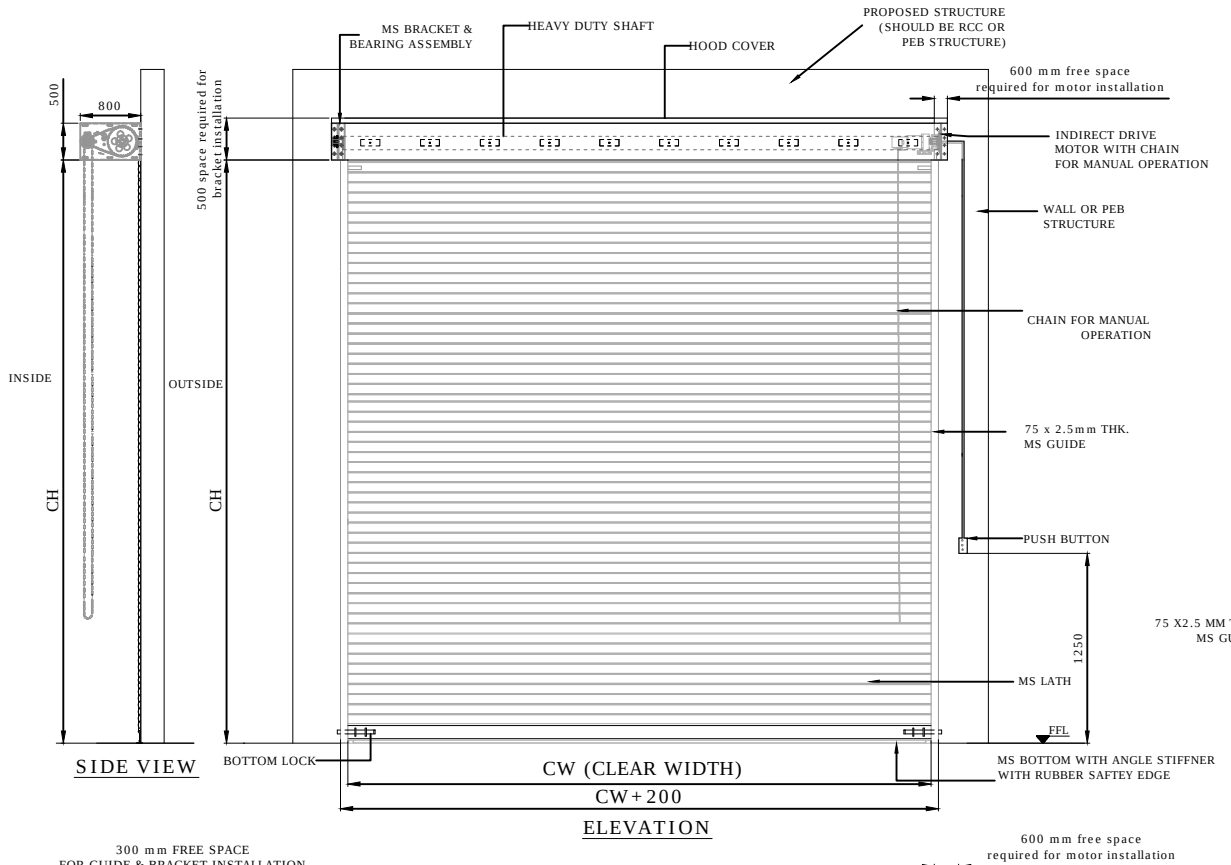


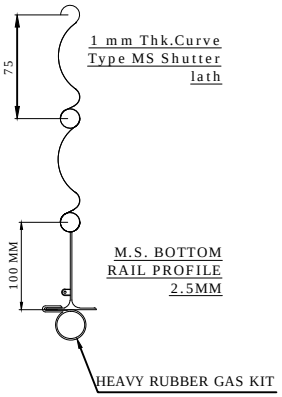

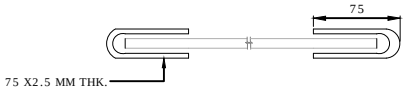

CLEAR WIDTH (CW)	CLEAR HEIGHT (CH)	QUANTITY
2500	3000	05 NOS

DIMENSION :

CLEAR WIDTH	CLEAR HEIGHT	QUANTITY
2500	3000	05 NOS

MATERIAL:

THICKNESS :

NOTE:
1.REQUIRED STRUCTURE FOR ROLLING SHUTTER WILL BE CLIENT'S SCOPE.
2.ONE COAT OF RED OXIDE PRIMER WILL BE GIVEN TO THE SHUTTER.
3.SINGLE PHASE. 3 CORE 1.5 SQ. CABLE REQUIRE AT SITE(CLIENT'S SCOPE).
4. FOR FINAL FINISH CLIENT SHOULD CONFIRM RAL COLOR SHADE.

NIHVA TECHNOLOGIES PVT. LTD.
NIHVA TECHNOLOGIES PVT. LTD. PUNE
Email:- info@nihva.com
Website:- www.nihva.com

TITLE:

MOTORIZED ROLLING SHUTTER

CLIENT'S APPROVAL :

CLIENT - SCON PROJECT.

PROJECT -ENZENE BIOSCIENCES LTD.

SITE LOCATION -CHAKAN.

DWG. NO. : NIHVA/17-18/0284. | REV. : 0

SCALE: NTS | WT: | SHEET:1 OF 1

		DATE	SIGN.
DRAWN	SURAJ	21-11-2017	
CHECK	OMKAR	21-11-2017	
APPRD.	SHEKHAR	21-11-2017	

If any queries contact : projects@nihva.com

NOTE: ALL DIMENSIONS ARE IN mm

THIS DRAWING & DESIGN IS THE PROPERTY OF NIHVA TECHNOLOGIES. NOT TO BE SOLD OR COPIED TO ANY OTHER CONCERN.