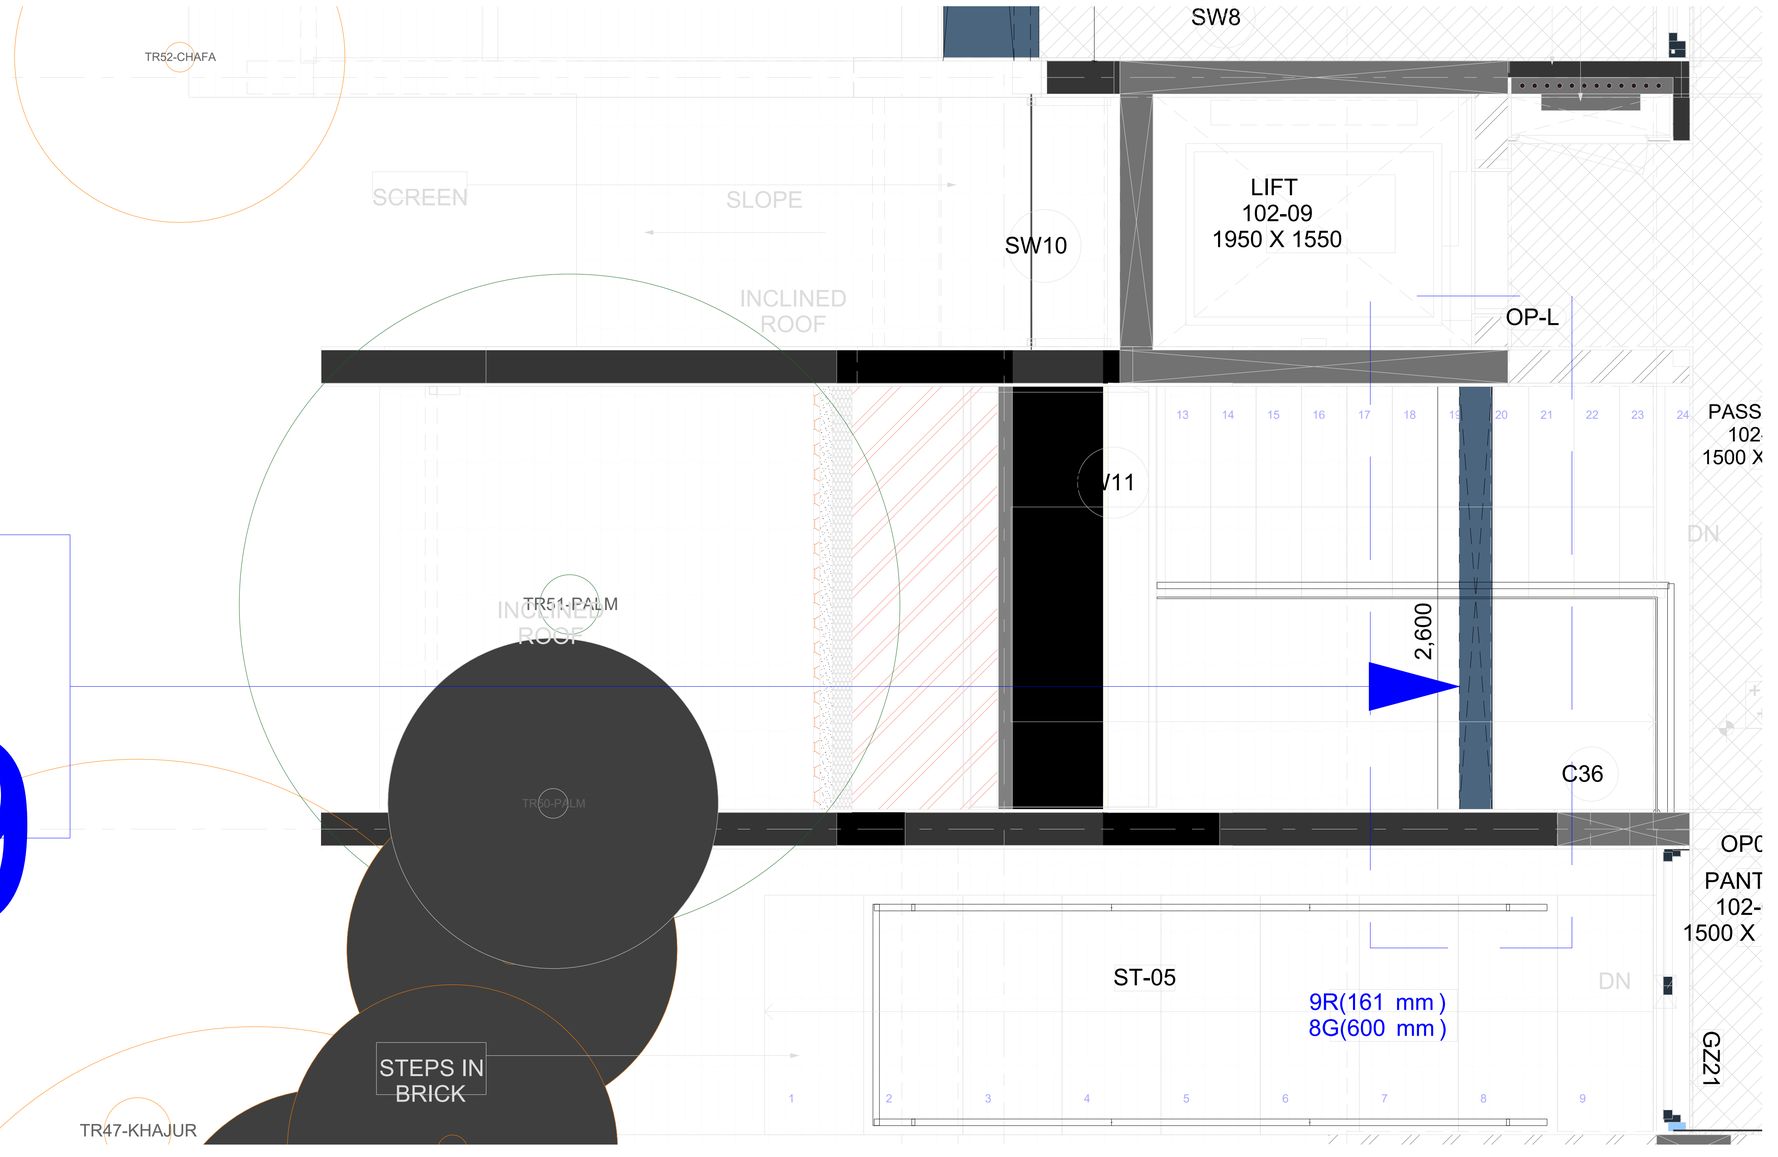
SK09


SW8
TR52-CHAFA
SCREEN
SLOPE
SW10
LIFT
102-09
1950 X 1550
INCLINED
ROOF
OP-L
PASS
102
1500 X
13
14
15
16
17
18
19
20
21
22
23
24
V11
DN
TR51-PALM
INCLINED
ROOF
2,600
C36
TR50-PALM
OPC
PANT
102-
1500 X
ST-05
9R(161 mm)
8G(600 mm)
DN
GZ21
STEPS IN
BRICK
1
2
3
4
5
6
7
8
9
TR47-KHAJUR