


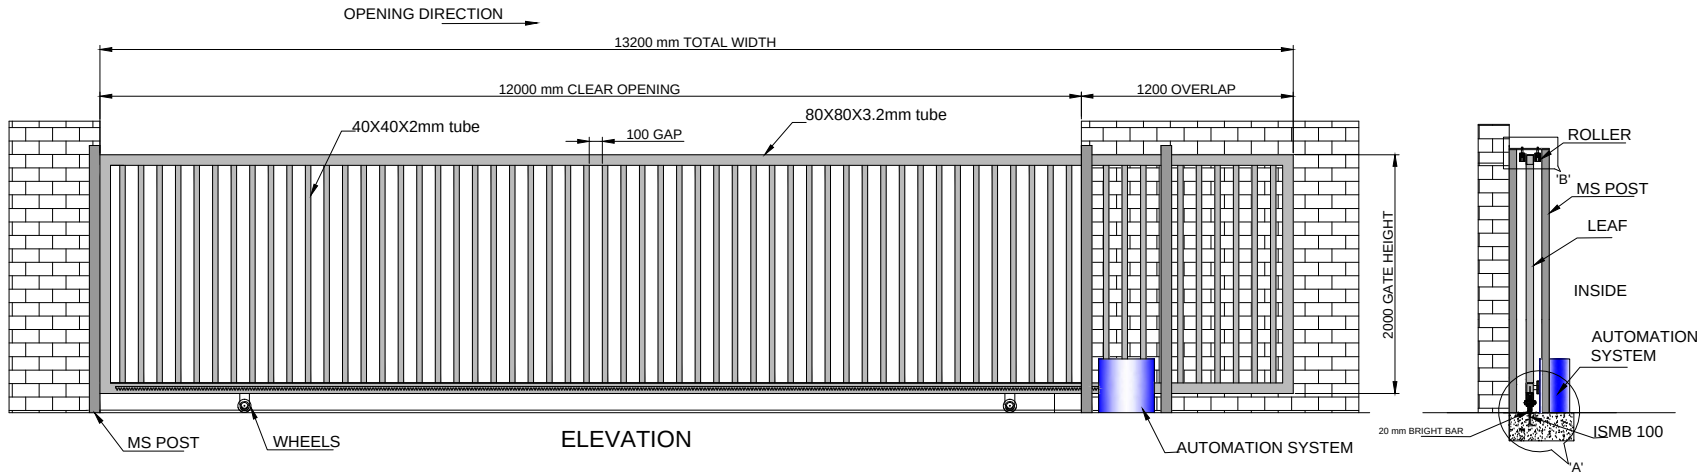


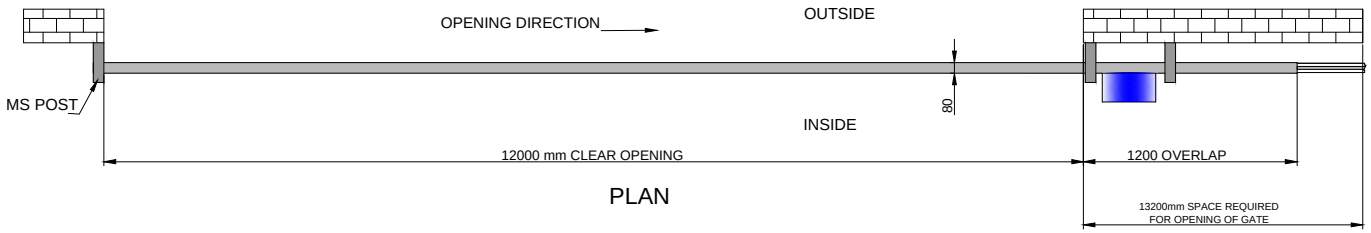

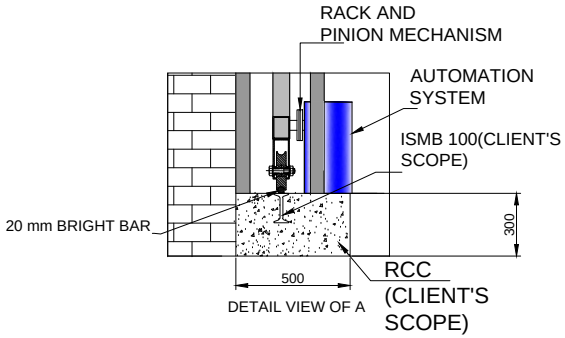

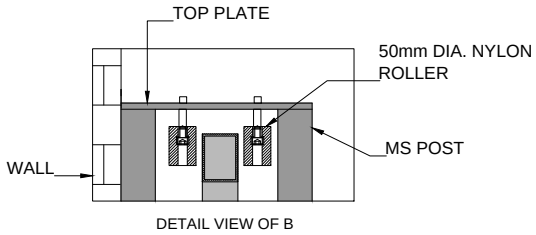

NOTE-
1. ALL REQUIRED CIVIL WORK WILL BE IN CLIENTS SCOPE.
3.GATE LEAF WILL BE IN TWO PARTS FOR TRANSPORTATION & WILL BE WELD TOGETHER ON SITE.

TOLERANCE - ±10mm

TOTAL NO OF POST ARE 05.

SR NO	TUBE SPECIFICATION	
1	80X80X3.2mm	OUTER FRAME
2	40X40X2mm	INNER PATTERN
3	80X80X3.2mm	FOR MS POST

CLEAR WIDTH	CLEAR HEIGHT	QUANTITY
12000	2000	01 NOS

This drawing & design is the property of NIHVA TECHNOLOGIES. Not to be sold or copied to any other concern.

TITLE: SLIDING GATE

NIHVA TECHNOLOGIES PVT. LTD.

NIHVA TECHNOLOGIES PVT. LTD. PUNE
Tel : 020 66304033
Email:- info@nihva.com
Website:- www.nihva.com

	NAME	SIGN	DATE
DRAWN	A.K.		21.01.2019
CHECK	P.A.		21.01.2019
APPRD.	R.D.		21.01.2019

CLIENT - ESR PUNE
PROJECT - BMW
SITE LOCATION - CHAKAN, PUNE.
If any queries contact : design@nihva.com
DWG. NO. : NIHVA/18-19/0251 REV- 0
ALL DIMENSION ARE IN mm
SCALE: NTS WT: SHEET: 01 OF 01