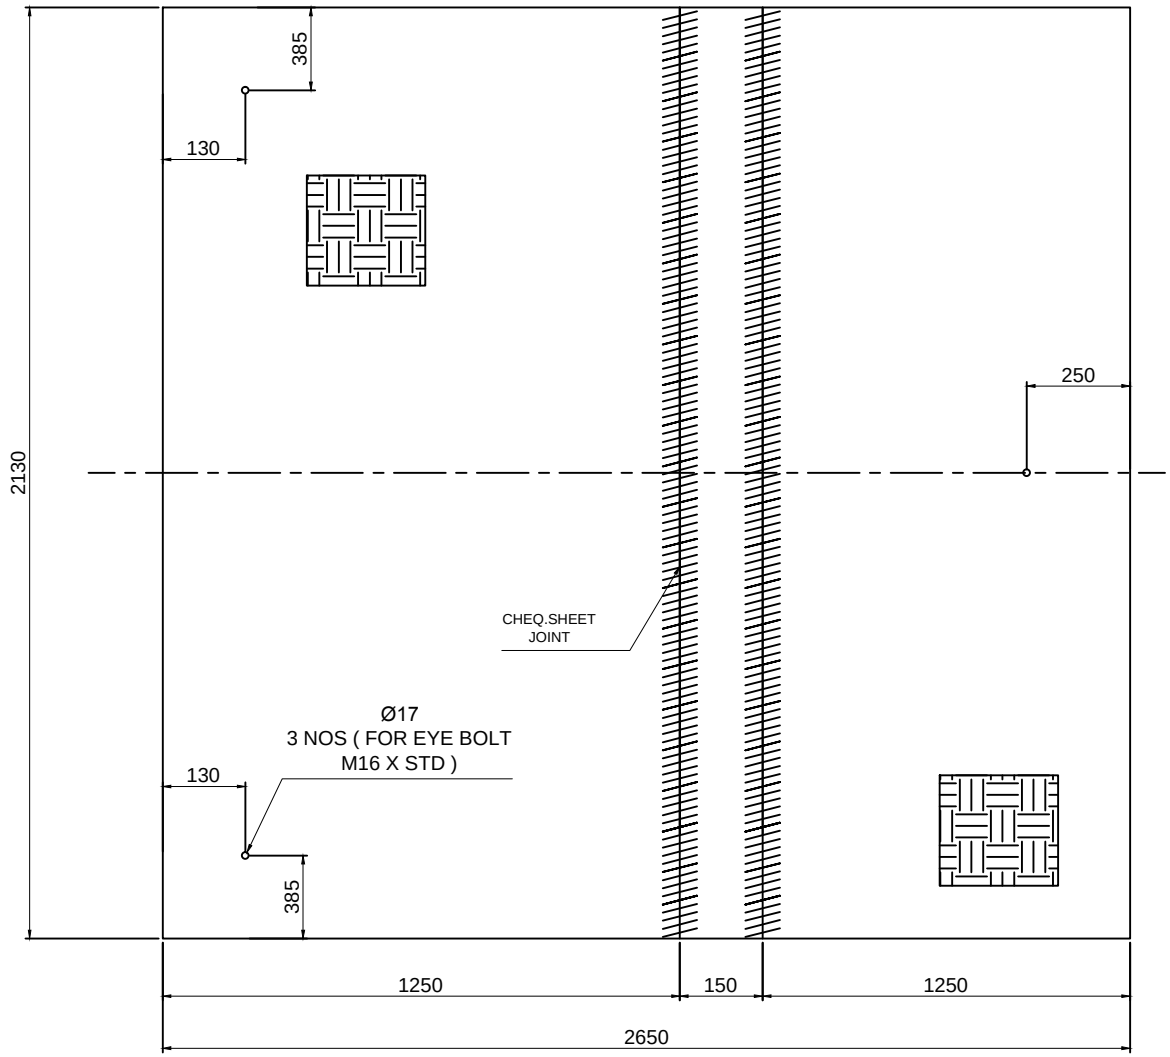


1. CHEQ.SHEET 1250 X 8 THK X 2130L = 2 NOS
2. CHEQ.SHEET 150 X 8 THK X 2130L = 1 NO

This drawing & design is the property of NIHVA TECHNOLOGIES. Not to be sold or copied to any other concern.

TITLE				
DECK CHEQ.SHEET				NIHVA TECHNOLOGIES PVT. LTD.
	NAME	SIGN	DATE	
DRAWN	P.V.A		20.06.2019	CLIENT -
CHECK	V.M.T		20.06.2019	PROJECT - NDL451
APPRD.				SITE LOCATION -
If any queries contact : design@nihva.com				DWG. NO. : NIHVA/19-20/VDR/074
ALL DIMENSION ARE IN mm				SCALE: NTS / WT: / REV- 00

NIHVA TECHNOLOGIES PVT. LTD. PUNE
Tel : 020 66304033
Email:- info@nihva.com
Website:- www.nihva.com