

DRAWING

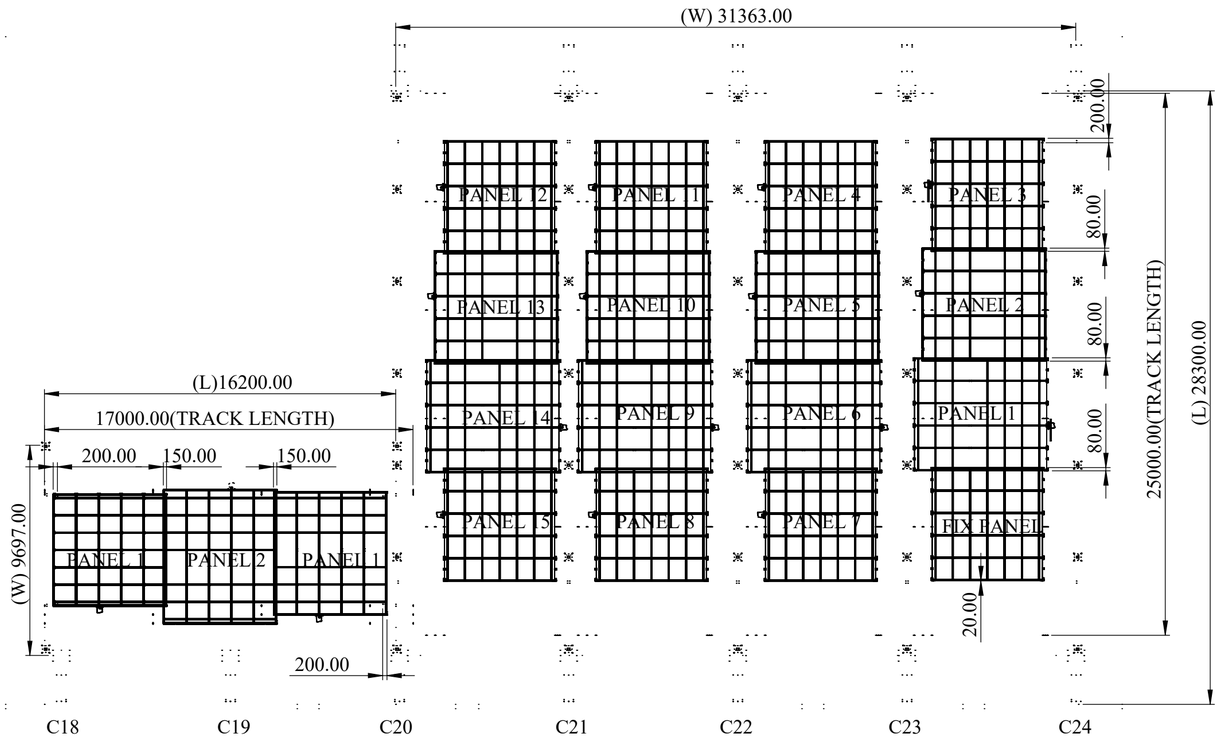


SPA SHOP UNIT

VWM & HWM SHOP UNIT


T.V.

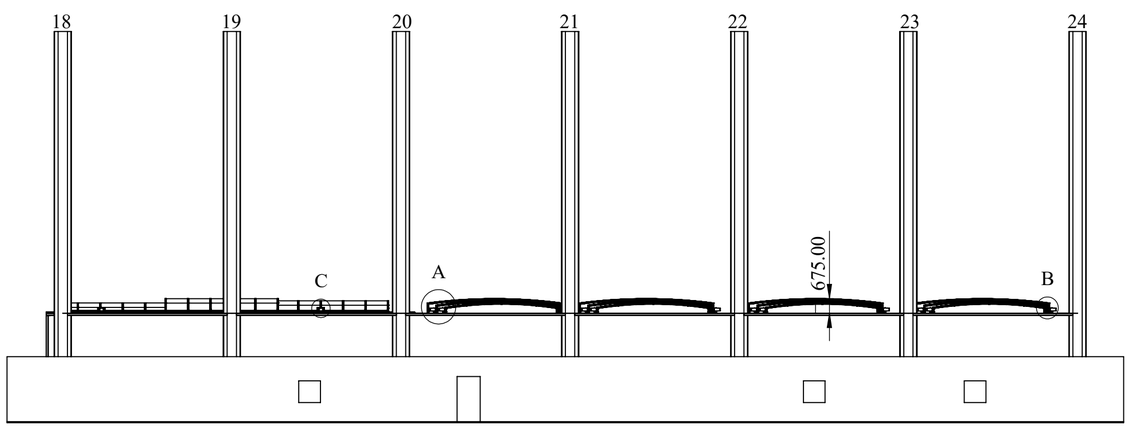


F.V.

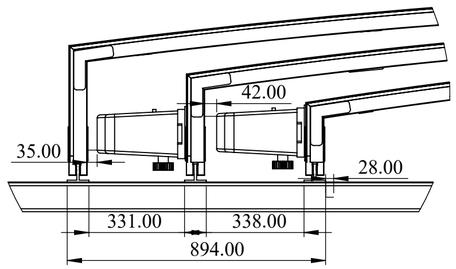

DETAIL A
SCALE 1 : 15

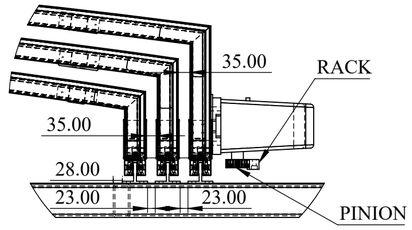

DETAIL B
SCALE 1 : 13

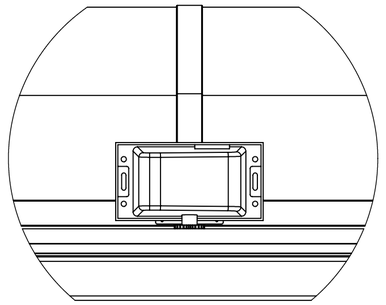

DETAIL C
SCALE 1 : 10

MOTOR

REV DESCRIPTION	DATE	REV NO
	19-06-2026	REV 00
1.		

NOTE :

SPECIAL INSTRUCTION'S :

This drawing & design is the property of NIHVA TECHONOLOGIES PVT. LTD. Not to be sold or copied to any other concern.

TITLE - SPA SHOP

DWG NO - NTPL-002-PM-01

NIHVA TECHNOLOGIES PVT.LTD.PUNE
Website - www.nihva.com

	NAME	SIGNATURE	DATE
DRAWN	V.W.		19-06-2026
CHK'D	S.P.		20-06-2026
APPV'D	V.T.		20-06-2026

PRODUCT - C-SHAPE RETRACTABLE ROOF

PROJECT NO - NTPL-002-PM | REVISION - 00

SITE LOCATION-HYDRABAD | WEIGHT -

MATRIAL - | QTY - 1


If any queries contact - design2@nihva.com

ALL DIMENSION ARE IN mm | A2

PROJECTION METHOD:

SCALE :


DRAWING

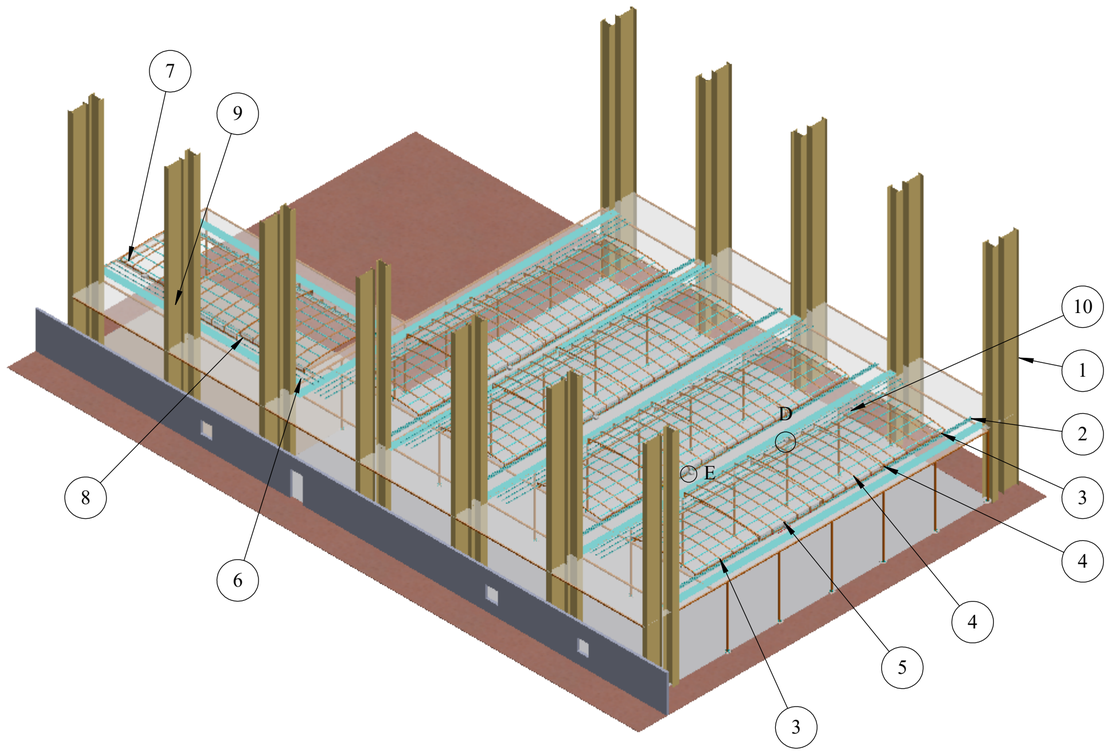

ISO VIEW


ITEM NO.	PART NUMBER	DESCRIPTION	QTY.
1	BASE STRUCTURE ASSEMBLY VWM & HWM UNIT & SPA SHOP UNIT	CLIENT SCOPE	1
2	GUIDE RAILS-T75-1B	STD (5 M LENGTH)	120
3	PANEL ASM NO - 1	AL FRAME	8
4	PANEL ASM NO - 2	AL FRAME	4
5	PANEL ASM NO - 3	AL FRAME	4
6	GUIDE RAILS-T75-1B	STD (5 M LENGTH)	22
7	PANEL ASM NO - 1 SPA	AL FRAME	1
8	PANEL ASM NO - 2 - SPA	AL FRAME	1
9	PANEL ASM NO - 3- SPA	AL FRAME	1
10	RACK	STD (1 M LENGTH)	225

REV DESCRIPTION	DATE	REV NO
	19-06-2026	REV 00
1.		

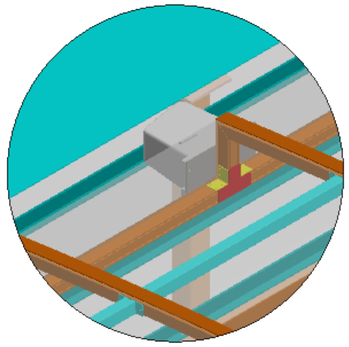

DETAIL D
SCALE 1 : 15

MOTOR MOUNTING

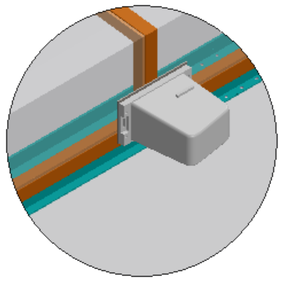

DETAIL E
SCALE 1 : 15

MOTOR MOUNTING

NOTE :

SPECIAL INSTRUCTION'S :

This drawing & design is the property of NIHVA TECHONOLOGIES PVT. LTD. Not to be sold or copied to any other concern.

TITLE - SPA SHOP

DWG NO - NTPL-002-PM-01

NIHVA Technologies Pvt. Ltd.

NIHVA TECHNOLOGIES PVT.LTD.PUNE
Website - www.nihva.com

	NAME	SIGNATURE	DATE
DRAWN	V.W.		19-06-2026
CHK'D	S.P.		20-06-2026
APPV'D	V.T.		20-06-2026

PRODUCT - C-SHAPE RETRACTABLE ROOF
PROJECT NO - NTPL-002-PM | REVISION - 00
SITE LOCATION-HYDRABAD | WEIGHT -
MATRIAL - | QTY - 1


If any queries contact - design2@nihva.com

ALL DIMENSION ARE IN mm | A2


PROJECTION METHOD:

SCALE :


DRAWING

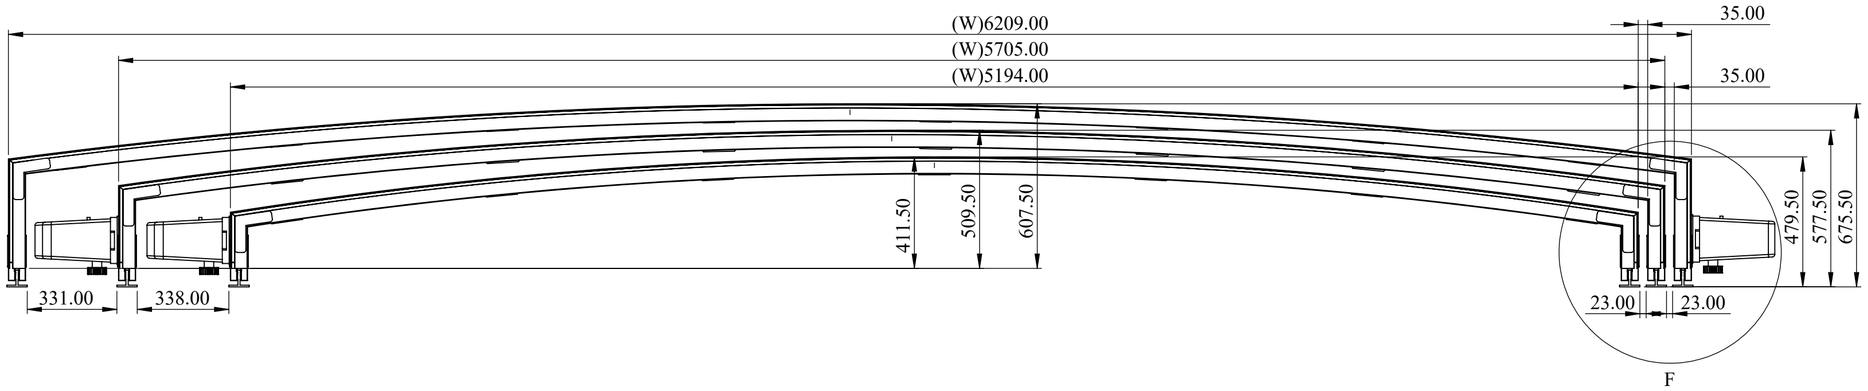

REV DESCRIPTION	DATE	REV NO
	19-06-2026	REV 00
1.		

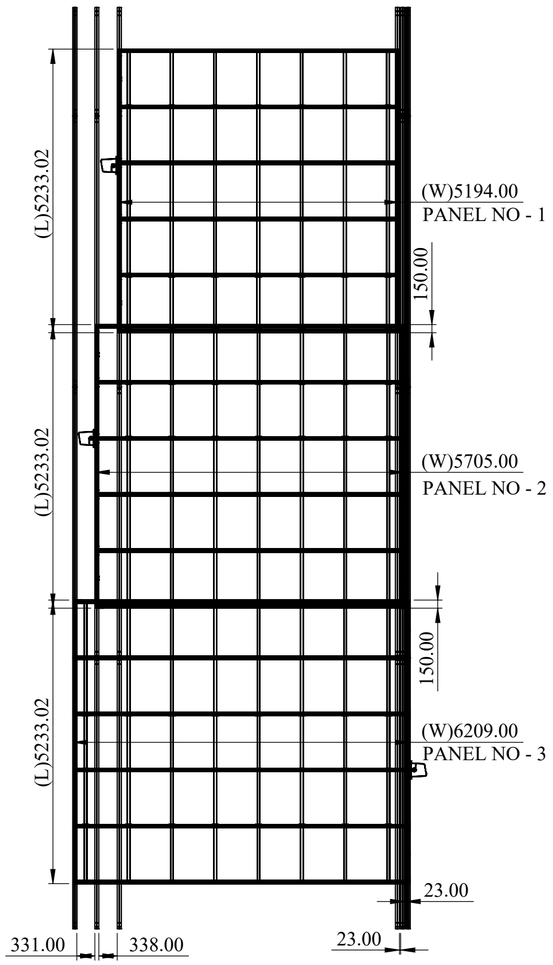

ITEM NO.	PART NUMBER	DESCRIPTION	QTY.
1	GUIDE RAILS-T75-1B	STD (5 M LENGTH)	18
2	GUIDE RAILS-T75-1B	STD (5 M LENGTH)	6
3	PANEL ASM NO - 1 SPA	AL FRAME	1
4	PANEL ASM NO - 2 - SPA	AL FRAME	1
5	PANEL ASM NO - 3- SPA	AL FRAME	1

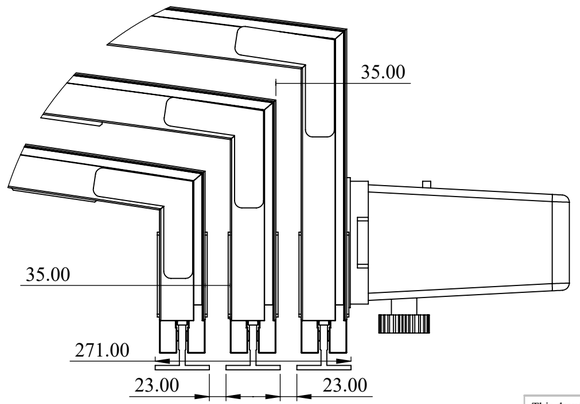

DETAIL F
SCALE 1 : 6

NOTE :

THREE PANEL ASSEMBLY

SPECIAL INSTRUCTION'S :

This drawing & design is the property of NIHVA TECHONOLOGIES PVT. LTD. Not to be sold or copied to any other concern.

TITLE - SPA SHOP UNIT


DWG NO - NTPL-002-PM-01

NIHVA TECHNOLOGIES PVT.LTD.PUNE
Website - www.nihva.com

	NAME	SIGNATURE	DATE
DRAWN	V.W.		19-06-2026
CHK'D	S.P.		20-06-2026
APPV'D	V.T.		20-06-2026

PRODUCT - C-SHAPE RETRACTABLE ROOF
PROJECT NO - NTPL-000-PM
REVISION - 00
SITE LOCATION-HYDRABAD
WEIGHT -
MATRIAL -
QTY - 1
If any queries contact - design2@nihva.com
PROJECTION METHOD:
SCALE :
ALL DIMENSION ARE IN mm
A2


DRAWING

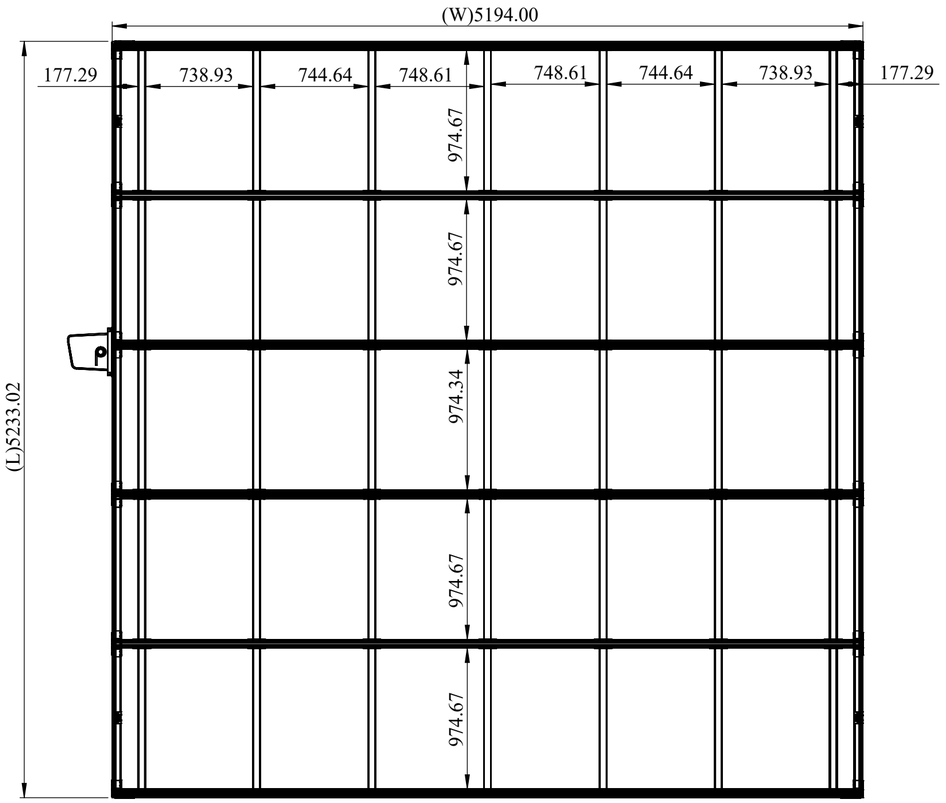


T.V.

ITEM NO.	PART NUMBER	DESCRIPTION	QTY.
1	PANEL NO - 01 - SPA	AL PROFILE	1
2	BEARING BLOCK ASM _ T75_1B. - SPA	AL	4
3	INTERMEDIATE SUPPORT TUBE ASM . - SPA	AL SQ TUBE - 50X50X1.5 MM THK	35
4	MOTOR BASE PLATE - SPA	AL/MS	1
5	NICE RB 0.8T	NICE	1
6	T PLATE	SS304 -117.5X156X3 MM THK	16
7	L PLATE	SS304- 91X106X3 MM THK	8
8	L ANGLE PLATE	SS304 - 60X60X3 MM	20
9	L ANGLE WELDING CORNER JOINING PLATE	AL WELDING JOINING PLATE	24

REV DESCRIPTION	DATE	REV NO
	19-06-2026	REV 00
1.		

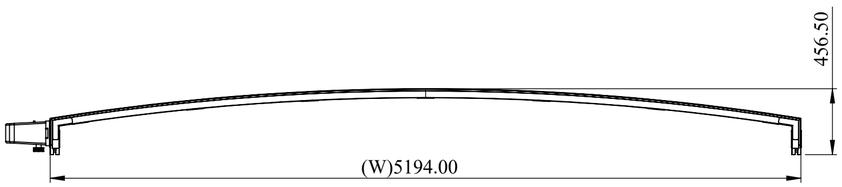

F.V.

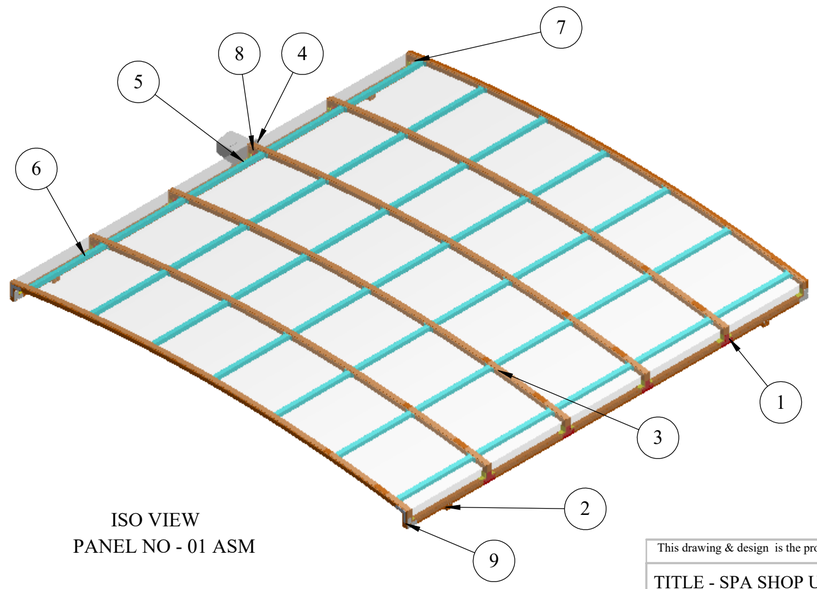

ISO VIEW
PANEL NO - 01 ASM

NOTE :

NAME : PANEL NO - 1 ASM
PROFILE : AL GNTOO6
QTY : 01 NOS.

SPECIAL INSTRUCTION'S :

This drawing & design is the property of NIHVA TECHONOLOGIES PVT. LTD. Not to be sold or copied to any other concern.

TITLE - SPA SHOP UNIT

DWG NO - NTPL-002-PM-01


NIHVA TECHNOLOGIES PVT.LTD.PUNE
Website - www.nihva.com

	NAME	SIGNATURE	DATE
DRAWN	V.W.		19-06-2026
CHK'D	S.P.		20-06-2026
APPV'D	V.T.		20-06-2026

PRODUCT - C-SHAPE RETRACTABLE ROOF
PROJECT NO - NTPL-002-PM | REVISION - 00
SITE LOCATION-HYDRABAD | WEIGHT -
MATRIAL - | QTY - 1


If any queries contact - design2@nihva.com
ALL DIMENSION ARE IN mm | A2
PROJECTION METHOD:
SCALE :

DRAWING

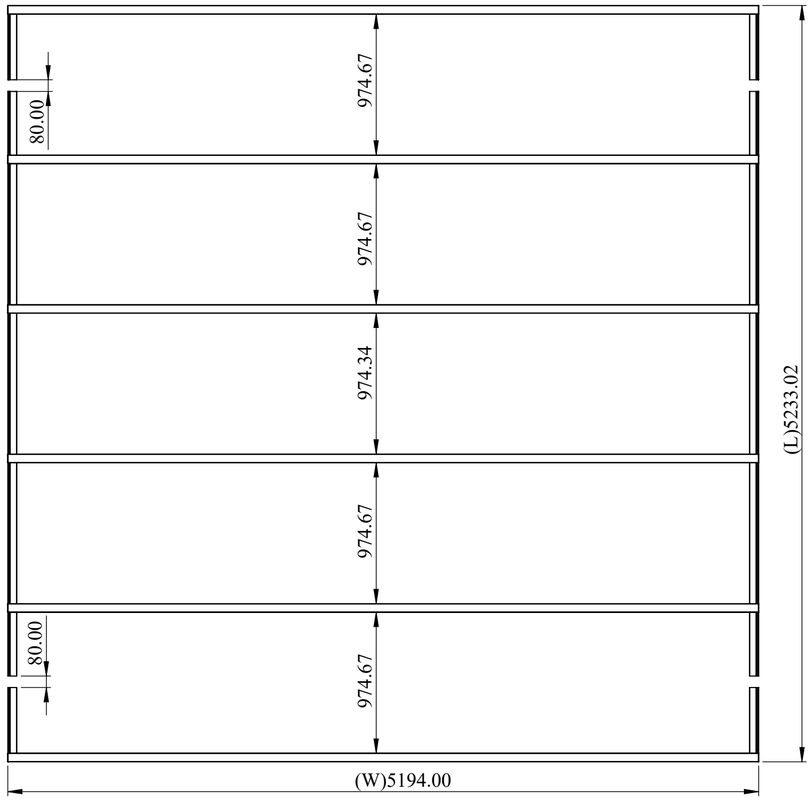


T.V.

ITEM NO.	PART NUMBER	DESCRIPTION	QTY.
1	PANEL NO - 01 - SPA	AL PROFILE	1

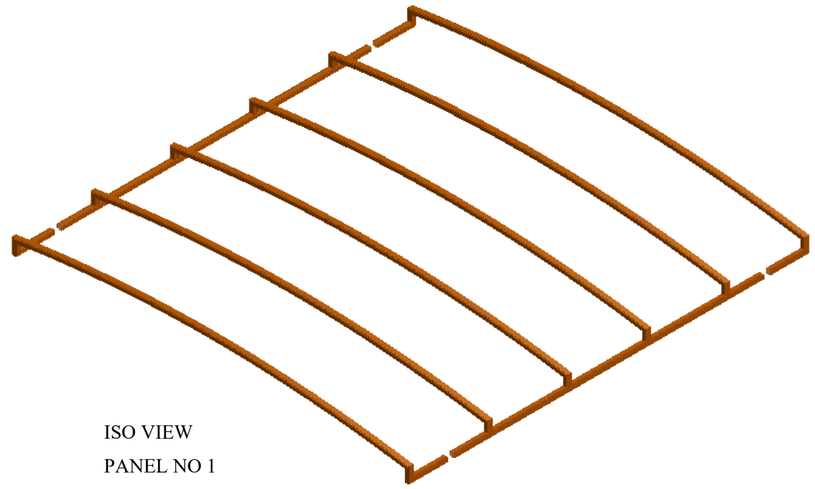



ISO VIEW
PANEL NO 1

REV DESCRIPTION	DATE	REV NO
	19-06-2026	REV 00
1.		

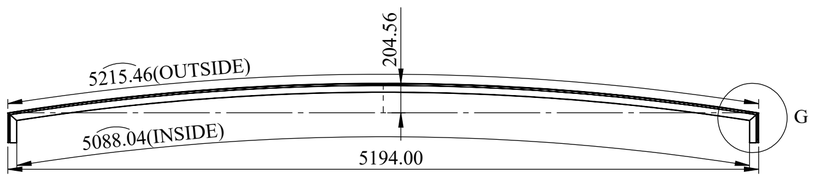


F.V.

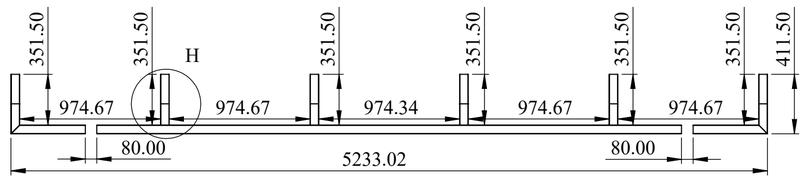

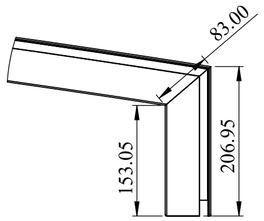

DETAIL G
SCALE 1 : 6

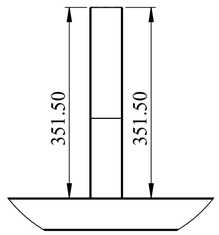

DETAIL H
SCALE 1 : 8

NOTE :


NAME : PANEL NO - 1
PROFILE : AL GNTOO6 (60X63)
QTY : 01 NOS

SPECIAL INSTRUCTION'S :


This drawing & design is the property of NIHVA TECHONOLOGIES PVT. LTD. Not to be sold or copied to any other concern.

TITLE - SPA SHOP UNIT				NIHVA TECHNOLOGIES PVT.LTD.PUNE Website - www.nihva.com	
DWG NO - NTPL-002-PM-01					
	NAME	SIGNATURE	DATE	PRODUCT - C-SHAPE RETRACTABLE ROOF	
DRAWN	V.W.		19-06-2026	PROJECT NO - NTPL-002-PM	REVISION - 00
CHK'D	S.P.		20-06-2026	SITE LOCATION-HYDRABAD	WEIGHT -
APPV'D	V.T.		20-06-2026	MATRIAL -	QTY - 1
If any queries contact - design2@nihva.com				PROJECTION METHOD:	SCALE :
ALL DIMENSION ARE IN mm			A2		SHEET 5 OF 19


DRAWING

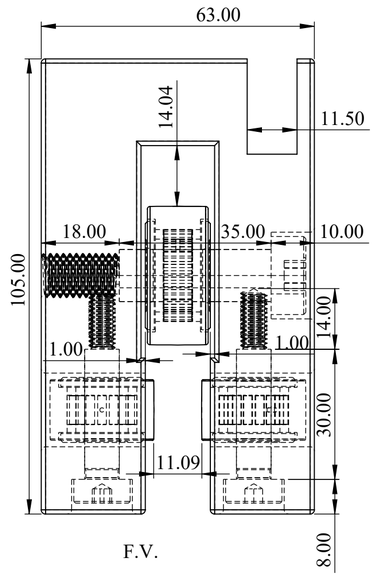

F.V.

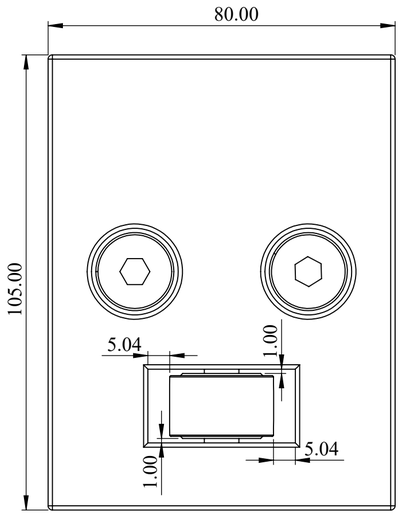


S.V.

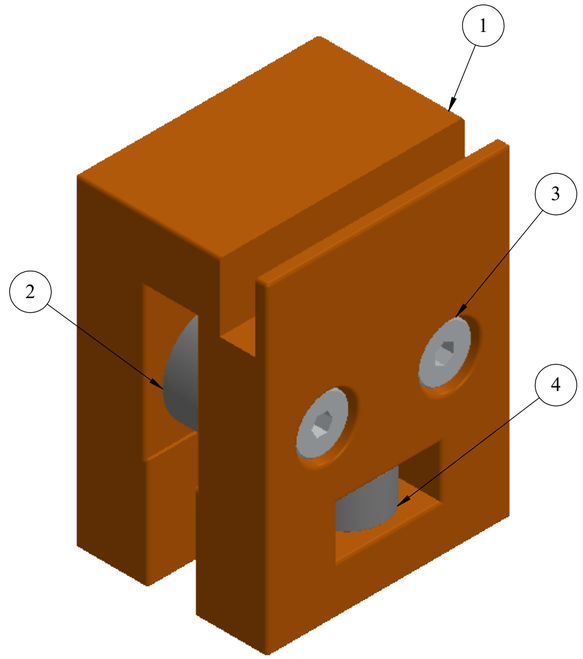

ISO VIEW

REV DESCRIPTION	DATE	REV NO
	19-06-2026	REV 00
1.		

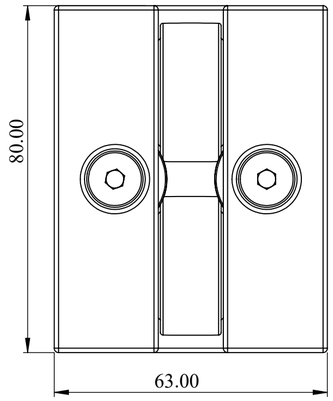

B.V.

ITEM NO.	PART NUMBER	DESCRIPTION	QTY.
1	BEARING BLOCK (T75-1B)	80X105X63 MM (VMC PART)	1
2	BEARING SKF_NATR 12	SKF (STD)	2
3	SHOULDER BOLT NATR 12.	SS	2
4	BEARING SKF_NATR 8	SKF(STD)	2
5	SHOULDER BOLT NATR - 8 x 30 --- N	SS	2

NOTE :

NAME : BEARING BLOCK HOUSING ASSEMBLY
SIZE : W63 X L80 X H105 MM
QTY FOR 1 PANEL : 4 NOS
QTY FOR 3 PANEL : 12 NOS

SPECIAL INSTRUCTION'S :

This drawing & design is the property of NIHVA TECHONOLOGIES PVT. LTD. Not to be sold or copied to any other concern.

TITLE - SPA SHOP UNIT

DWG NO - NTPL-002-PM-01


NIHVA TECHNOLOGIES PVT.LTD.PUNE
Website - www.nihva.com


	NAME	SIGNATURE	DATE	
DRAWN	V.W.		19-06-2026	PRODUCT - C-SHAPE RETRACTABLE ROOF
CHK'D	S.P.		20-06-2026	PROJECT NO - NTPL-002-PM / REVISION - 00
APPV'D	V.T.		20-06-2026	SITE LOCATION-HYDRABAD / WEIGHT -
				MATRIAL - / QTY - 1

If any queries contact - design2@nihva.com

ALL DIMENSION ARE IN mm | A2 | PROJECTION METHOD: | SCALE :


DRAWING

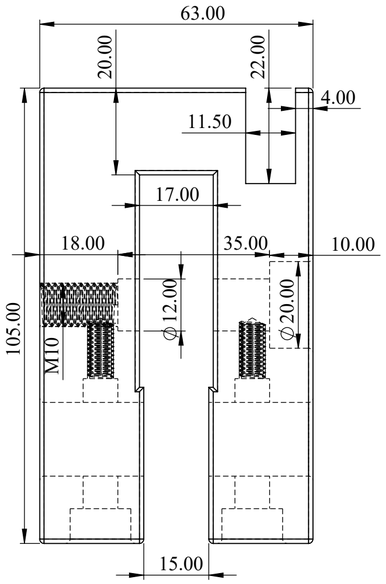


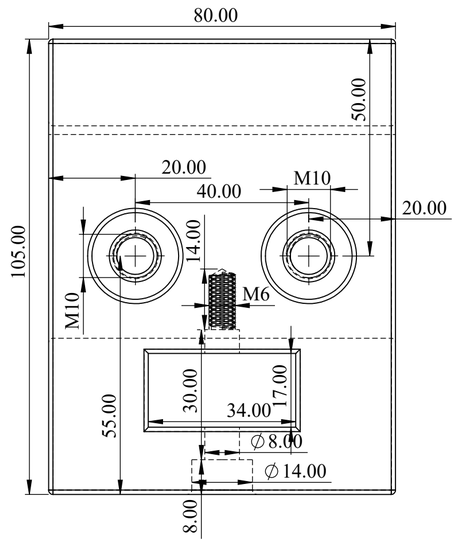

ITEM NO.	PART NUMBER	DESCRIPTION	QTY.
1	BEARING BLOCK (T75-1B)	80X105X63 MM (VMC PART)	12

REV DESCRIPTION	DATE	REV NO
	19-06-2026	REV 00
1.		

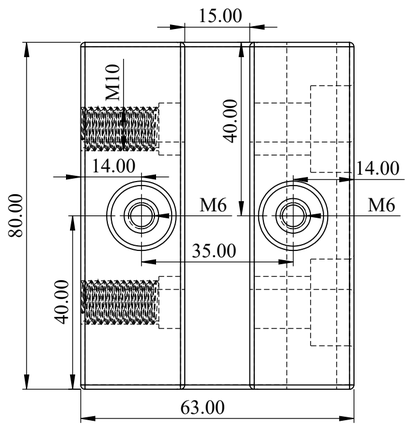

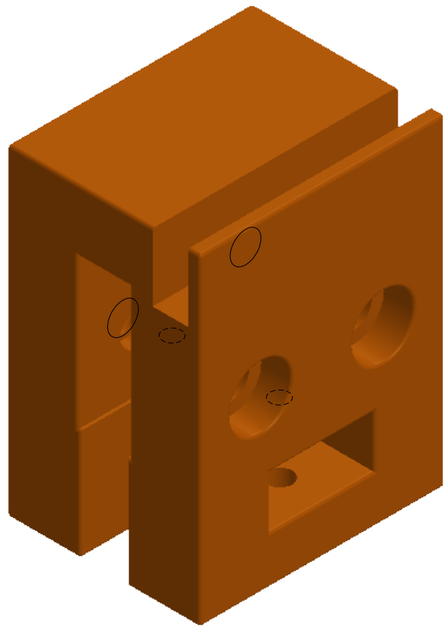

NOTE :

NAME : BEARING BLOCK HOUSING
SIZE : W63 X L80 X H105 MM
MTL : AL
QTY FOR 1 PANEL : 4 NOS
QTY FOR 3 PANEL : 12 NOS
OPERATION : VMC MACHINING

SPECIAL INSTRUCTION'S :

This drawing & design is the property of NIHVA TECHONOLOGIES PVT. LTD. Not to be sold or copied to any other concern.

TITLE - SPA SHOP UNIT

DWG NO - NTPL-002-PM-01

NIHVA Technologies Pvt. Ltd.


NIHVA TECHNOLOGIES PVT.LTD.PUNE
Website - www.nihva.com


	NAME	SIGNATURE	DATE
DRAWN	V.W.		19-06-2026
CHK'D	S.P.		20-06-2026
APPV'D	V.T.		20-06-2026

PRODUCT - C-SHAPE RETRACTABLE ROOF
PROJECT NO - NTPL-002-PM
REVISION - 00
SITE LOCATION-HYDRABAD
WEIGHT -
MATRIAL -
QTY - 1
PROJECTION METHOD:
SCALE :
SHEET 7 OF 19


If any queries contact - design2@nihva.com
ALL DIMENSION ARE IN mm
A2

DRAWING

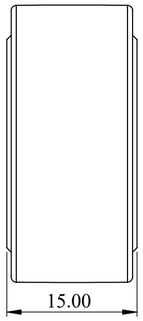

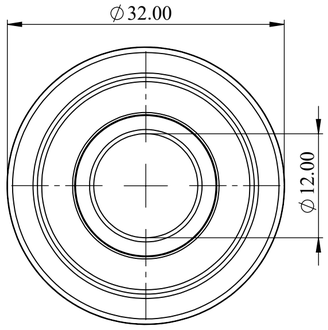



ITEM NO.	PART NUMBER	DESCRIPTION	QTY.
1	BEARING SKF_NATR 12	SKF (STD)	24

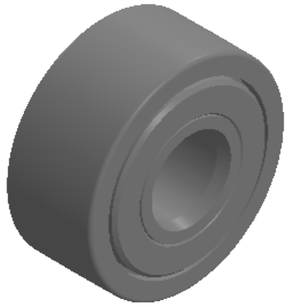


NAME : BEARING SKF NATR 12
SIZE : ID12 X OD32 X W15 MM
MTL : BEARING STEEL
QTY FOR 1 BLOCK : 2 NOS
QTY FOR 12 BLOCK : 24 NOS
DYANAMIC LOAD RATING : 7.04 KN

REV DESCRIPTION	DATE	REV NO
	19-06-2026	REV 00
1.		

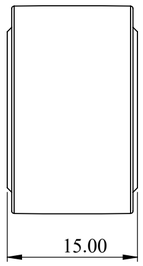

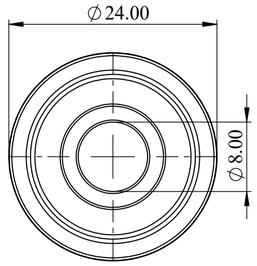

ITEM NO.	PART NUMBER	DESCRIPTION	QTY.
1	BEARING SKF_NATR 8	SKF(STD)	24

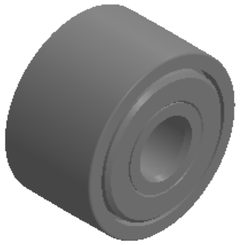

NAME : BEARING SKF NATR 8
SIZE : ID8 X OD24 X W15 MM
MTL : BEARING STEEL
QTY FOR 1 BLOCK : 2 NOS
QTY FOR 12 BLOCK : 24 NOS
DYANAMIC LOAD RATING : 4.57 KN

NOTE :

SPECIAL INSTRUCTION'S :

This drawing & design is the property of NIHVA TECHONOLOGIES PVT. LTD. Not to be sold or copied to any other concern.

TITLE - SPA SHOP UNIT

DWG NO - NTPL-002-PM-01


NIHVA TECHNOLOGIES PVT.LTD.PUNE
Website - www.nihva.com


	NAME	SIGNATURE	DATE
DRAWN	V.W.		19-06-2026
CHK'D	S.P.		20-06-2026
APPV'D	V.T.		20-06-2026

PRODUCT - C-SHAPE RETRACTABLE ROOF
PROJECT NO - NTPL-002-PM | REVISION - 00
SITE LOCATION-HYDRABAD | WEIGHT -
MATRIAL - | QTY - 1


If any queries contact - design2@nihva.com
ALL DIMENSION ARE IN mm | A2
PROJECTION METHOD:
SCALE :

DRAWING

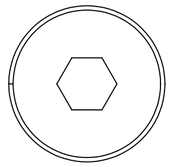

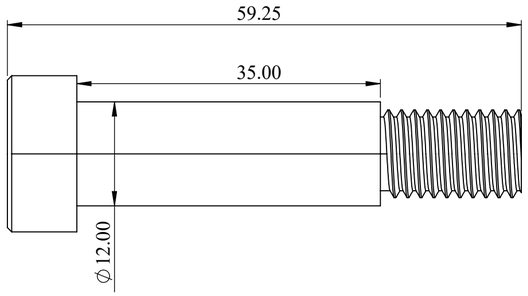


ITEM NO.	PART NUMBER	DESCRIPTION	QTY.
1	SHOULDER BOLT NATR 12.	SS	24

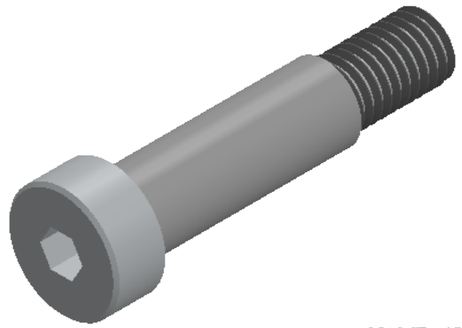


NAME : SHOULDER BOLT NATR 12
SIZE : M12X35 MM
MTL : SS
QTY FOR 1 BLOCK : 2 NOS
QTY FOR 12 BLOCK : 24 NOS

REV DESCRIPTION	DATE	REV NO
	19-06-2026	REV 00
1.		

ITEM NO.	PART NUMBER	DESCRIPTION	QTY.
1	ISO 7379 - 8 x 30 --- N	SS	24

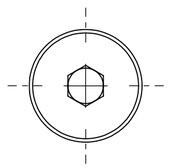

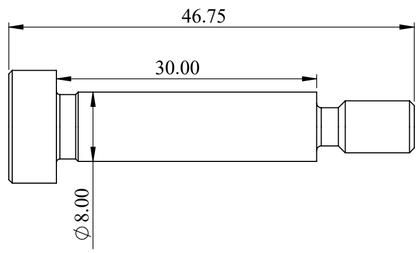



NAME : SHOULDER BOLT NATR 8
SIZE : M8X30 MM
MTL : SS
QTY FOR 1 BLOCK : 2 NOS
QTY FOR 12 BLOCK : 24 NOS

NOTE :

SPECIAL INSTRUCTION'S :

This drawing & design is the property of NIHVA TECHONOLOGIES PVT. LTD. Not to be sold or copied to any other concern.

TITLE - SPA SHOP UNIT

DWG NO - NTPL-002-PM-01

NIHVA TECHNOLOGIES PVT.LTD.PUNE
Website - www.nihva.com


	NAME	SIGNATURE	DATE
DRAWN	V.W.		19-06-2026
CHK'D	S.P.		20-06-2026
APPV'D	V.T.		20-06-2026

PRODUCT - C-SHAPE RETRACTABLE ROOF
PROJECT NO - NTPL-000-PM
REVISION - 00
SITE LOCATION-HYDRABAD
WEIGHT -
MATRIAL -
QTY - 1
SCALE :
PROJECTION METHOD:
If any queries contact - design2@nihva.com
ALL DIMENSION ARE IN mm
A2


DRAWING

ITEM NO.	PART NUMBER	DESCRIPTION	QTY.
1	INTERMIDEATE TUBE 50X50x1.5MM .		1
2	INTERMEDIATE SUPPORT WELDING PLATE .		2


REV DESCRIPTION	DATE	REV NO
	19-06-2026	REV 00
1.		

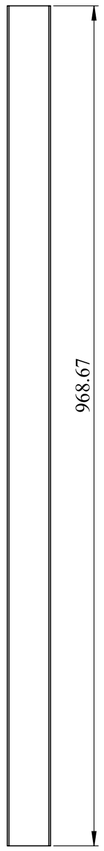


NAME : INTERMEDIATE SUPPORT TUBE
SIZE : 50X50X1.5 MM THK
MTL : AL
QTY FOR 1 PANEL : 36 NOS
QTY FOR 3 PANEL : 108 NOS
OPERATION : CUTTING

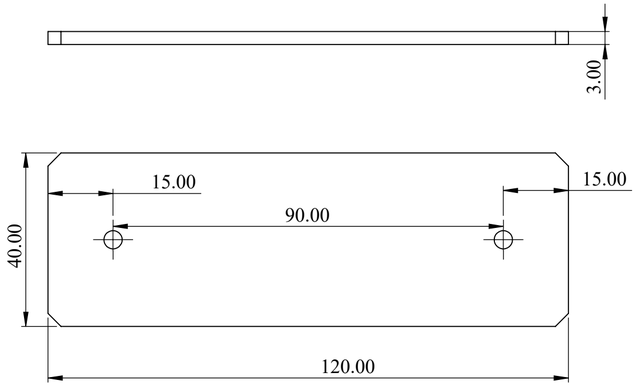

NAME : INTERMEDIATE SUPPORT TUBE WELDING PLATE
SIZE : 50X120X3 MM THK
MTL : AL
QTY FOR 1 PANEL : 72 NOS
QTY FOR 3 PANEL : 216 NOS
OPERATION : LASER CUTTING

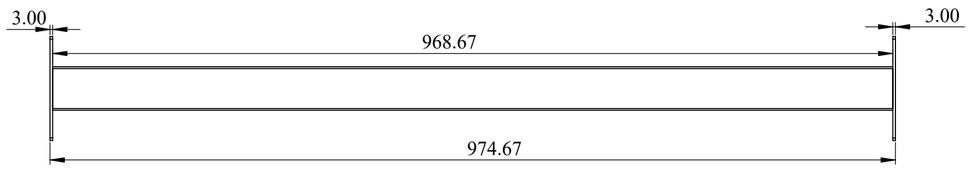

NAME : INTERMEDIATE SUPPORT TUBE
SIZE : 50X50X1.5 MM THK
MTL : AL
QTY FOR 1 PANEL : 36 NOS
QTY FOR 3 PANEL : 108 NOS
OPERATION : CUTTING

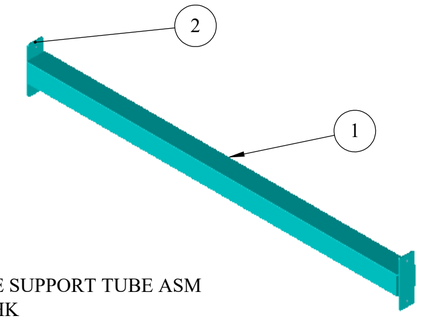

ISO VIEW

NAME : INTERMEDIATE SUPPORT TUBE ASM
SIZE : 50X50X1.5 MM THK
MTL : AL
QTY FOR 1 PANEL : 36 NOS
QTY FOR 3 PANEL : 108 NOS
OPERATION : CUTTING

NOTE :

SPECIAL INSTRUCTION'S :

This drawing & design is the property of NIHVA TECHONOLOGIES PVT. LTD. Not to be sold or copied to any other concern.

TITLE - SPA SHOP UNIT

DWG NO - NTPL-002-PM-01

NIHVA TECHNOLOGIES PVT.LTD.PUNE
Website - www.nihva.com


	NAME	SIGNATURE	DATE
DRAWN	V.W.		19-06-2026
CHK'D	S.P.		20-06-2026
APPV'D	V.T.		20-06-2026

PRODUCT - C-SHAPE RETRACTABLE ROOF
PROJECT NO - NTPL-000-PM | REVISION - 00
SITE LOCATION-HYDRABAD | WEIGHT -
MATRIAL - | QTY - 1
If any queries contact - design2@nihva.com
ALL DIMENSION ARE IN mm | A2
PROJECTION METHOD:
SCALE :


DRAWING


ITEM NO.	PART NUMBER	DESCRIPTION	QTY.
1	T PLATE	SS304 -117.5X156X3 MM THK	48

REV DESCRIPTION	DATE	REV NO
	19-06-2026	REV 00
1.		

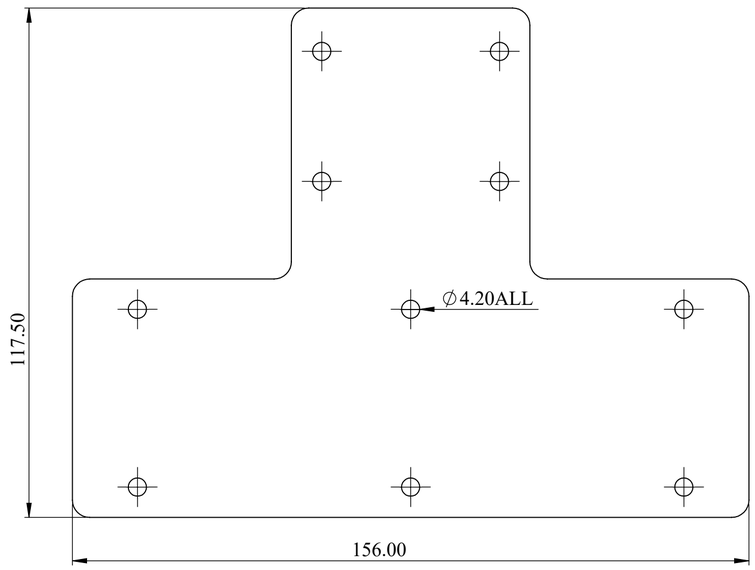

DEVELOPMENT VIEW

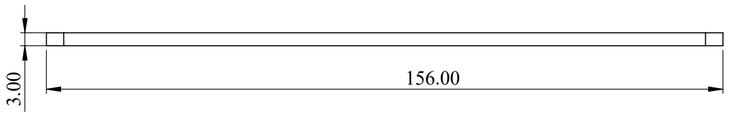

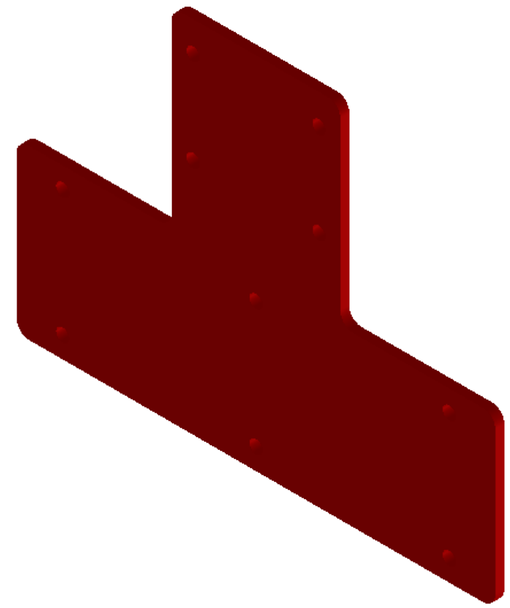

ISO VIEW

NAME : SS T PLATE
SIZE : 117.5X156X3 MM THK
THK : 3MM
MTL : SS
QTY REQ FOR 1 PANEL : 16 NOS
QTY REQ FOR 3 PANEL : 48 NOS.

NOTE :

SPECIAL INSTRUCTION'S :

This drawing & design is the property of NIHVA TECHONOLOGIES PVT. LTD. Not to be sold or copied to any other concern.

TITLE - SPA SHOP UNIT

DWG NO - NTPL-002-PM-01

NIHVA TECHNOLOGIES PVT.LTD.PUNE
Website - www.nihva.com


	NAME	SIGNATURE	DATE
DRAWN	V.W.		19-06-2026
CHK'D	S.P.		20-06-2026
APPV'D	V.T.		20-06-2026

PRODUCT - C-SHAPE RETRACTABLE ROOF
PROJECT NO - NTPL-002-PM | REVISION - 00
SITE LOCATION-HYDRABAD | WEIGHT -
MATRIAL - | QTY - 1
If any queries contact - design2@nihva.com | PROJECTION METHOD: | SCALE :
ALL DIMENSION ARE IN mm | A2 | SHEET 11 OF 19


DRAWING

ITEM NO.	PART NUMBER	DESCRIPTION	QTY.
1	L PLATE	SS304- 91X106X3 MM THK	24

REV DESCRIPTION	DATE	REV NO
	19-06-2026	REV 00
1.		

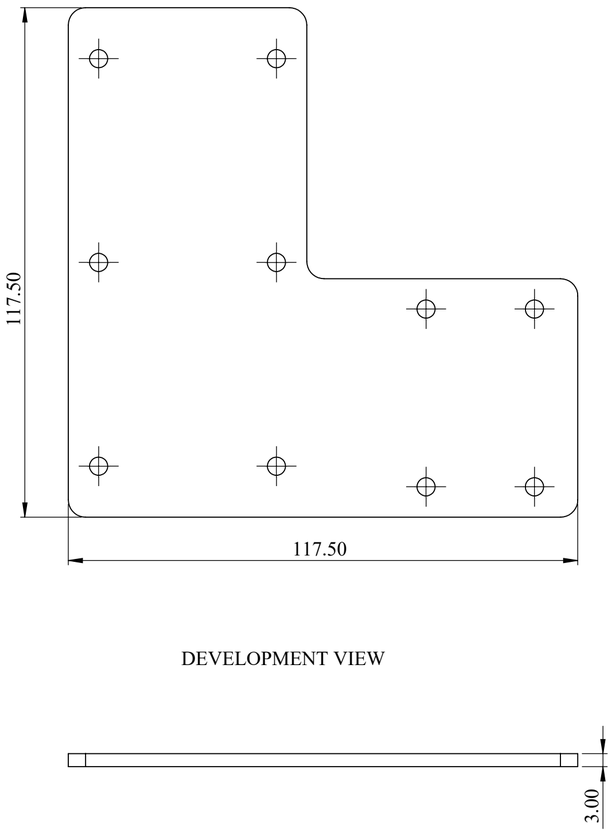

DEVELOPMENT VIEW

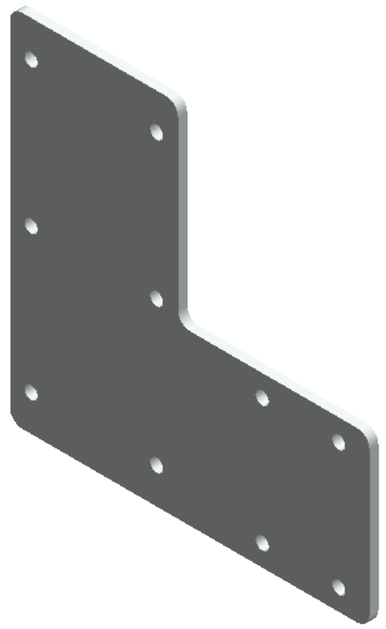

NAME : SS L PLATE
SIZE : 117.5X117.5X3 MM THK
THK : 3MM
MTL : SS
QTY REQ FOR 1 PANEL : 8 NOS
QTY REQ FOR 3 PANEL : 24 NOS.

NOTE :

SPECIAL INSTRUCTION'S :

This drawing & design is the property of NIHVA TECHONOLOGIES PVT. LTD. Not to be sold or copied to any other concern.

TITLE - SPA SHOP UNIT

DWG NO - NTPL-002-PM-01

NIHVA TECHNOLOGIES PVT.LTD.PUNE
Website - www.nihva.com

	NAME	SIGNATURE	DATE
DRAWN	V.W.		19-06-2026
CHK'D	S.P.		20-06-2026
APPV'D	V.T.		20-06-2026


PRODUCT - C-SHAPE RETRACTABLE ROOF
PROJECT NO - NTPL-002-PM
REVISION - 00
SITE LOCATION-HYDRABAD
WEIGHT -
MATRIAL -
QTY - 1


If any queries contact - design2@nihva.com
ALL DIMENSION ARE IN mm
A2
PROJECTION METHOD:
SCALE :


DRAWING

ITEM NO.	PART NUMBER	DESCRIPTION	QTY.
1	L ANGLE WELDING CORNER JOINING PLATE	AL WELDING JOINING PLATE	72

REV DESCRIPTION	DATE	REV NO
	19-06-2026	REV 00
1.		

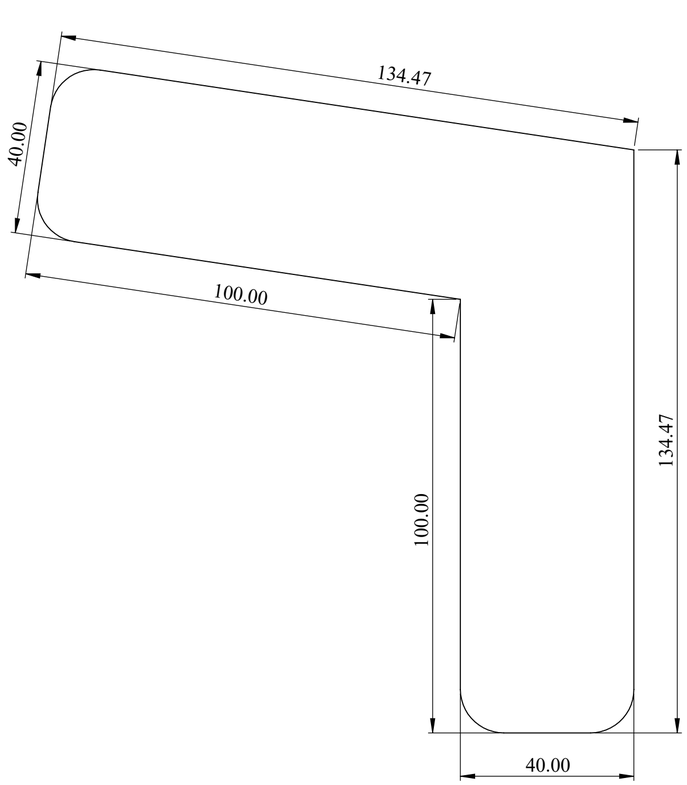

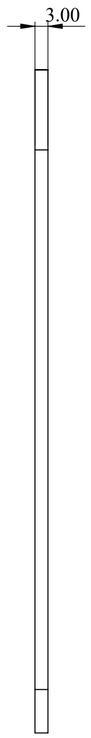

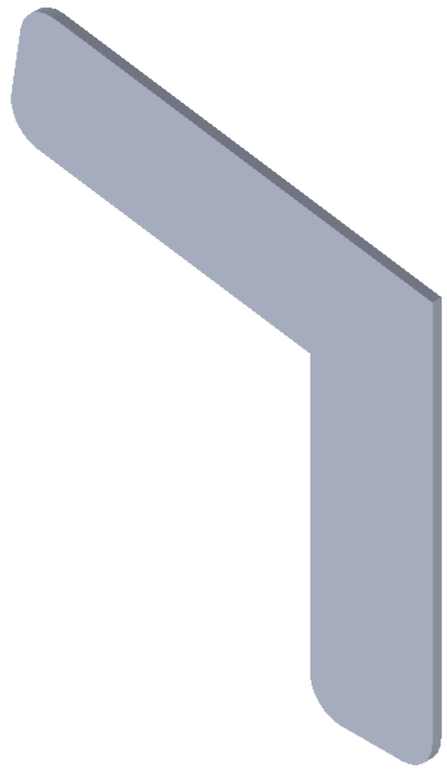

NAME : AL L ANGLE WELDING PLATE
SIZE : 40X100X3 MM THK
THK : 3MM
MTL : AL
QTY REQ FOR 1 PANEL : 24 NOS
QTY REQ FOR 3 PANEL : 72 NOS.

NOTE :

SPECIAL INSTRUCTION'S :

This drawing & design is the property of NIHVA TECHONOLOGIES PVT. LTD. Not to be sold or copied to any other concern.

TITLE - SPA SHOP UNIT


DWG NO - NTPL-002-PM-01

NIHVA TECHNOLOGIES PVT.LTD.PUNE
Website - www.nihva.com


	NAME	SIGNATURE	DATE
DRAWN	V.W.		19-06-2026
CHK'D	S.P.		20-06-2026
APPV'D	V.T.		20-06-2026

PRODUCT - C-SHAPE RETRACTABLE ROOF
PROJECT NO - NTPL-002-PM
REVISION - 00
SITE LOCATION-HYDRABAD
WEIGHT -
MATRIAL -
QTY - 1
SCALE :
PROJECTION METHOD:
If any queries contact - design2@nihva.com
ALL DIMENSION ARE IN mm
A2

DRAWING

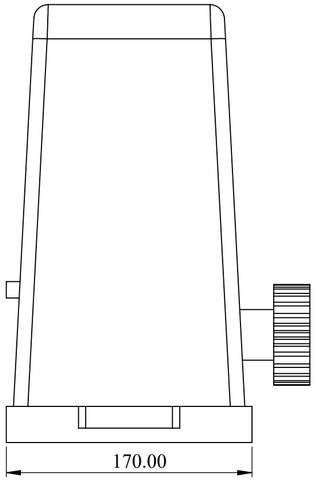


F.V.

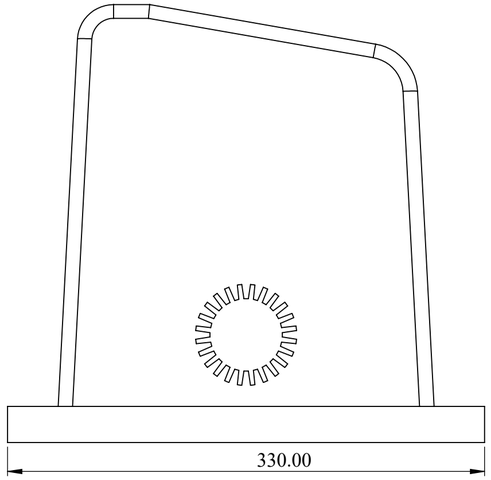


S.V.

ITEM NO.	PART NUMBER	DESCRIPTION	QTY.
1	NICE RB 1T	MOTOR	3

REV DESCRIPTION	DATE	REV NO
	19-06-2026	REV 00
1.		

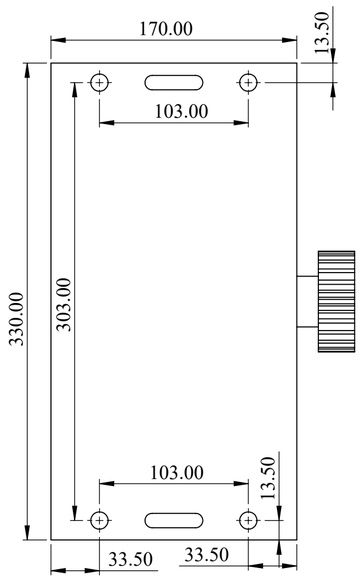

B.V.

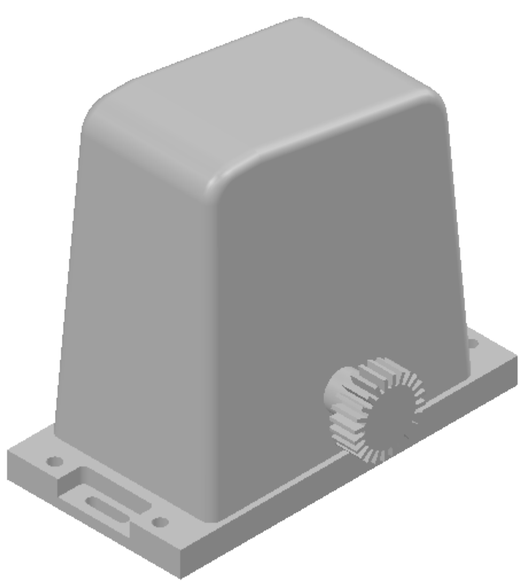

ISO VIEW

NAME : NICE MOTOR
SIZE : 0.8T
QTY REQ FOR 1 PANEL : 1 NOS
QTY REQ FOR 3 PANEL : 3 NOS.

NOTE :

SPECIAL INSTRUCTION'S :

This drawing & design is the property of NIHVA TECHONOLOGIES PVT. LTD. Not to be sold or copied to any other concern.

TITLE - SPA SHOP UNIT

DWG NO - NTPL-002-PM-01


NIHVA TECHNOLOGIES PVT.LTD.PUNE
Website - www.nihva.com

	NAME	SIGNATURE	DATE
DRAWN	V.W.		19-06-2026
CHK'D	S.P.		20-06-2026
APPV'D	V.T.		20-06-2026


PRODUCT - C-SHAPE RETRACTABLE ROOF
PROJECT NO - NTPL-002-PM
REVISION - 00
SITE LOCATION-HYDRABAD
WEIGHT -
MATRIAL -
QTY - 1
PROJECTION METHOD:
SCALE :
SHEET 14 OF 19

If any queries contact - design2@nihva.com
ALL DIMENSION ARE IN mm
A2


DRAWING

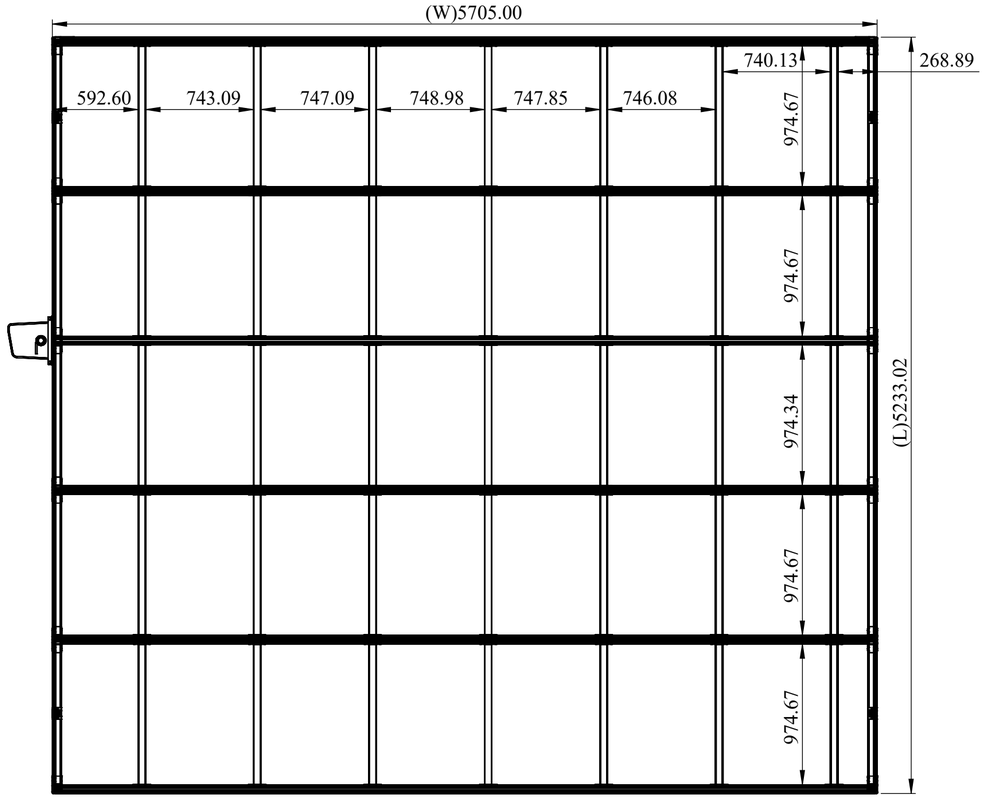

T.V.

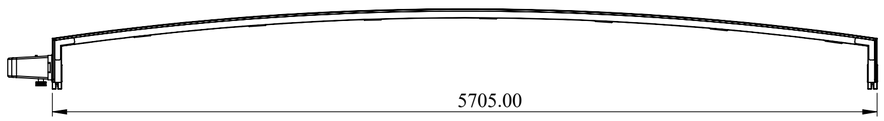

F.V.

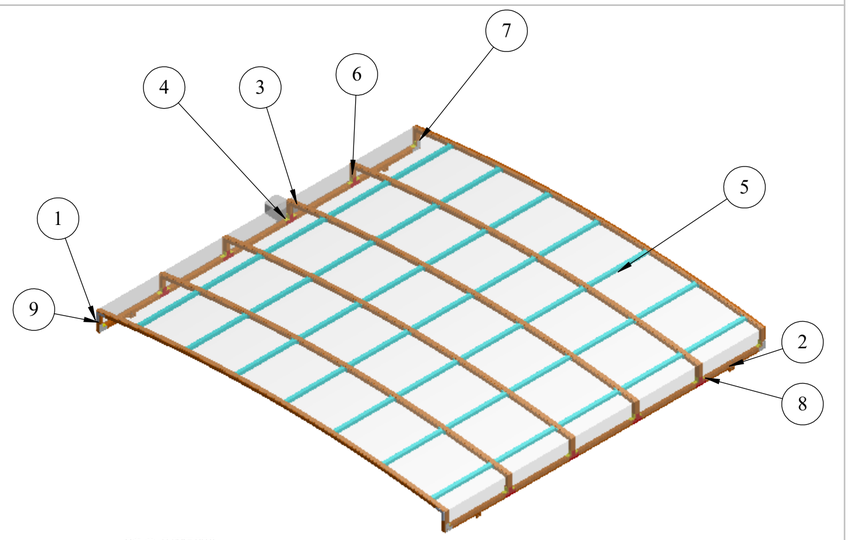

ISO VIEW

PANEL NO - 02 ASM

ITEM NO.	PART NUMBER	DESCRIPTION	QTY.
1	PANEL - 2 - SPA	AL PROFILE	1
2	BEARING BLOCK ASM _ T75_1B. - 2 - SPA	AL	4
3	MOTOR BASE PLATE - SPA	AL/MS	1
4	NICE RB 0.8T	NICE	1
5	INTERMEDIATE SUPPORT TUBE ASM . - 2 - SPA	AL	35
6	T PLATE	SS304 -117.5X156X3 MM THK	16
7	L PLATE	SS304- 91X106X3 MM THK	8
8	L ANGLE PLATE	SS304 - 60X60X3 MM	20
9	L ANGLE WELDING CORNER JOINING PLATE	AL WELDING JOINING PLATE	24

REV DESCRIPTION	DATE	REV NO
	19-06-2026	REV 00
1.		

NOTE :

NAME : PANEL NO - 02 ASM
PROFILE : AL GNTOO6
QTY : 01 NOS

SPECIAL INSTRUCTION'S :

This drawing & design is the property of NIHVA TECHONOLOGIES PVT. LTD. Not to be sold or copied to any other concern.


TITLE - SPA SHOP UNIT

DWG NO - NTPL-002-PM-01

NIHVA TECHNOLOGIES PVT.LTD.PUNE
Website - www.nihva.com


	NAME	SIGNATURE	DATE		
DRAWN	V.W.		19-06-2026	PRODUCT - C-SHAPE RETRACTABLE ROOF	
CHK'D	S.P.		20-06-2026	PROJECT NO - NTPL-000-PM	REVISION - 00
APPV'D	V.T.		20-06-2026	SITE LOCATION-HYDRABAD	WEIGHT -
				MATRIAL -	QTY - 1
If any queries contact - design2@nihva.com				PROJECTION METHOD:	SCALE :
ALL DIMENSION ARE IN mm		A2			SHEET 15 OF 19

DRAWING

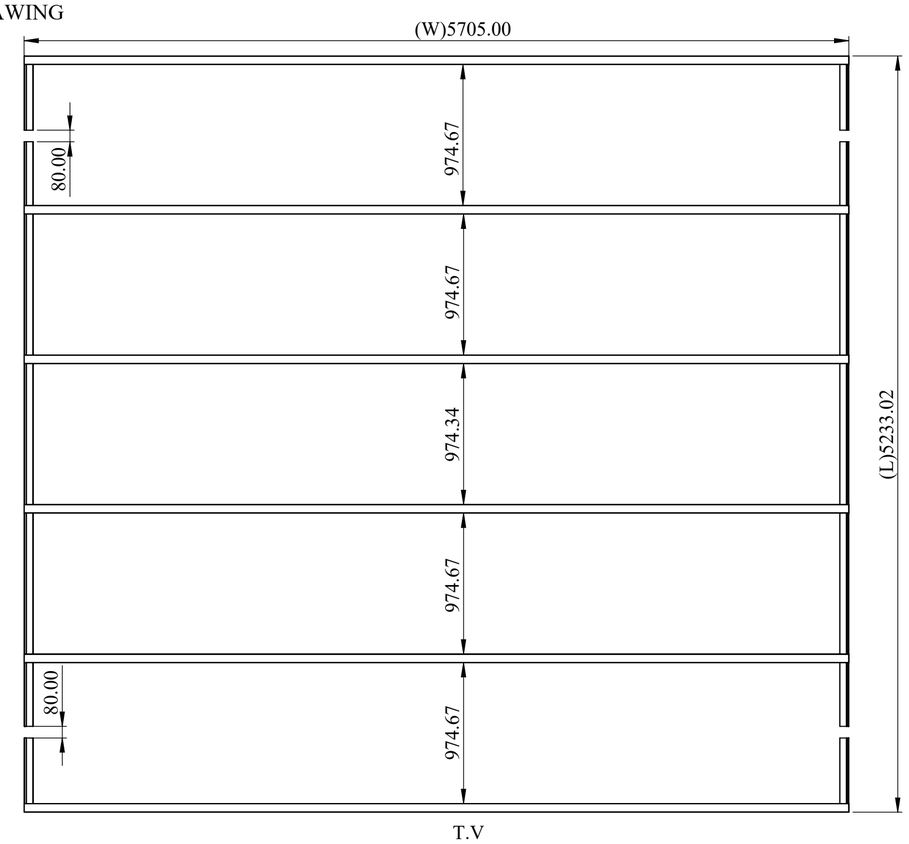


T.V

ITEM NO.	PART NUMBER	DESCRIPTION	QTY.
1	PANEL - 2		01

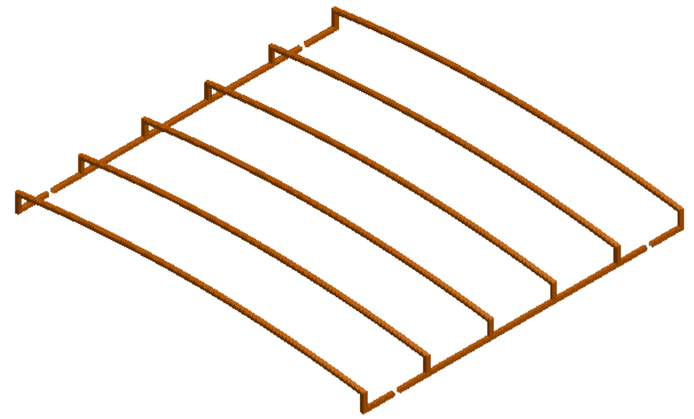


ISO VIEW
PANEL NO - 2 SPA SHOP


REV DESCRIPTION	DATE	REV NO
	19-06-2026	REV 00
1.		

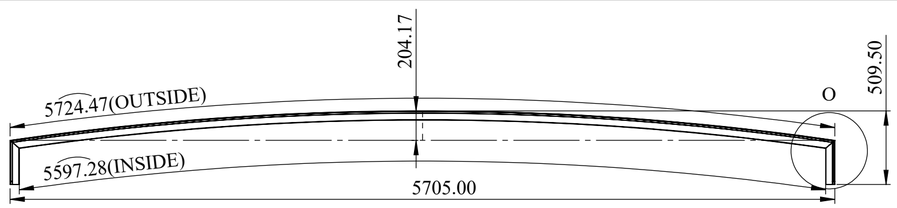


F.V

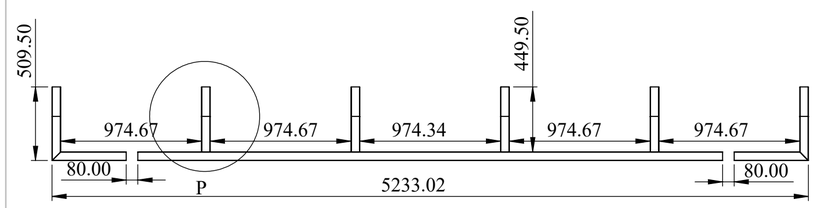

S.V

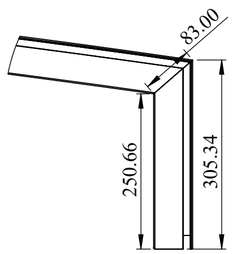

DETAIL O
SCALE 1 : 7

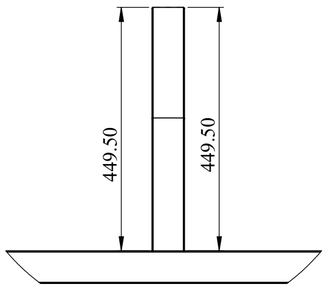

DETAIL P
SCALE 1 : 8

NOTE :

NAME : PANEL NO - 02
PROFILE : AL GNTOO6 (60X63)
QTY : 01 NOS.

SPECIAL INSTRUCTION'S :

This drawing & design is the property of NIHVA TECHONOLOGIES PVT. LTD. Not to be sold or copied to any other concern.

TITLE - SPA SHOP UNIT

DWG NO - NTPL-002-PM-01

NIHVA TECHNOLOGIES PVT.LTD.PUNE
Website - www.nihva.com

	NAME	SIGNATURE	DATE		
				PRODUCT - C-SHAPE RETRACTABLE ROOF	
DRAWN	V.W.		19-06-2026	PROJECT NO - NTPL-002-PM	REVISION - 00
CHK'D	S.P.		20-06-2026	SITE LOCATION-HYDRABAD	WEIGHT -
APPV'D	V.T.		20-06-2026	MATRIAL -	QTY - 1


If any queries contact - design2@nihva.com

ALL DIMENSION ARE IN mm | A2

PROJECTION METHOD:


SCALE :


DRAWING

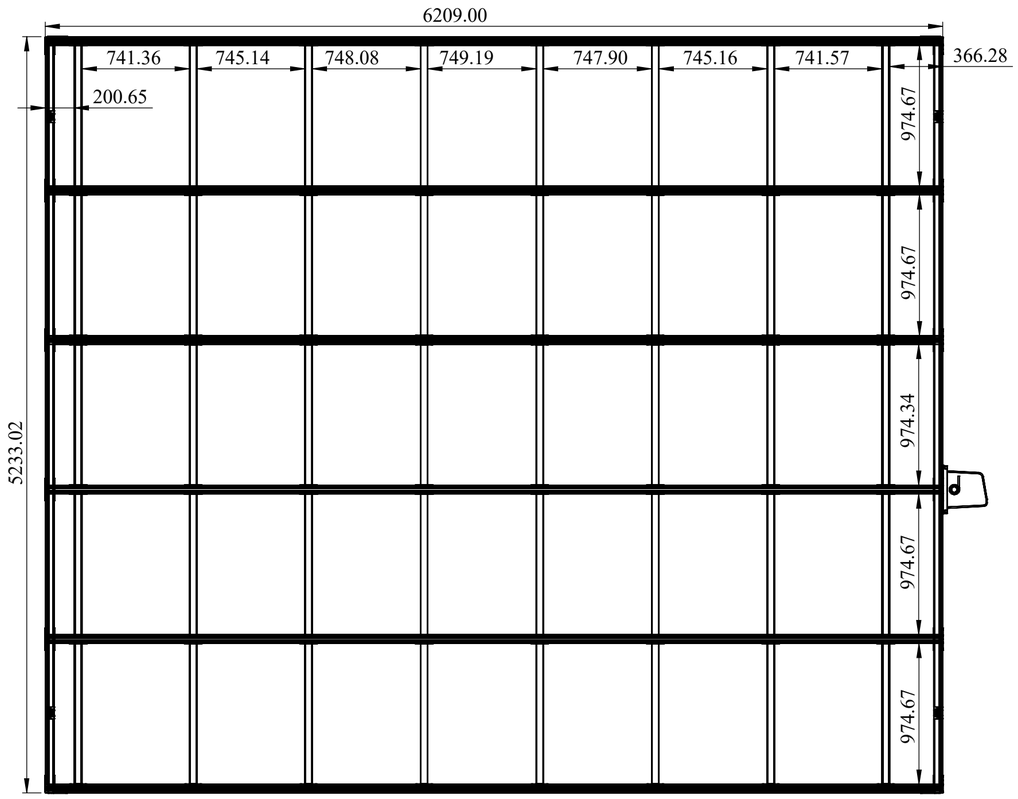

ITEM NO.	PART NUMBER	DESCRIPTION	QTY.
1	PANEL - 3- SPA	AL PROFILE	1
2	BEARING BLOCK ASM _ T75_1B. - 3- SPA	AL	4
3	INTERMEDIATE SUPPORT TUBE ASM . - 3- SPA	SQ TUBE 50X50X1.5MM THK	40
4	MOTOR BASE PLATE- SPA	MS/AL	1
5	NICE RB 0.8T- SPA	NICE	1
6	T PLATE	SS304 -117.5X156X3 MM THK	16
7	L PLATE	SS304- 91X106X3 MM THK	8
8	L ANGLE WELDING CORNER JOINING PLATE	AL WELDING JOINING PLATE	24

REV DESCRIPTION	DATE	REV NO
	19-06-2026	REV 00
1.		

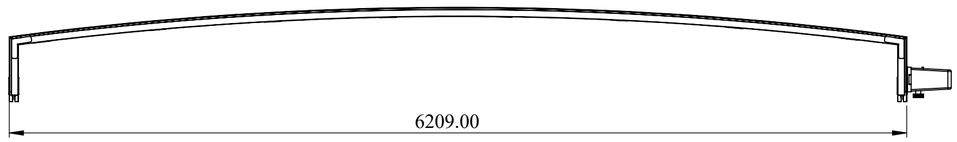

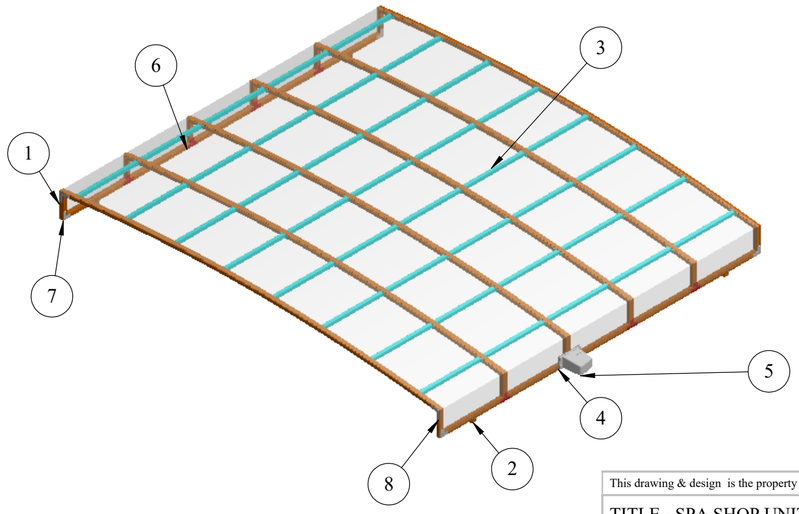

NOTE :

NAME : PANEL NO - 03 ASM
PROFILE : AL GNTOO6
QTY : 01 NOS

SPECIAL INSTRUCTION'S :

This drawing & design is the property of NIHVA TECHONOLOGIES PVT. LTD. Not to be sold or copied to any other concern.

TITLE - SPA SHOP UNIT

DWG NO - NTPL-002-PM-01

NIHVA TECHNOLOGIES PVT.LTD.PUNE
Website - www.nihva.com

	NAME	SIGNATURE	DATE	
DRAWN	V.W.		19-06-2026	PRODUCT - C-SHAPE RETRACTABLE ROOF
CHK'D	S.P.		20-06-2026	PROJECT NO - NTPL-002-PM / REVISION - 00
APPV'D	V.T.		20-06-2026	SITE LOCATION-HYDRABAD / WEIGHT -
				MATRIAL - / QTY - 1


If any queries contact - design2@nihva.com

ALL DIMENSION ARE IN mm | A2

PROJECTION METHOD:


SCALE :

DRAWING

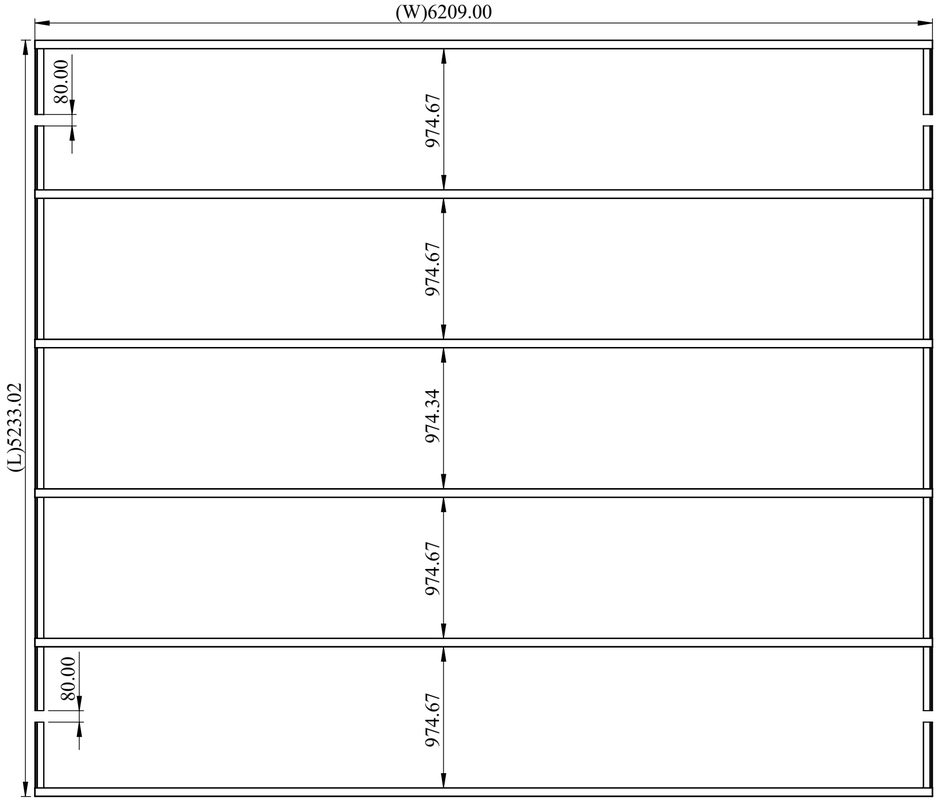


T.V.

ITEM NO.	PART NUMBER	DESCRIPTION	QTY.
1	PANEL - 3- SPA	AL PROFILE	1

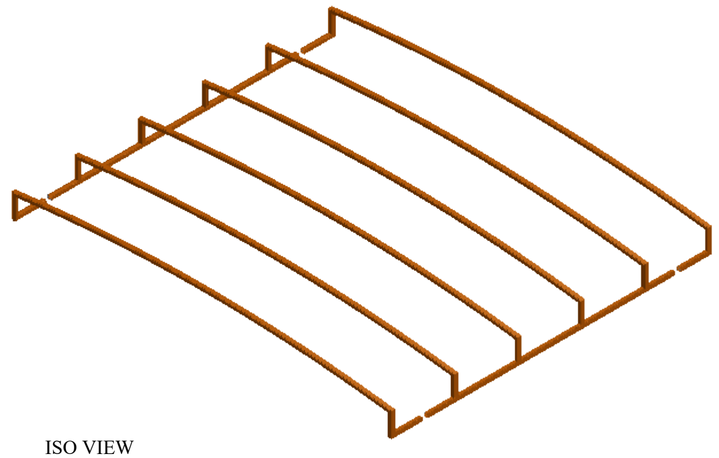


ISO VIEW
PANEL NO 3


REV DESCRIPTION	DATE	REV NO
	19-06-2026	REV 00
1.		

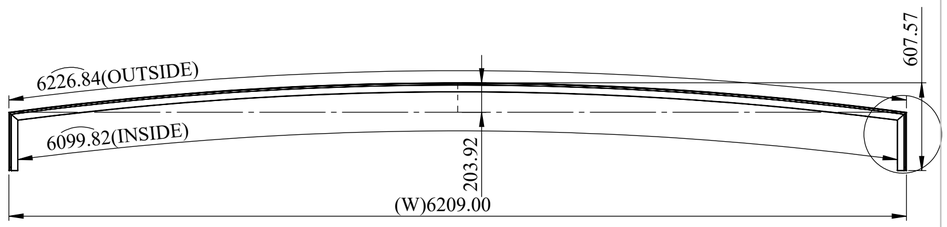


F.V.

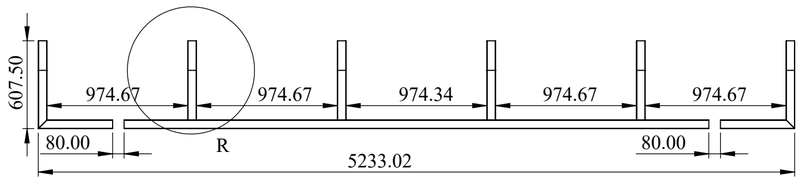

S.V.

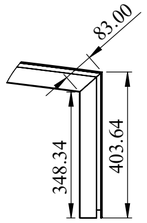

DETAIL Q
SCALE 1 : 12
T.V.

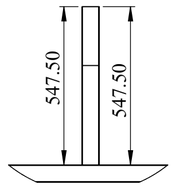

DETAIL R
SCALE 1 : 15

NOTE :

NAME : PANEL NO - 03
PROFILE : AL GNTOO6 (60X63)
QTY : 01 NOS.

SPECIAL INSTRUCTION'S :

This drawing & design is the property of NIHVA TECHONOLOGIES PVT. LTD. Not to be sold or copied to any other concern.

TITLE - SPA SHOP UNIT

DWG NO - NTPL-002-PM-01

NIHVA TECHNOLOGIES PVT.LTD.PUNE
Website - www.nihva.com


	NAME	SIGNATURE	DATE
DRAWN	V.W.		19-06-2026
CHK'D	S.P.		20-06-2026
APPV'D	V.T.		20-06-2026


PRODUCT - C-SHAPE RETRACTABLE ROOF
PROJECT NO - NTPL-002-PM
REVISION - 00
SITE LOCATION-HYDRABAD
WEIGHT -
MATRIAL -
QTY - 1
If any queries contact - design2@nihva.com
PROJECTION METHOD:
SCALE :
ALL DIMENSION ARE IN mm
A2

DRAWING

REV DESCRIPTION	DATE	REV NO
	19-06-2026	REV 00
1.		

ITEM NO.	PART NUMBER	DESCRIPTION	QTY.
1	RACK	STD (1 M LENGTH)	45

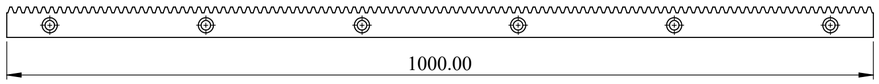

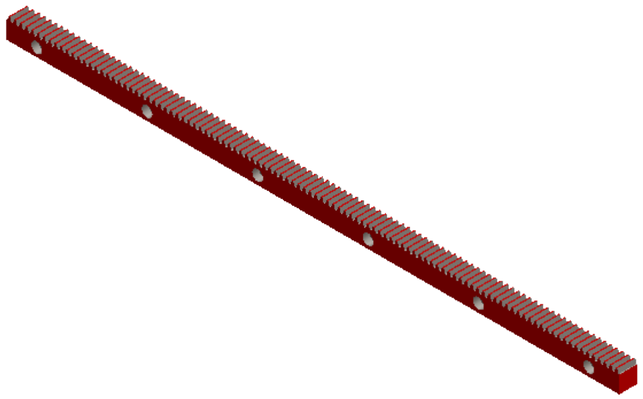

NAME : RACK
SIZE : M6 MODULE (30X30X8 MM)
QTY REQUIRED FOR 1 PANEL : 15 NOS
QTY REQUIRED FOR 3 PANEL : 45 NOS

NOTE :

SPECIAL INSTRUCTION'S :

This drawing & design is the property of NIHVA TECHONOLOGIES PVT. LTD. Not to be sold or copied to any other concern.

TITLE - ROOF AUTOMATION

DWG NO - NTPL-002-PM-01

NIHVA TECHNOLOGIES PVT.LTD.PUNE
Website - www.nihva.com

	NAME	SIGNATURE	DATE
DRAWN	V.W.		19-06-2026
CHK'D	S.P.		20-06-2026
APPV'D	V.T.		20-06-2026

If any queries contact - design2@nihva.com

ALL DIMENSION ARE IN mm | A2

PRODUCT - C-SHAPE RETRACTABLE ROOF

PROJECT NO - NTPL-002-PM | REVISION - 00

SITE LOCATION-HYDRABAD | WEIGHT -

MATRIAL - | QTY - 1

PROJECTION METHOD:

SCALE :