

DRAWING NO:- 02/02

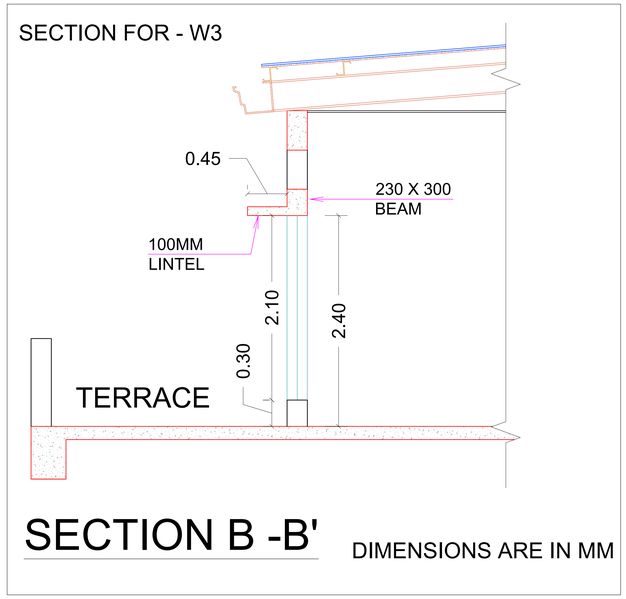

SECTION B -B'

DIMENSIONS ARE IN MM

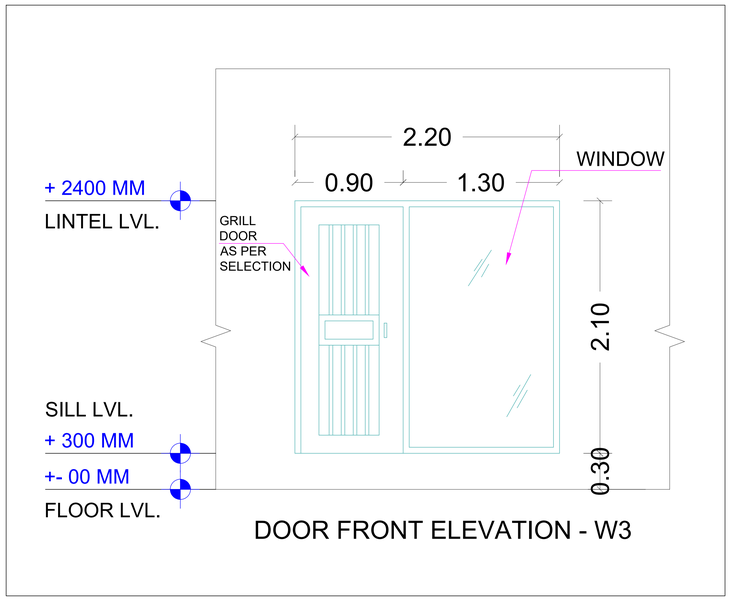


DOOR FRONT ELEVATION - W3

SCHEDULE OF OPENING:

NAME	LENGTH	HEIGHT	NOS.
V	4.00	0.60	6
V1	3.00	0.60	12
V2	COLUMN WIDE	0.60	?
W1	2.60	1.50	16
W2	2.20	1.50	26
W3	2.20	2.10	2

SCHEDULE OF OPENING:

NAME	LENGTH	HEIGHT	NOS.
D1	1.20	2.40	22

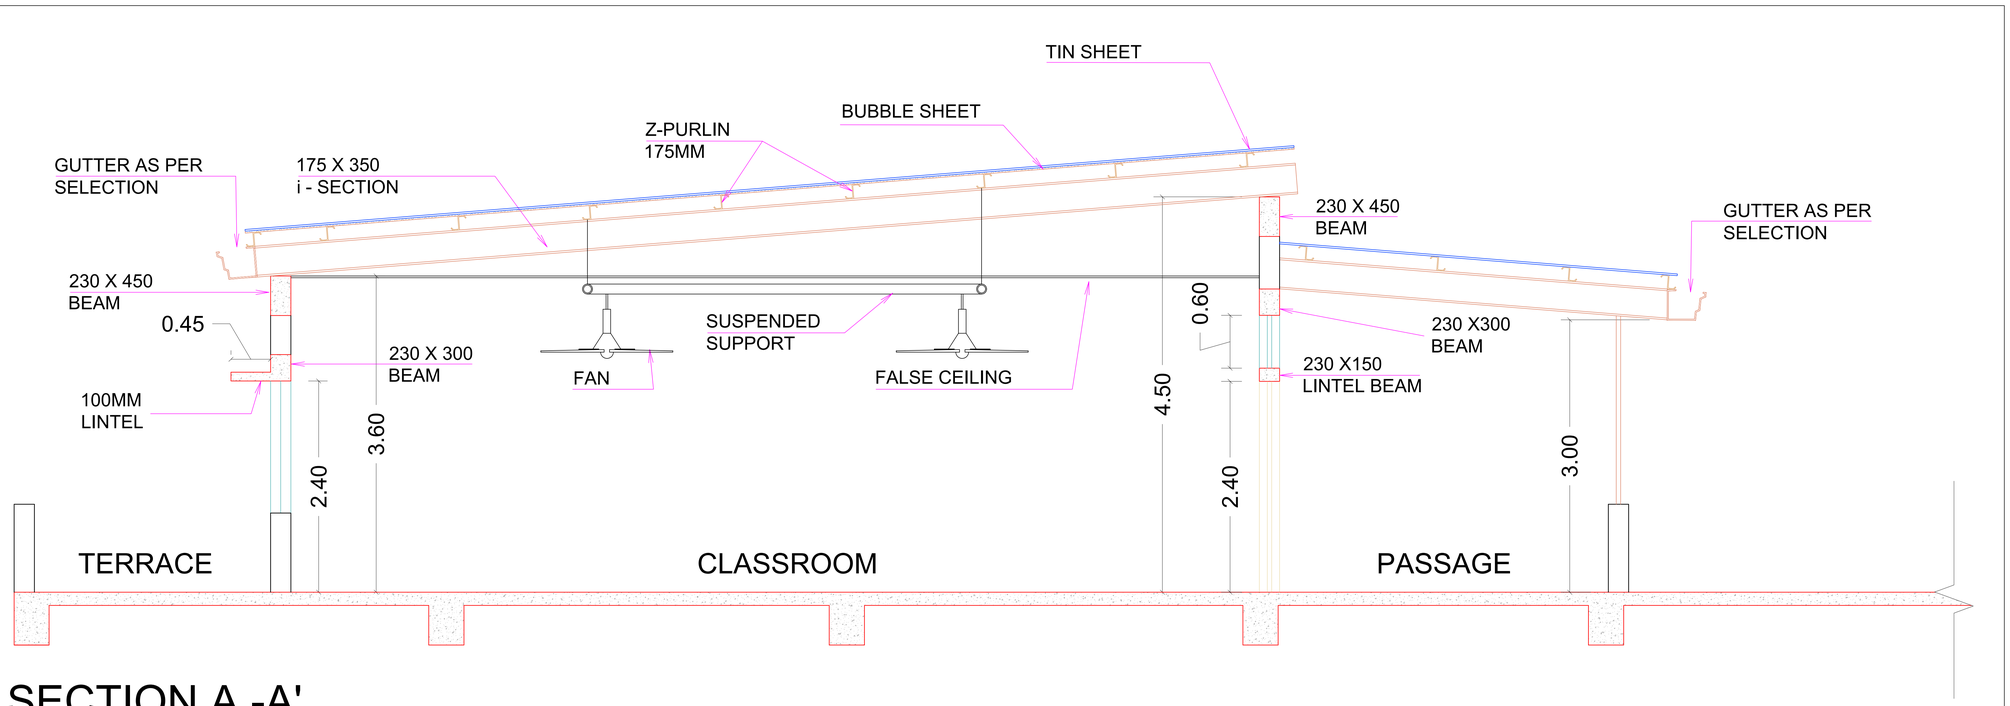

SECTION A -A'

DIMENSIONS ARE IN MM

NOTES :-

1) All dimensions are in MM, unless otherwise specified.
2) Do not scale the drawing. Follow written dimensions only.
3) The architectural & structural drawings should be read out in coordination.
4) Consult architects in case of any discrepancy on site or in the drawing.
5) The contractor shall not make any deviation, alteration in specification involving implication without prior consent of the architect

REVISIONS :

SR.NO.	REVISION	NO
01	R0	R0

PROJECT TITLE :-
PROPOSED FLOOR EXTENSION FOR DEOGIRI INSTITIUTE OF ENGINEERING AND MANAGEMENT STUDIES

CLIENT NAME :- DEOGIRI INSTITIUTE OF ENGINEERING AND MANAGEMENT STUDIES

BUILDING NAME :- DEOGIRI INSTITUTE OF ENGINEERING

DRAWING TITLE :- FIFTH FLOOR WORKING PLAN

DRAWING NO:- 01

DATE	SCALE	DRAWN BY	CHKD BY
19.07.2025	N.T.S	AR.SAMEER	

FILE LOCATION: Y:\sakhare sir\MSP MANDAL\AURANGABAD\DEOGIRI ENGINEERING\FLOOR EXTENSION 27 03 2025\DEOGIRI FLOOR EXTENSION PLAN-15.07.2025

NORTH

N

ARCHITECT SIGN & STAMP

ARCHITECT :-

SARTHAK ASSOCIATES

I ARCHITECTS I INTERIOR DESIGNERS I VALUER I

C-7,PROZONE TRADE CENTRE,PROZONE MALL AURANGABAD.