


PRODUCED BY AN AUTODESK EDUCATIONAL PRODUCT

# F3

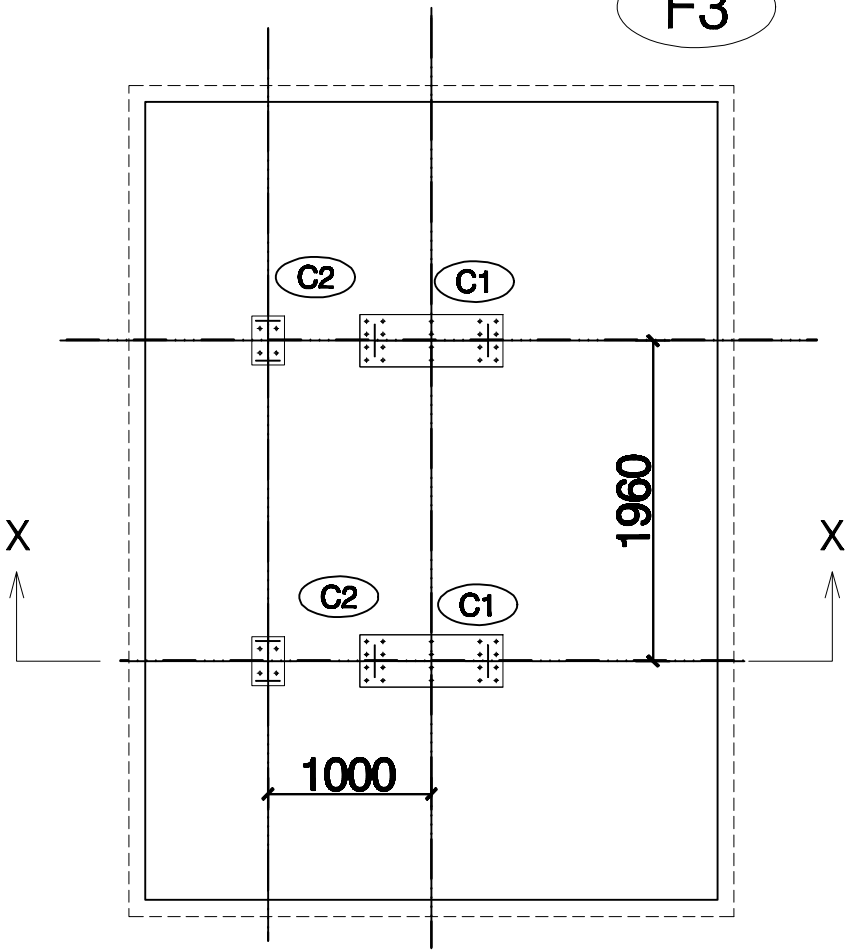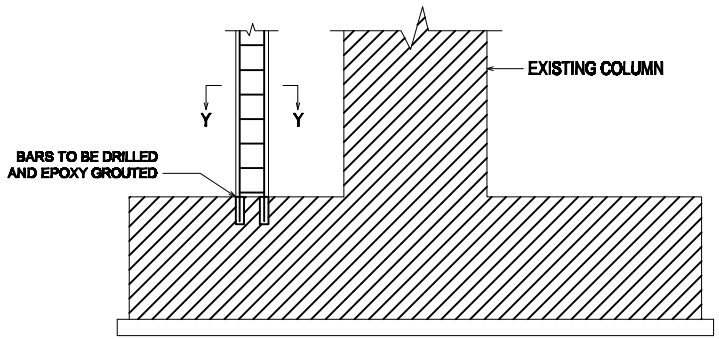



SECTION X- X

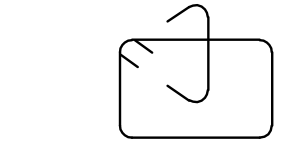

T8 @ 200
(2NOS.-LINKS/SET)

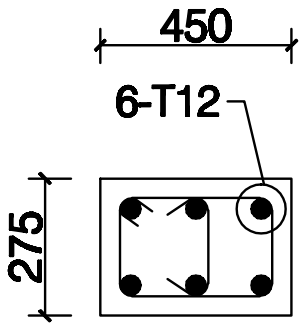


SECTION Y- Y

KEY PLAN :-

LEGEND :-

REINFORCED CONCRETE

230MM THK BRICK WALL

STRUCTURAL GLAZING

N

**GENERAL NOTES :**

ALL DIMENSIONS ARE IN MILLIMETERS AND ARE MEASURED DIMENSIONS UNLESS OTHERWISE SPECIFIED.

ALL LEVELS ARE IN METERS AND ARE MEASURED LEVELS UNLESS OTHERWISE SPECIFIED.

DO NOT SCALE DRAWING, ONLY WRITTEN DIMENSIONS SHALL BE FOLLOWED. ANY DISCREPANCIES NEED SHALL BE BROUGHT TO THE NOTICE OF THE ARCHITECT PRIOR TO EXECUTION.

**SCHEDULE OF JOINERY**

| TYPE | DESCRIPTION | SIZE | NO. |
|---|---|---|---|
| RS | HANGER DOOR | 24000 x 6000 | 01 |
| W | WINDOW | 1500 x 1200 | 20 |
| D | DOOR | 1200 x 2200 | 9 |
| | | | |
| | | | |

**GENERAL NOTES :**

1. ALL DIMENSIONS ARE IN MM UNLESS NOTED OTHERWISE.
2. READ THIS DRG ALONG WITH RELEVANT ARCH. DRG.
3. CONCRETE GRADE M25 FOR ALL EXCEPT NOTED OTHERWISE.
4. DO NOT SCALE THE DRG, FOLLOW WRITTEN DIMENSIONS. ANY MISMATCH IN ARCH OR SERVICES DRGS TO BE CLARIFIED FROM ENGINEER.
5. 'Y' DESIGNATES STEEL REINFORCEMENT DIA, AND SHALL CONFORM TO IS-1786 WITH MINIMUM YIELD STRENGTH OF 500 N/SQ.MM.
6. DO NOT PROVIDE MORE THAN 50% LAPPING AT ANY SECTION, AND AVOID LAPS AT LOCATIONS OF MAXIMUM BENDING MOMENTS. LAP LENGTH/DEVELOPMENT LENGTH SHALL BE AS FOLLOWS: 40xBAR DIA FOR M20 CONCRETE; 45xBAR DIA FOR M25 CONCRETE
7. NOMINAL COVER SHALL BE AS FOLLOWS: BEAMS–30MM, SLABS–25MM, COLUMNS–40MM, FOUNDATION–50MM.
8. WATER CEMENT RATIO FOR CONCRETE MIX SHALL NOT BE MORE THAN 0.45. IF REQUIRED USE PLASTICISER TO CONTROL SAME.
9. DISTRIBUTION STEEL WHEREVER NOT SHOWN SHALL BE 8Y–200 C/C
10. FOR DETAILS TO THIS DRG REFER OTHER STR DRGS.
11. THE FDN IS DESIGNED CONSIDERING 30T/SQM NET BEARING CAPACITY AT FOUNDING LEVEL
12. ALL LAYOUT DIMNS TO MATCH ARCHT DRGS AND ALL MEMBER SIZES AND REINFT TO MATCH STRUCTURAL DRGS.

| REV. | DESCRIPTION | DATE | BY | CHD. |
|---|---|---|---|---|
| R0 | ISSUED FOR APPROVAL | 20-07-17 | CMF | SSF |

AMENDMENT

GRAPHIC SCALE: 0 0.5M 2M 4M / 0.5M 0 1M 3M 5M

ARCHITECT

CLIENT:
HANGER
AT PUNE

PROJECT LOCATION:
PUNE

DRAWING TITLE:
COLUMN FOOTING DRAWINGS

SCALE : NTS | DRAWN : CMF
DATE : 06-09-2016 | CHKD : SNK

R0

PROJECT ID:
1718-AI-052-PEB

DRAWING NO:
PD: 01

Astre Infra
Private Limited
imagine and its done
691, Bansdal Indl. Estate,
Khanapur Rd,
Udyambag, Belgaum- 590008.
www.astreinfra.com

THESE DRAWINGS ARE AND SHALL REMAIN THE PROPERTY OF ASTRE INFRA PVT. LTD. AND ARE NOT TO BE USED IN ANY WAY WHATSOEVER EXCEPT WITH THE WRITTEN PERMISSION OF ASTRE INFRA PVT. LTD. ALL RIGHTS ARE RESERVED IN THE EVENT OF PUBLICATION OF THESE DRAWINGS THE COPYRIGHT NOTICE MUST BE READ AS ABOVE.

PRODUCED BY AN AUTODESK EDUCATIONAL PRODUCT