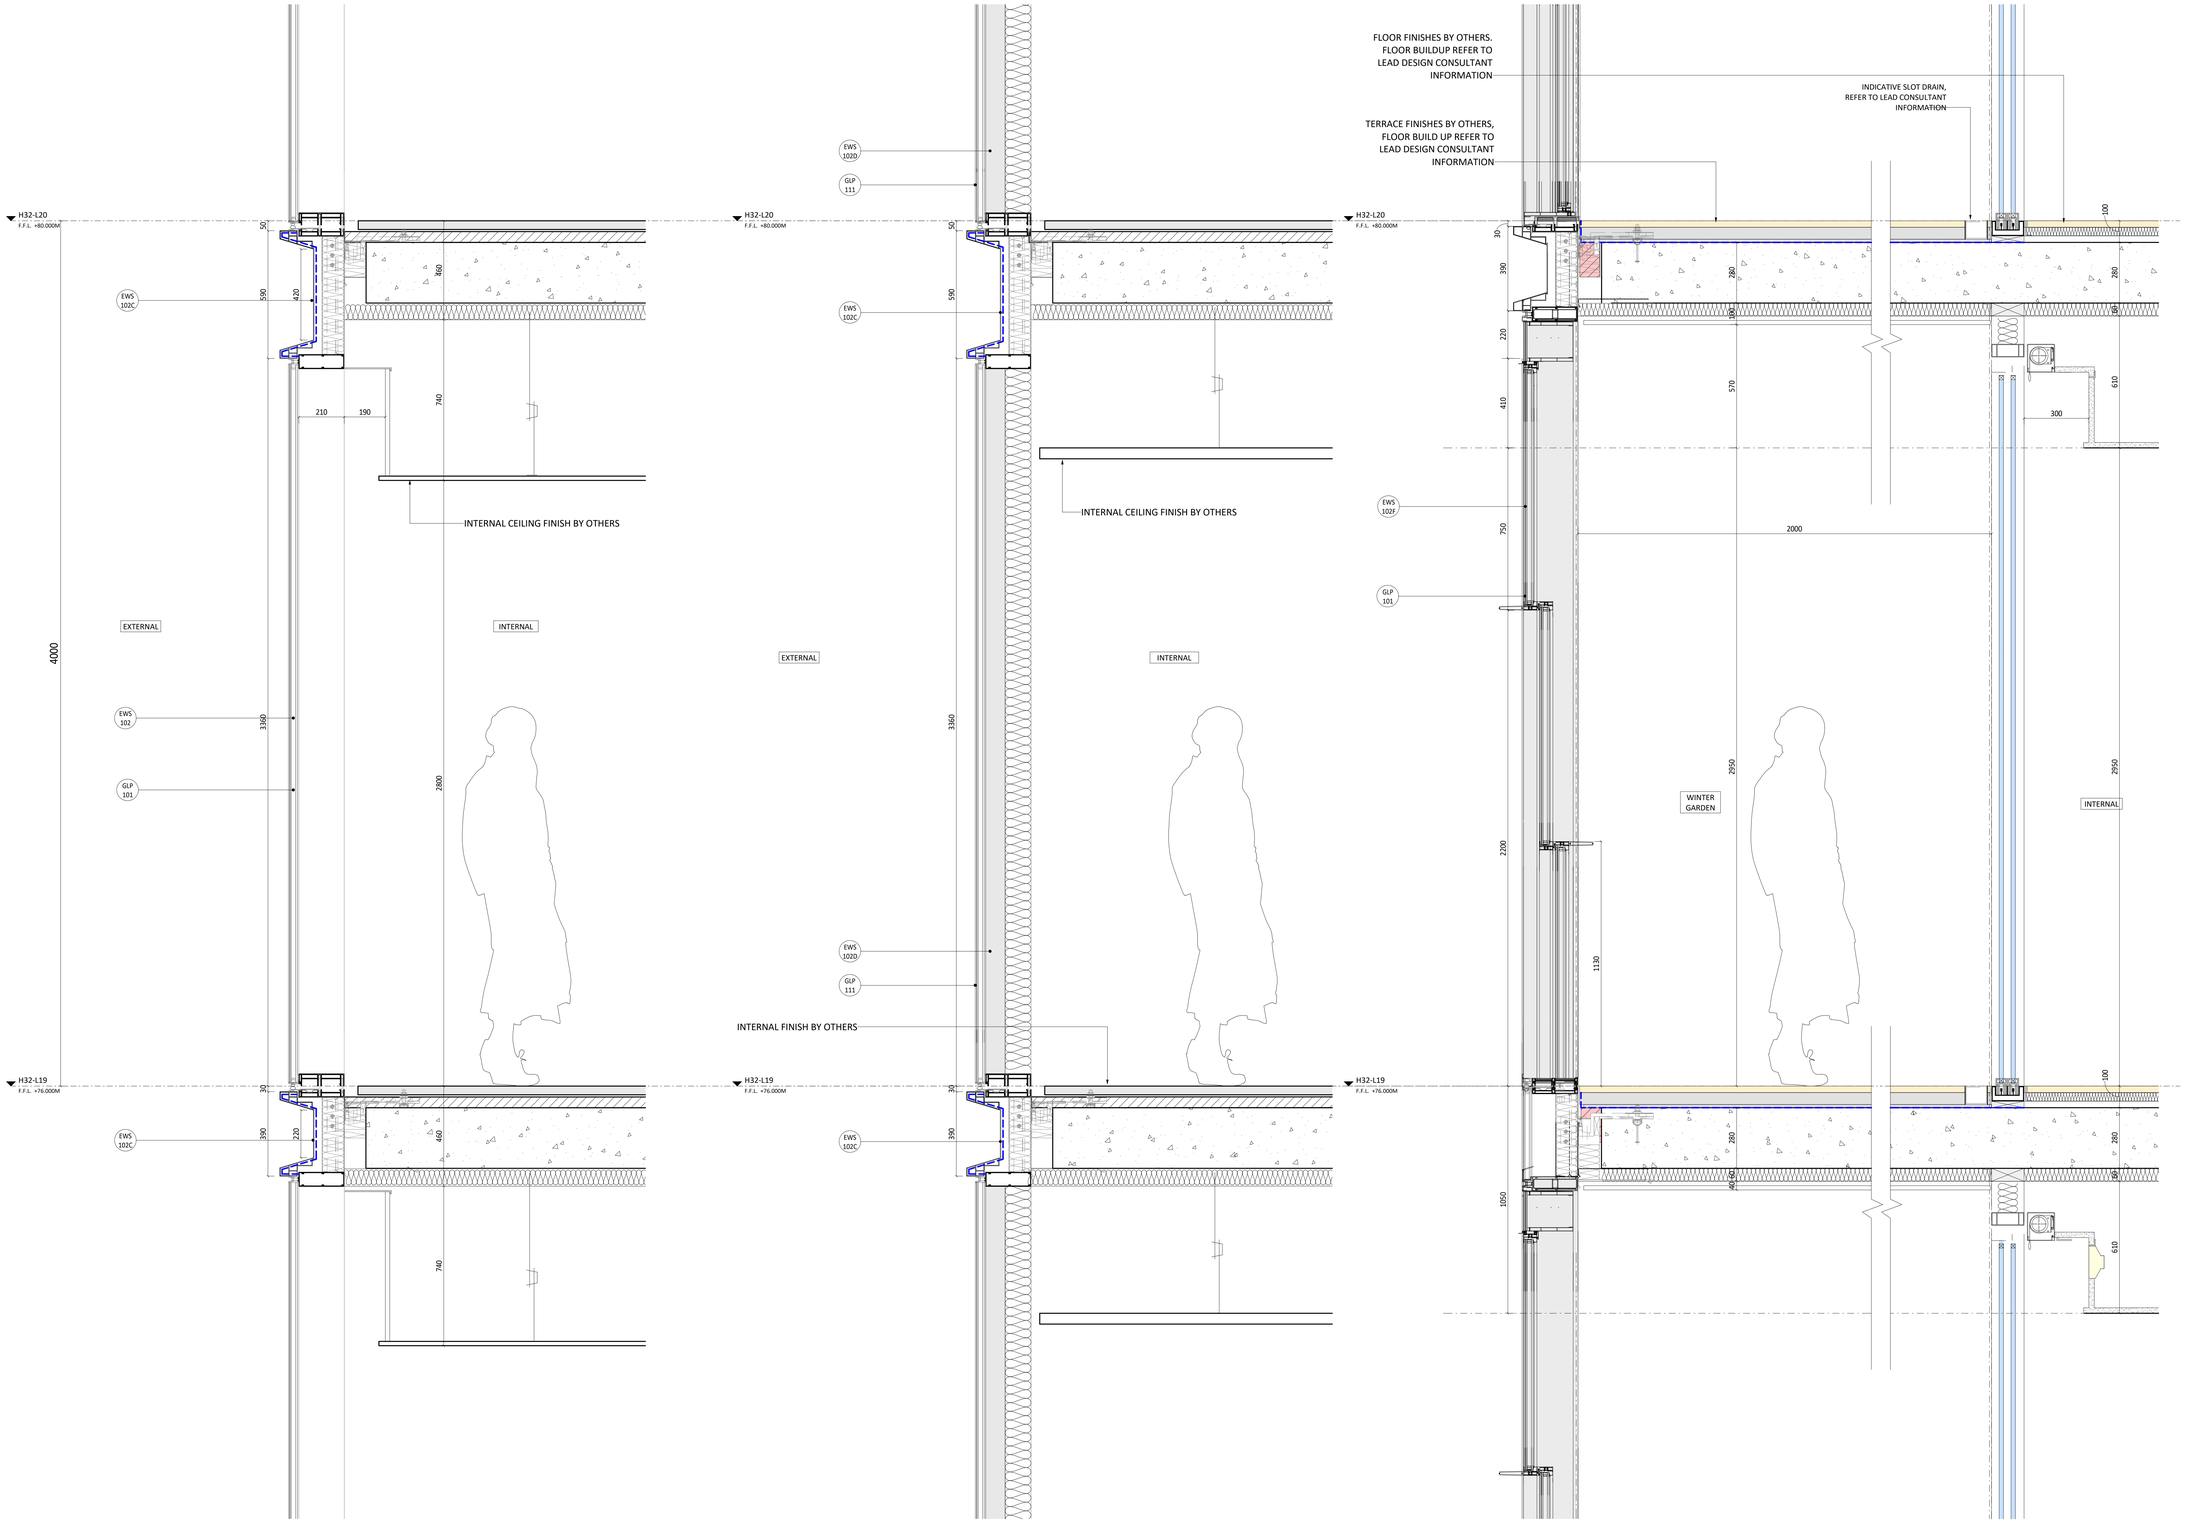


1 SECTION - FACADE TYPE 01 - UNITIZED GLAZING - 300-600MM RINGS
1 : 10

2 SECTION - FACADE TYPE 01 - UNITIZED SHADOW BOX
1 : 10

3 SECTION - FACADE TYPE 02 - WINTERGARDEN TYPICAL
1 : 10


Client:

القديـــة
Qiddiya

Project Name / Logo:

Motorsport Hotel Complex
QC00912012

Key Plan

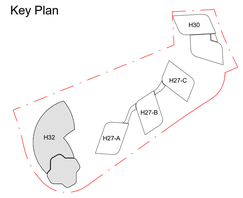

1:2000

Notes:

1. FOR STRUCTURAL INFORMATION REFER TO THE STRUCTURAL ENGINEERS DRAWINGS AND SPECIFICATIONS.

2. FOR SERVICES AND ENVIRONMENTAL INFORMATION REFER TO THE MEP ENGINEERS DRAWINGS AND SPECIFICATIONS.

3. REFER TO THE FAÇADE ENGINEERS DESIGN DOCUMENTS FOR:
- WORKS SPECIFICATION
- DETAILED DESIGN OF THE ILLUSTRATED FAÇADE TYPES
- BUILDING AND FAÇADE DIFFERENTIAL MOVEMENTS
- THERMAL, ACOUSTIC AND SECURITY PERFORMANCE REQUIREMENTS

4. ALL EXTERNAL WALL SYSTEMS ILLUSTRATED ARE THE AGREED DESIGN INTENT AND THE AGREED MATERIAL QUALITY. THE FAÇADE CONTRACTOR IS TO UNDERTAKE THE DETAILED DESIGN OF THE WORKS, COMPLYING WITH THE VISUAL INTENT INDICATED ON THE DESIGN DRAWINGS.

5. THE FAÇADE CONTRACTOR IS TO CO-ORDINATE WITH THE WORKS OF OTHERS, INCLUDING INTERFACES AS REQUIRED AND MAINTAIN PERFORMANCE AT INTERFACE CONDITIONS.

6. THESE DESIGN DRAWINGS ARE FOR THE SHELL AND CORE WORKS OF THE MOTORSPORTS HOTEL COMPLEX PROJECT.

7. ALL ARISING INTERFACES WITH THE INTERIOR DESIGN SCOPE OF WORKS IS TO BE MANAGED WITH QIC.

Rev. No	Description	Date	Checked
0A	100% DETAIL DESIGN	16-01-2025	EK

Lead Design Consultant:
SSH

SSH
www.sshic.com

Architect of Record:

المجموعة الإستشارية
Consultancy Group

Contractor:

Design Consultant:
WilkinsonEyre Architects

WilkinsonEyre

Drawing Title:

H32_WALL SECTIONS_TOWER

Reference File:
QC00912012-WEA-MOD-3DM-ARC-EV-H32-00010

Authored By:
-

Checked By:
Checker

Drawing Number:

Scale:
1 : 10@A0

Project ID	Orig.	Type.	Sub-DISC	DISC	Area	Venue	Seq.
QC00912012	SSH	DRW	DTL	ARC	EV	H32	32002