Revision		Date	By
A	New measurements, doors redrawn	2022-10-07	EB

Interior view, door closed

Interior view, door open

4.9T/27

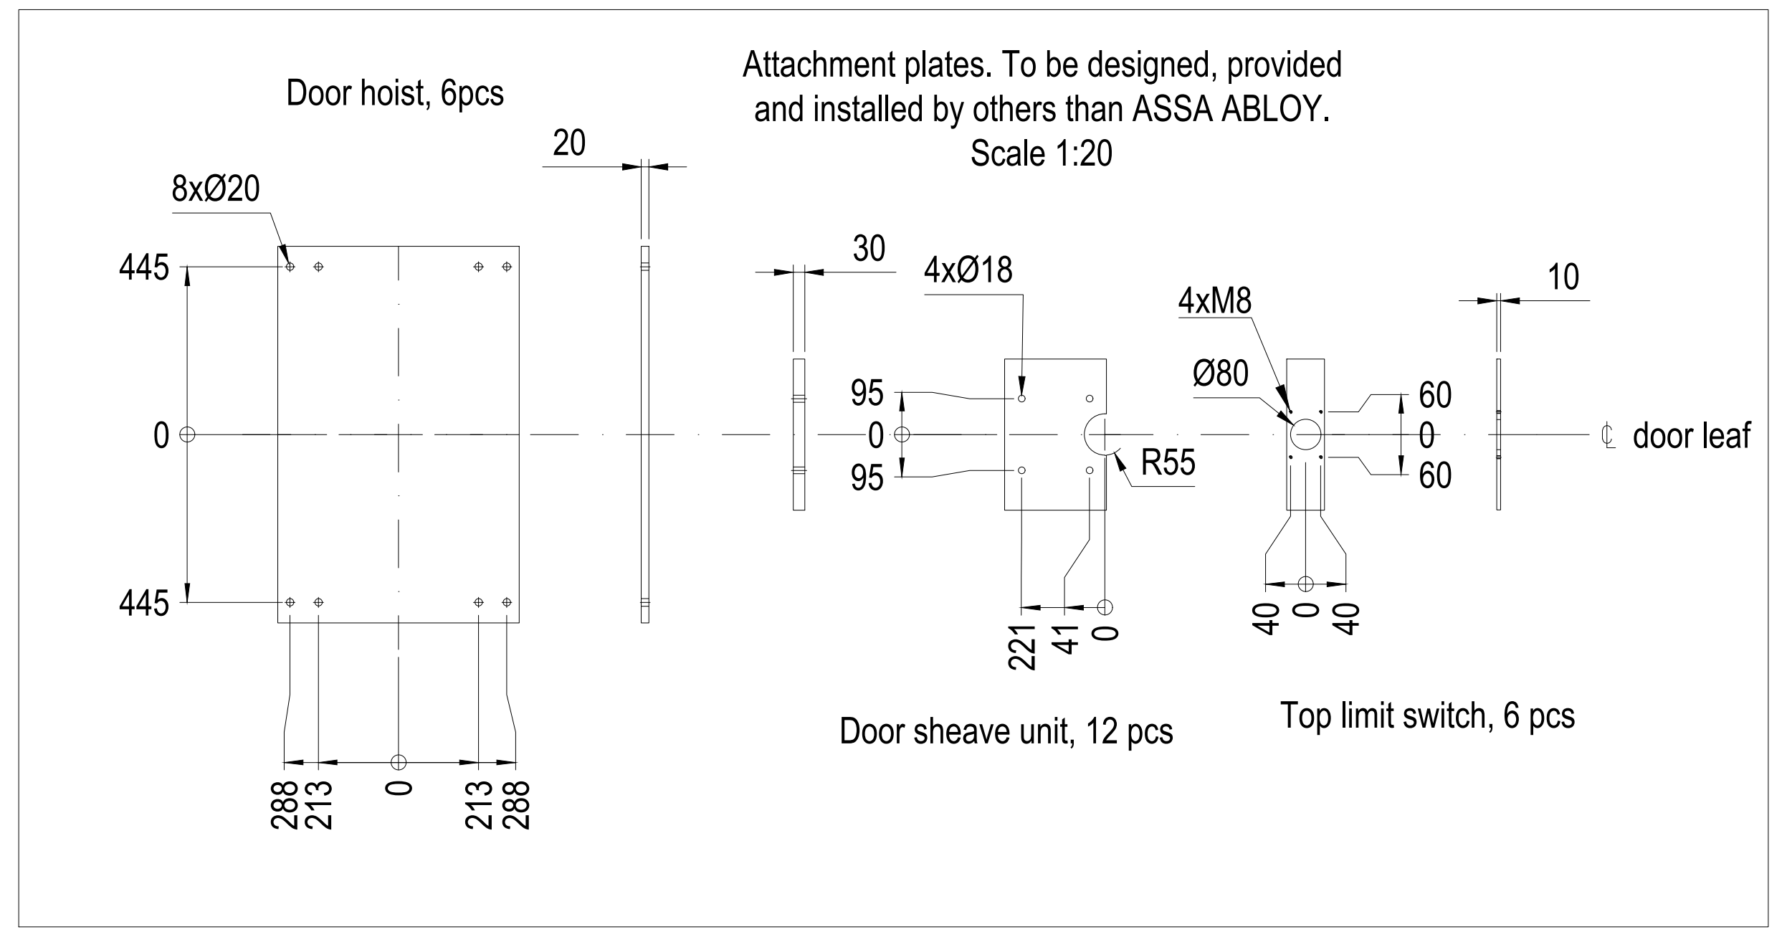

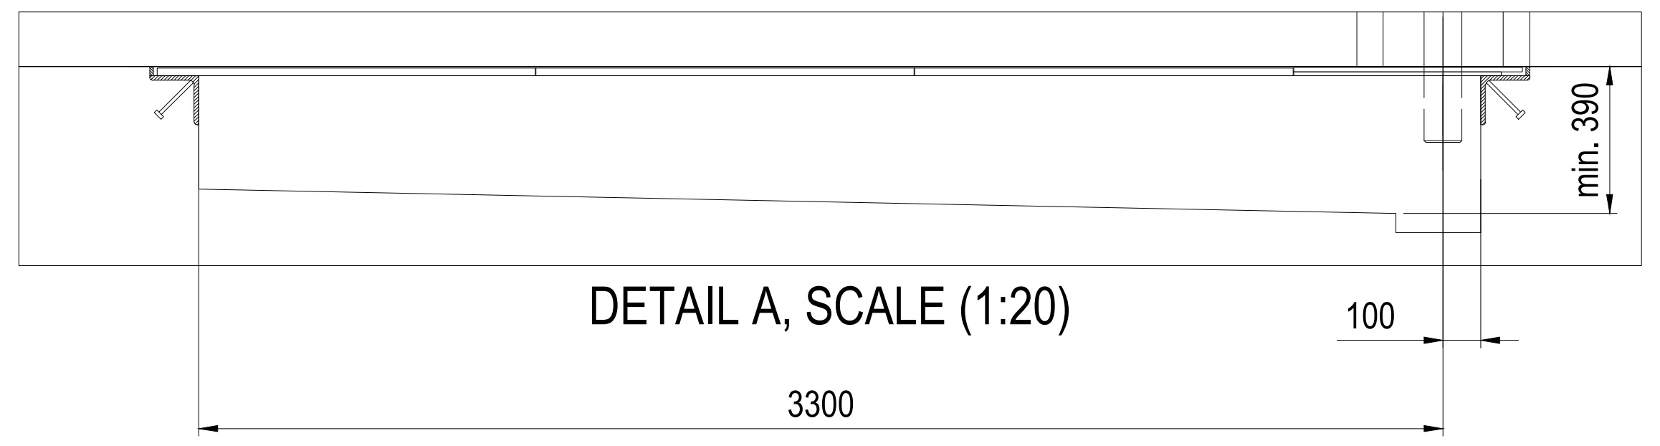

DETAIL A, SCALE (1:20)

DOOR IDENTITY NUMBER: 84801001

LOAD DIAGRAM & NOTES, ref. to drwng. no. 77450

INTERFACE, SECTIONS ref. to drwng. no. 77449

INTERFACE, PLAN VIEWS ref. to drwng. no. 77448

DESIGNED EB	SIZE A1F	SCALE 1:100	GMR Aero Technic Hangar2 India Megadoor 91136x14700/14000 Interface, Elevation
CODE 84801	If not otherwise stated: Tolerances ISO 2768-m EN ISO 13920-B Cutting class ISO 9013-442 Weld class ISO 5817-C Surface finish Smooth raw surface		PLOT DATE
ITEM NO			
DATE 2022-08-29			DRAWING NO 77447
ASSA ABLOY			REVISION A

This document is the property of ASSA ABLOY Entrance Systems AB and shall not without our written permission be copied, imparted to a third party or used for any other unauthorized purpose.