
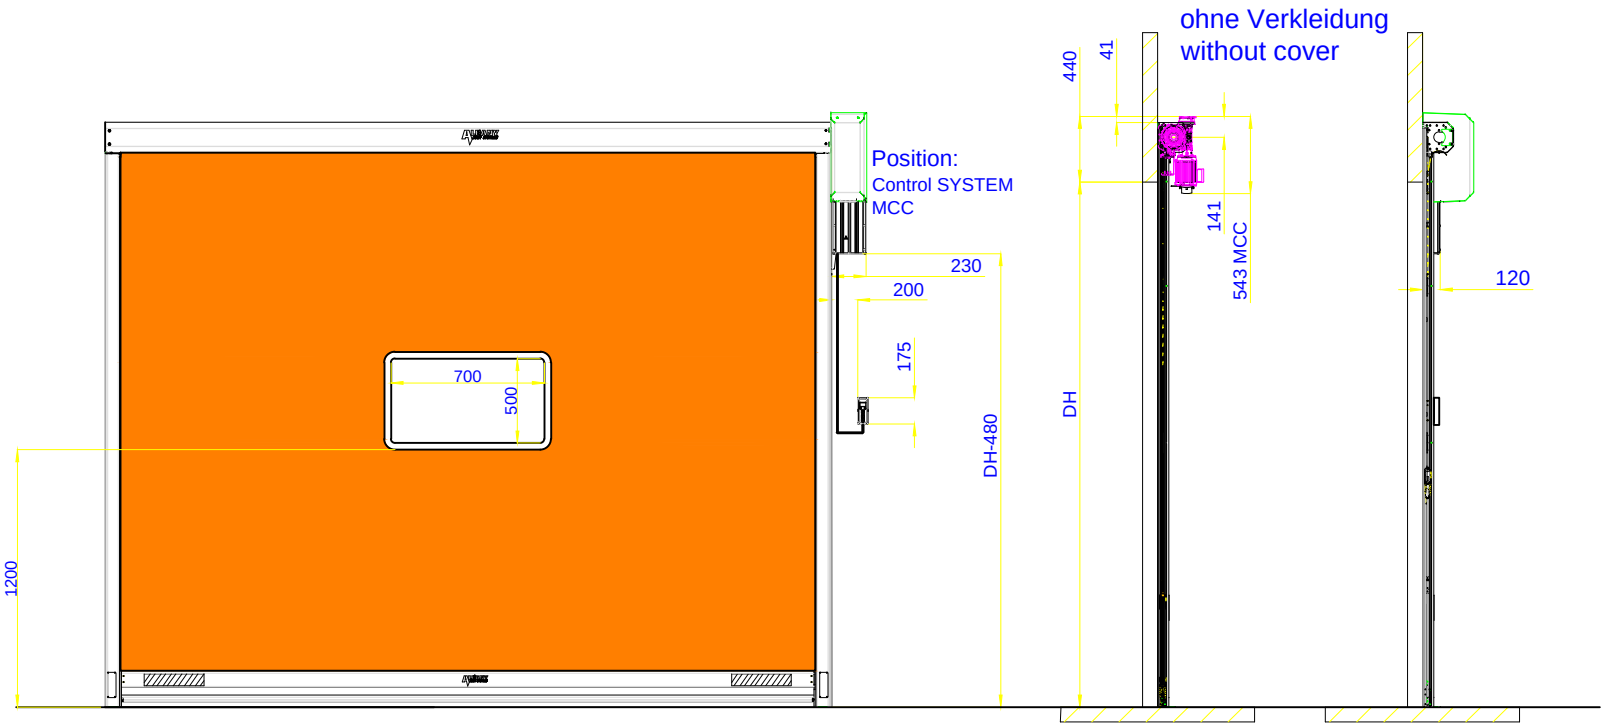


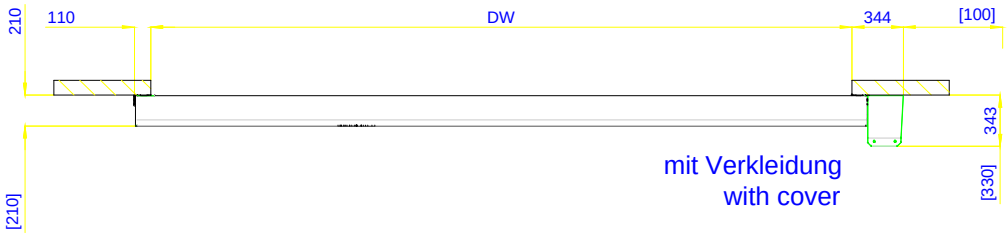

NOTE : RAL CODE - ORANGE 2009.

REV NO	REV DATE	DRAWN	REMARK
R01	05.11.2019	P.A	1. HEIGHT CHANGE 2. RAL CODE ADDED

Tolerance ±3 mm (for all dimensions)

Dimensions in [ ] ==> clearance for installation

This drawing & design is the property of NIHVA TECHNOLOGIES. Not to be sold or copied to any other concern.

TITLE: HIGH SPEED DOOR
RP300 WIDE

NIHVA TECHNOLOGIES PVT. LTD. PUNE
Tel : 020 66304033
Email:- info@nihva.com
Website:- www.nihva.com

	NAME	SIGN	DATE
DRAWN	P.V.A		01.10.19
CHECK	G.J		01.10.19
APPV'ED			

CLIENT :- WOOSHIN

PROJECT :-

LOCATION :-

If any queries contact : design@nihva.com

DWG. NO. :- NIHVA/19-20/0132/R01 REV.:-R01

ALL DIMENSION ARE IN mm

SCALE: NTS WT: SHEET: 01 OF 01

CLEAR WIDTH(DW)	CLEAR HEIGHT(DH)	QTY
4000 MM	3300 MM	04 NOS

NOTE : ALL CIVIL & STRUCTURAL WORK WILL BE IN CLIENT SCOPE.