
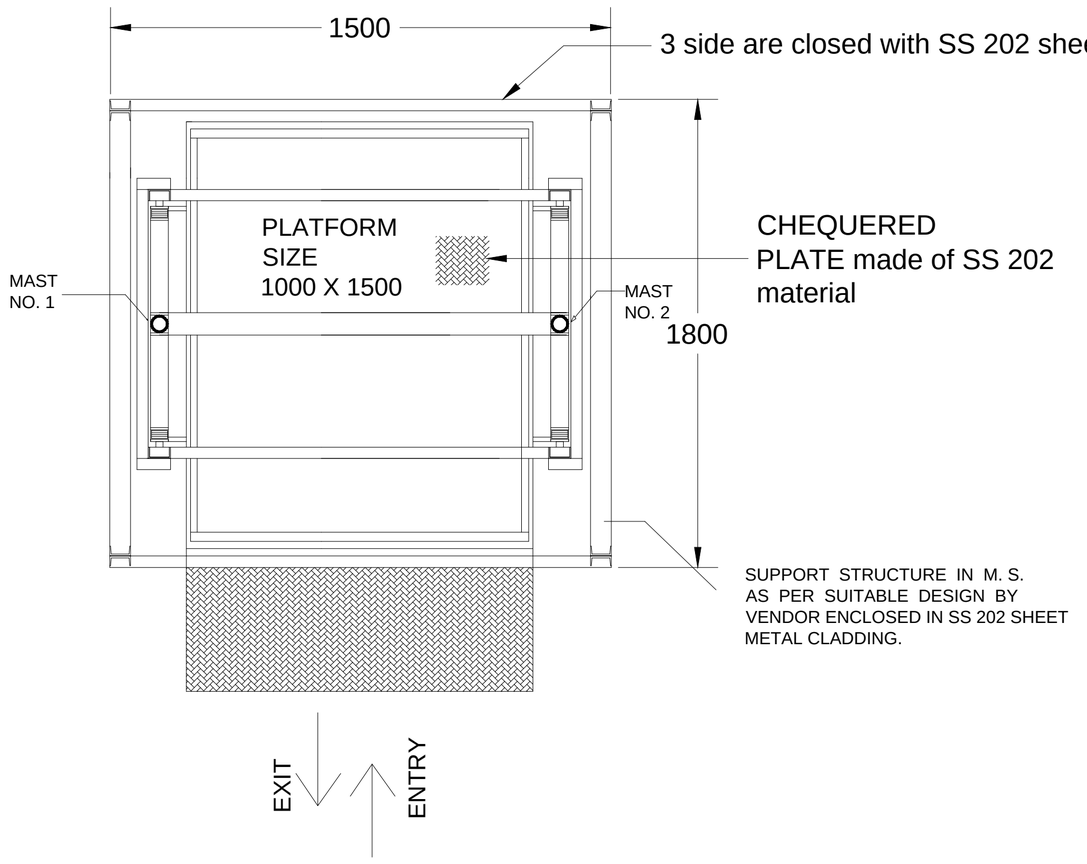


CAPACITY	1000 KGS
NO. OF FLOORS	GROUND + 1 FLOOR
PLATFORM SIZE	1000 mm X 1500 mm
LIFT HEIGHT	3000 mm
OPERATION	3 HP A. C. POWERPACK
NO. OF HYD. CYLINDERS	2 NOS
LIFTING SPEED	50-60 mm/s
NO. OF HYD. CYLINDERS	2 NOS
POWER SUPPLY	440VAC,3PH,50HZ

PLAN

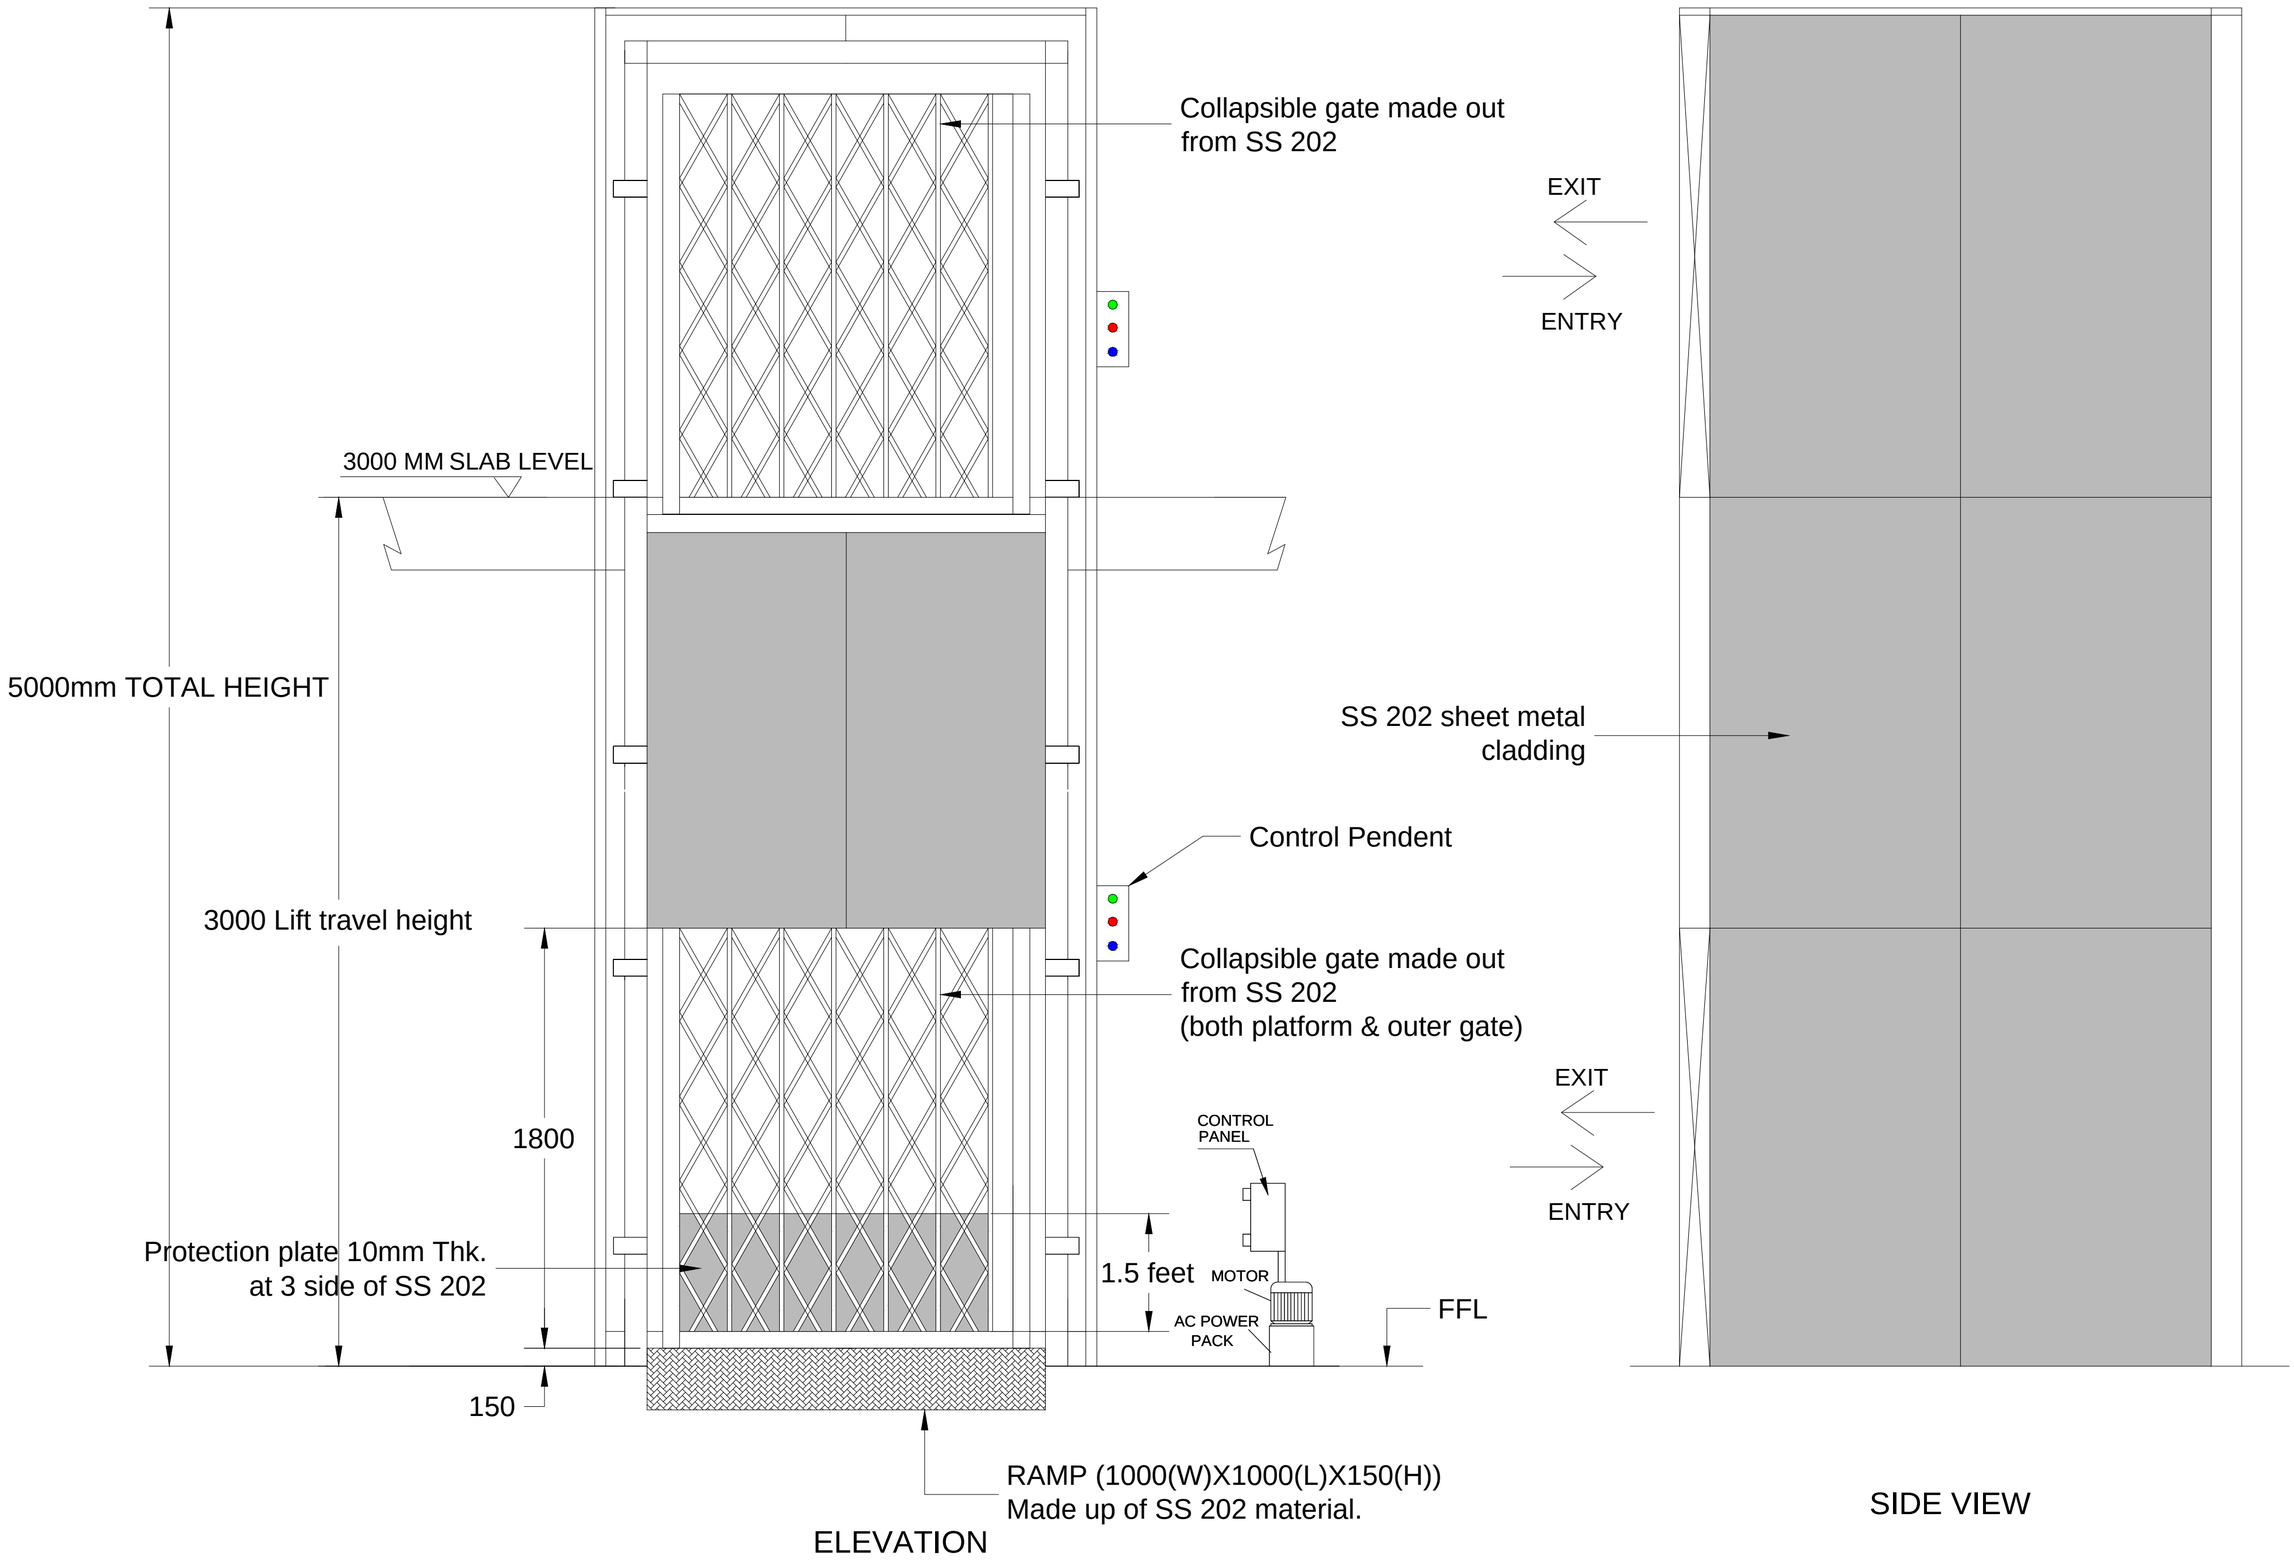

ELEVATION

SIDE VIEW

This drawing & design is the property of NIHVA TECHNOLOGIES. Not to be sold or copied to any other concern.

TITLE

GOODS LIFT G.A. DRG

CLIENT APPROVAL

ALL DIMENSION ARE IN mm

	SIGN	DATE
DRAWN	OMKAR	23/05/17
CHECK	SAGAR P.	23/05/17
REV.		
APPRD.		
MFG		
Ref. No.		

NIHVA TECHNOLOGIES PVT. LTD.

NIHVA TECHNOLOGIES
PVT. LTD. PUNE
Tel : 020 66304033
Email:- info@nihva.com
Website:- www.nihva.com

CLIENT -

PROJECT -

SITE -

DWG. NO. - NIHVA/16-17/VDR/0054

SCALE: NTS | WT: | SHEET: 01 OF 01

If any queries contact : projects@nihva.com