

Abbrevation's:
WOW-Wall Opening Width
WOH-Wall Opening Height
CH- Clear Height
UC-Under Cut
FFL-Finished Floor Level

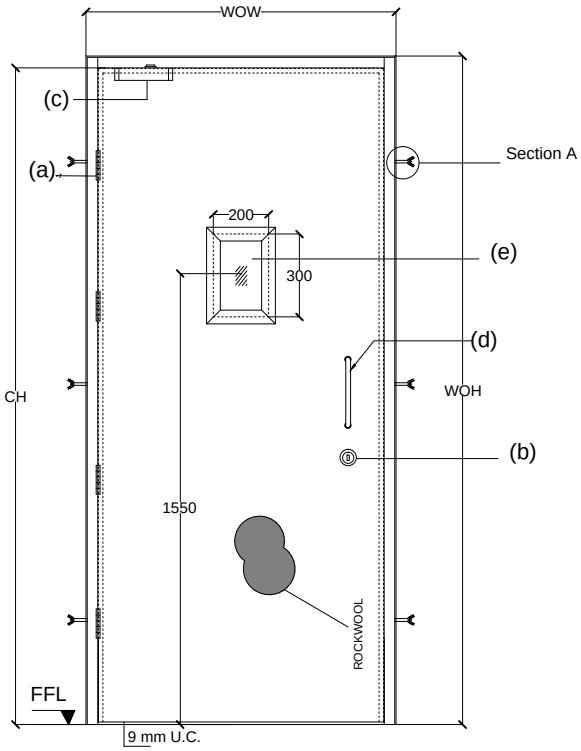

ELEVATION



TOP VIEW

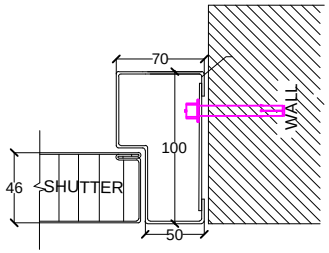

ACCESSORIES DETAILS

(a) HINGES.
(b) DOOR CLOSER.
(c) HANDLE : D Handle.
(d) VISION PANEL - 5mm THK. GLASS OF SIZE-200X300mm.

Door thickness : 46 mm
Frame Sheet thk : 1.5mm
Door sheet thk : 1.2mm
Fixing : On Soliid Brick plasterd wall with Anchors

NOTE:- *All Dimensions are in mm.
*Tolerance:-All Linear Dimensions ±3mm,Others ±0.5mm.
*The Drawing Is For Location of Hardware only. Drawing Does Not Represent The Hardware For More Clarity, Please Go Through Hardware Broucher.

Fire door size

WOW	WOH	TYPE 1	TYPE 2	TYPE 3	TYPE 4	QUANTITY
1250	2100					28

NOTE-

1. CLIENT SHOULD SELECT DOOR TYPE FROM ATTACHED DOOR HANDLING SHEET & COLOR OF DOOR.
2. THIRD PARTY FIRE RATED CERTIFICATE.
3. CLIENT SHOULD SELECT DOOR TYPE FROM ATTACHED DOOR HANDLING SHEET & COLOR OF DOOR.

This drawing & designing is the property of NIHVA TECHNOLOGIES. Not to be sold or copied to any other concern.

TITLE: FIRERATED STEEL DOOR

	NAME	SIGN	DATE
DRAWN	A.K.		21.01.2019
CHECK	P.A.		21.01.2019
APPROVAL	R.D.		21.01.2019
MFG.			

If any queries contact : projects@nihva.com

ALL DIMENSION ARE IN mm

NIHVA TECHNOLOGIES PVT. LTD.
NIHVA TECHNOLOGIES PVT. LTD. PUNE
Tel : 020 66304033
Email:- info@nihva.com
Website:- www.nihva.com

CLIENT- ESR PUNE
PROJECT - BMW
SITE -. CHAKAN, PUNE
DWG. NO. : NIHVA/18-19/0244 REV. : 00
SCALE: NTS WT: SHEET: 01 OF 01