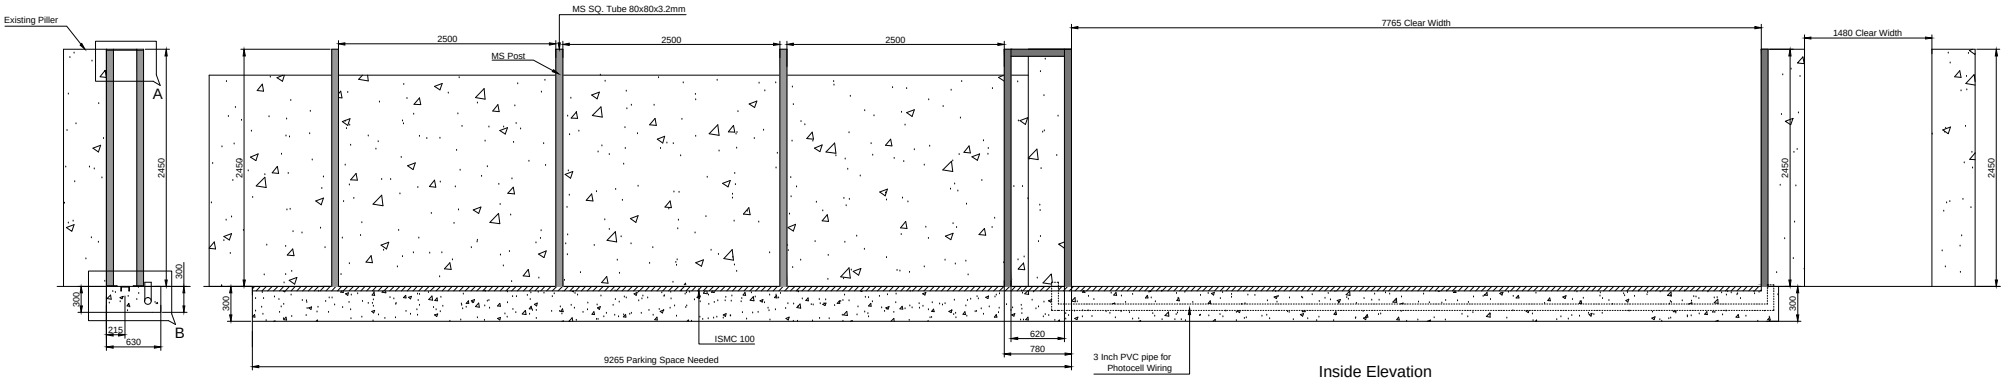

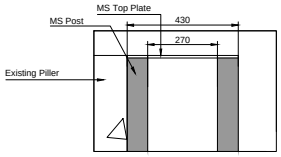

Detail view of A

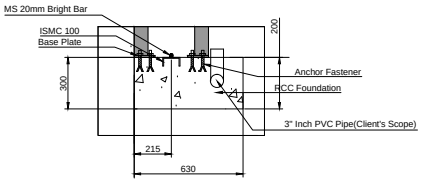

Detail view of B

SR NO	CLEAR WIDTH	CLEAR HEIGHT	QUANTITY
1	7765mm	2400mm	1 NOS

This drawing & designing is the property of NIHVA TECHNOLOGIES. Not to be sold or copied to any other concern.

TITLE
Foundation of Motorized Sliding gate 7.765x2.4m

NIHVA TECHNOLOGIES PVT. LTD.
NIHVA TECHNOLOGIES PVT. LTD., PUNE
Tel : 020 66304033
Email:- info@nihva.com
Website:- www.nihva.com

	SIGN	DATE
DRAWN	Omkar	06/02/18
CHECK	Shekhar	06/02/18
APPROVAL	Shekhar	06/02/18

CLIENT - DEV TECNOSKILL
PROJECT - AMAR TEA
SITE LOCATION - UMARGAON, GUJARAT
DWG. NO. : NIHVA/17-18/0355 Rev- 0
If any queries contact : design@nihva.com
SCALE: NTS WT: SHEET: 01 OF 01
ALL DIMENSION ARE IN mm