


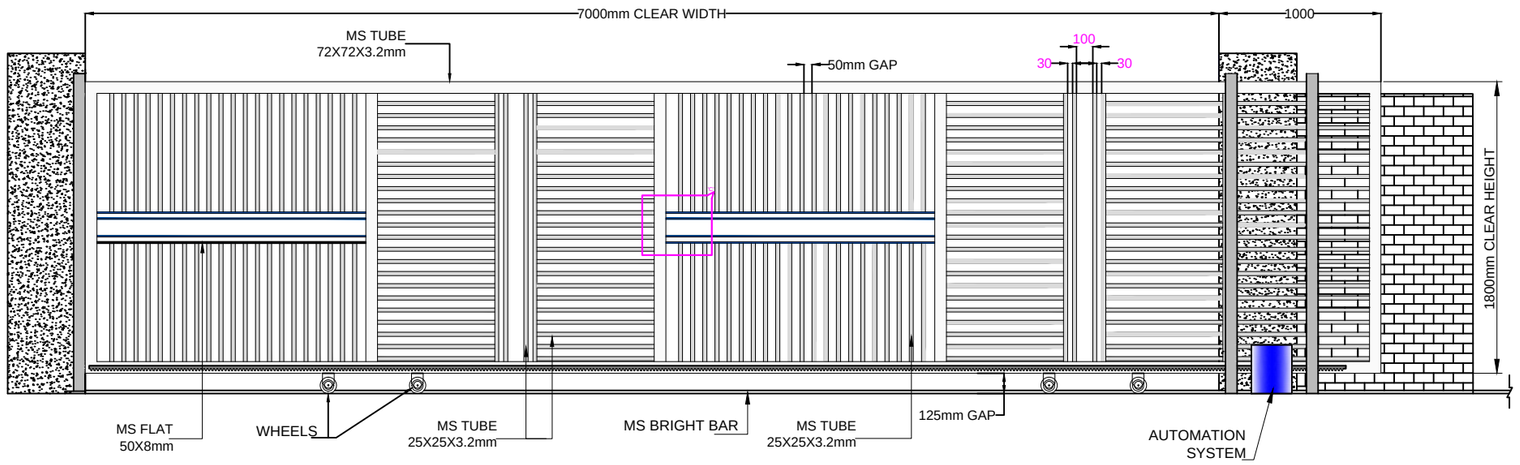


ELEVATION

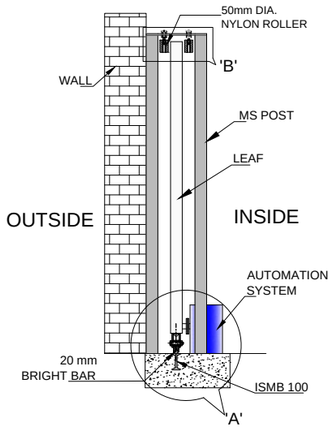


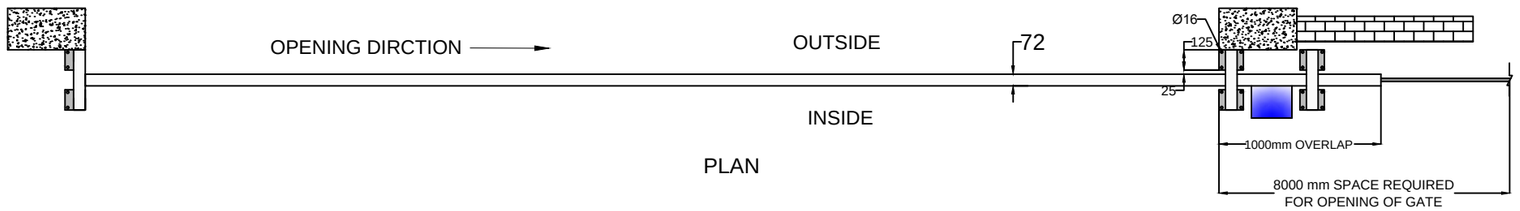


PLAN

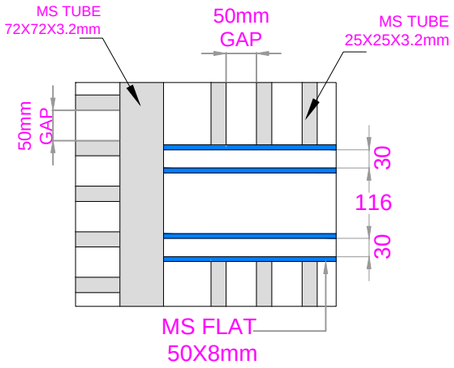

DETAIL VIEW OF 'C'.

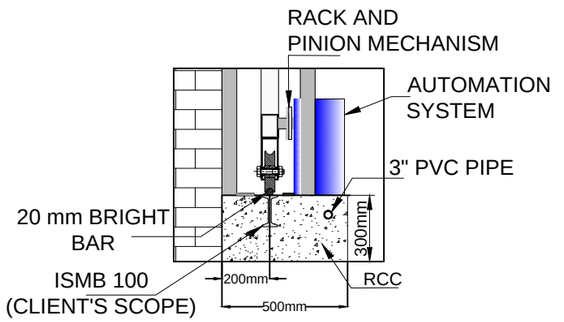

DETAIL VIEW OF 'A'.

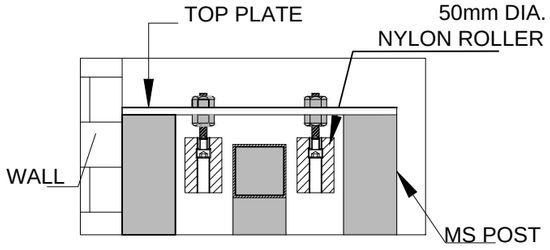

DETAIL VIEW OF 'B'.

TOLERANCE - ±10mm

NOTE-
1. ALL REQUIRED CIVIL WORK WILL BE IN CLIENTS SCOPE.
2. ONE COAT OF RED OXIDE & TWO COAT OF APPROVED RAL SHADE WILL BE GIVEN TO THE GATE.

SR NO	CLEAR WIDTH	CLEAR HEIGHT	QTY.
1	7000mm	1800mm	01NOS

REV:- 22-03-2018.
(1) ELECTRICAL DETAILS ADDED IN DRAWING.

electromechial motor–1500kg
Power supply – Single phase 230V, 50 Hz.
Cable for power supply– 1.5 sqmm 3 core
Cable for Photocell – 0.5 sqmm 4 core, length– 12m

This drawing & design is the property of NIHVA TECHNOLOGIES. Not to be sold or copied to any other concern.

TITLE
MOTORIZED SLIDING GATE

	NAME	SIGN	DATE
DRAWN	SURAJ		16-03-2018
CHECK	OMKAR		16-03-2018
APPRD.	SHEKHAR		16-03-2018

If any queries contact : design@nihva.com

ALL DIMENSION ARE IN mm

NIHVA
NIHVA TECHNOLOGIES PVT. LTD.

NIHVA TECHNOLOGIES
PVT. LTD. PUNE
Tel : 020 66304033
Email:- info@nihva.com
Website:- www.nihva.com

CLIENT - SCON PROJECT
PROJECT - ARI ARMATUREN STEAMLINE LLP
SITE LOCATION -PUNE
DWG. NO. : NIHVA/17-18/0399/R01.
REV- 01
SCALE: NTS
WT:
SHEET: 01 OF 01

22-03-2018 16:17:56