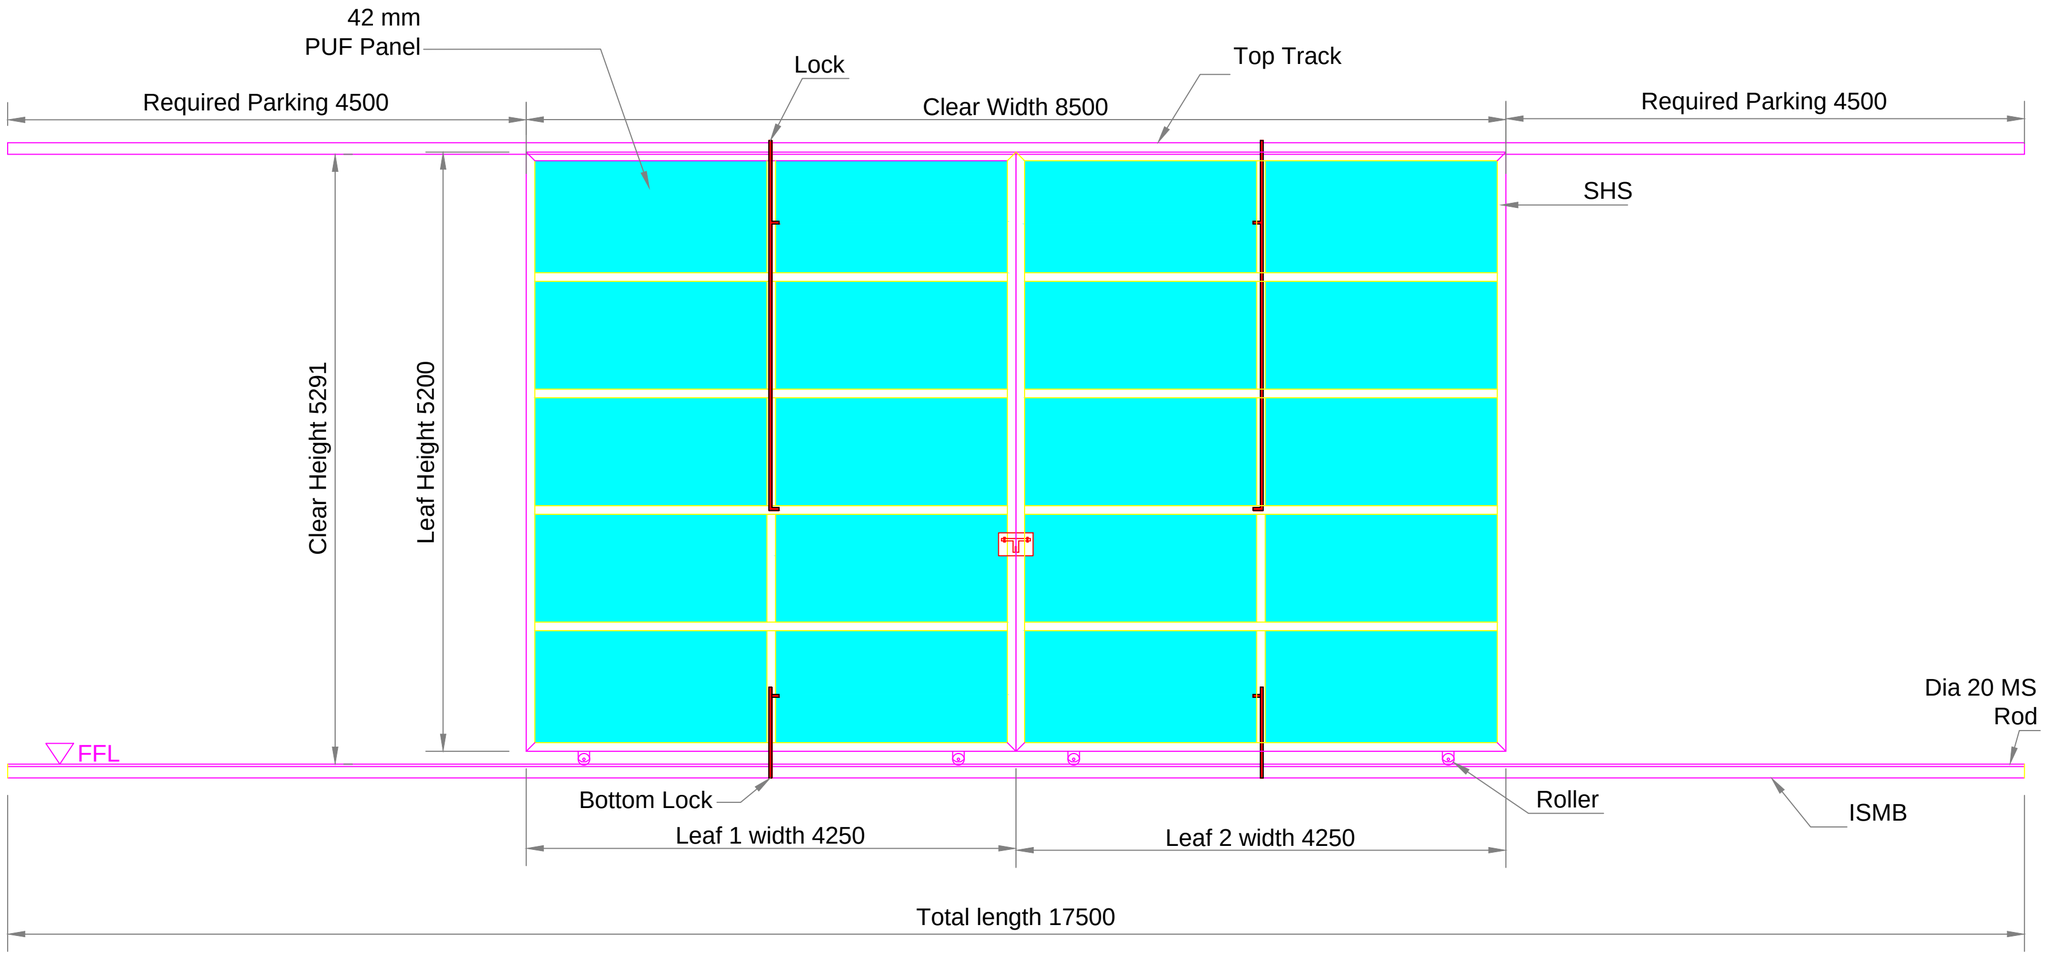


CLEAR WIDTH(DW)	CLEAR HEIGHT(DH)	QTY
8500mm	5200mm	15 NO

Note:
1. All civil work and structural work is in client scope.(If required)
2. For smooth moment of door:
   a) Uneven floor surface need to be clear.
   b) All the obstacles needs to be removed (Pipes/ fabrication/ Column/ beam/ perlin)
   c) We need clear space for assembly and installation of top track and bottom track.

This drawing & design is the property of NIHVA TECHNOLOGIES. Not to be sold or copied to any other concern.

TITLE	SLIDING DOOR 8500 X 5200			NIHVA TECHNOLOGIES PVT. LTD. PUNE Tel : 020 66304033 Email:- info@nihva.com Website:- www.nihva.com	
	NAME	SIGN	DATE		
DRAWN	G.P.		10.11.21	CLIENT :- Lestech Engineering India Pvt. Ltd.	
CHECK	P.J.		10.11.21	PROJECT :- POSCO	
	A.K.		10.11.21	LOCATION :- Mangaon	
If any queries contact : design@nihva.com				DWG. NO. :- NIHVA/21-22/0260	REV:- R00
ALL DIMENSION ARE IN mm				SCALE:NTS	WT: SHEET:01 OF 01