

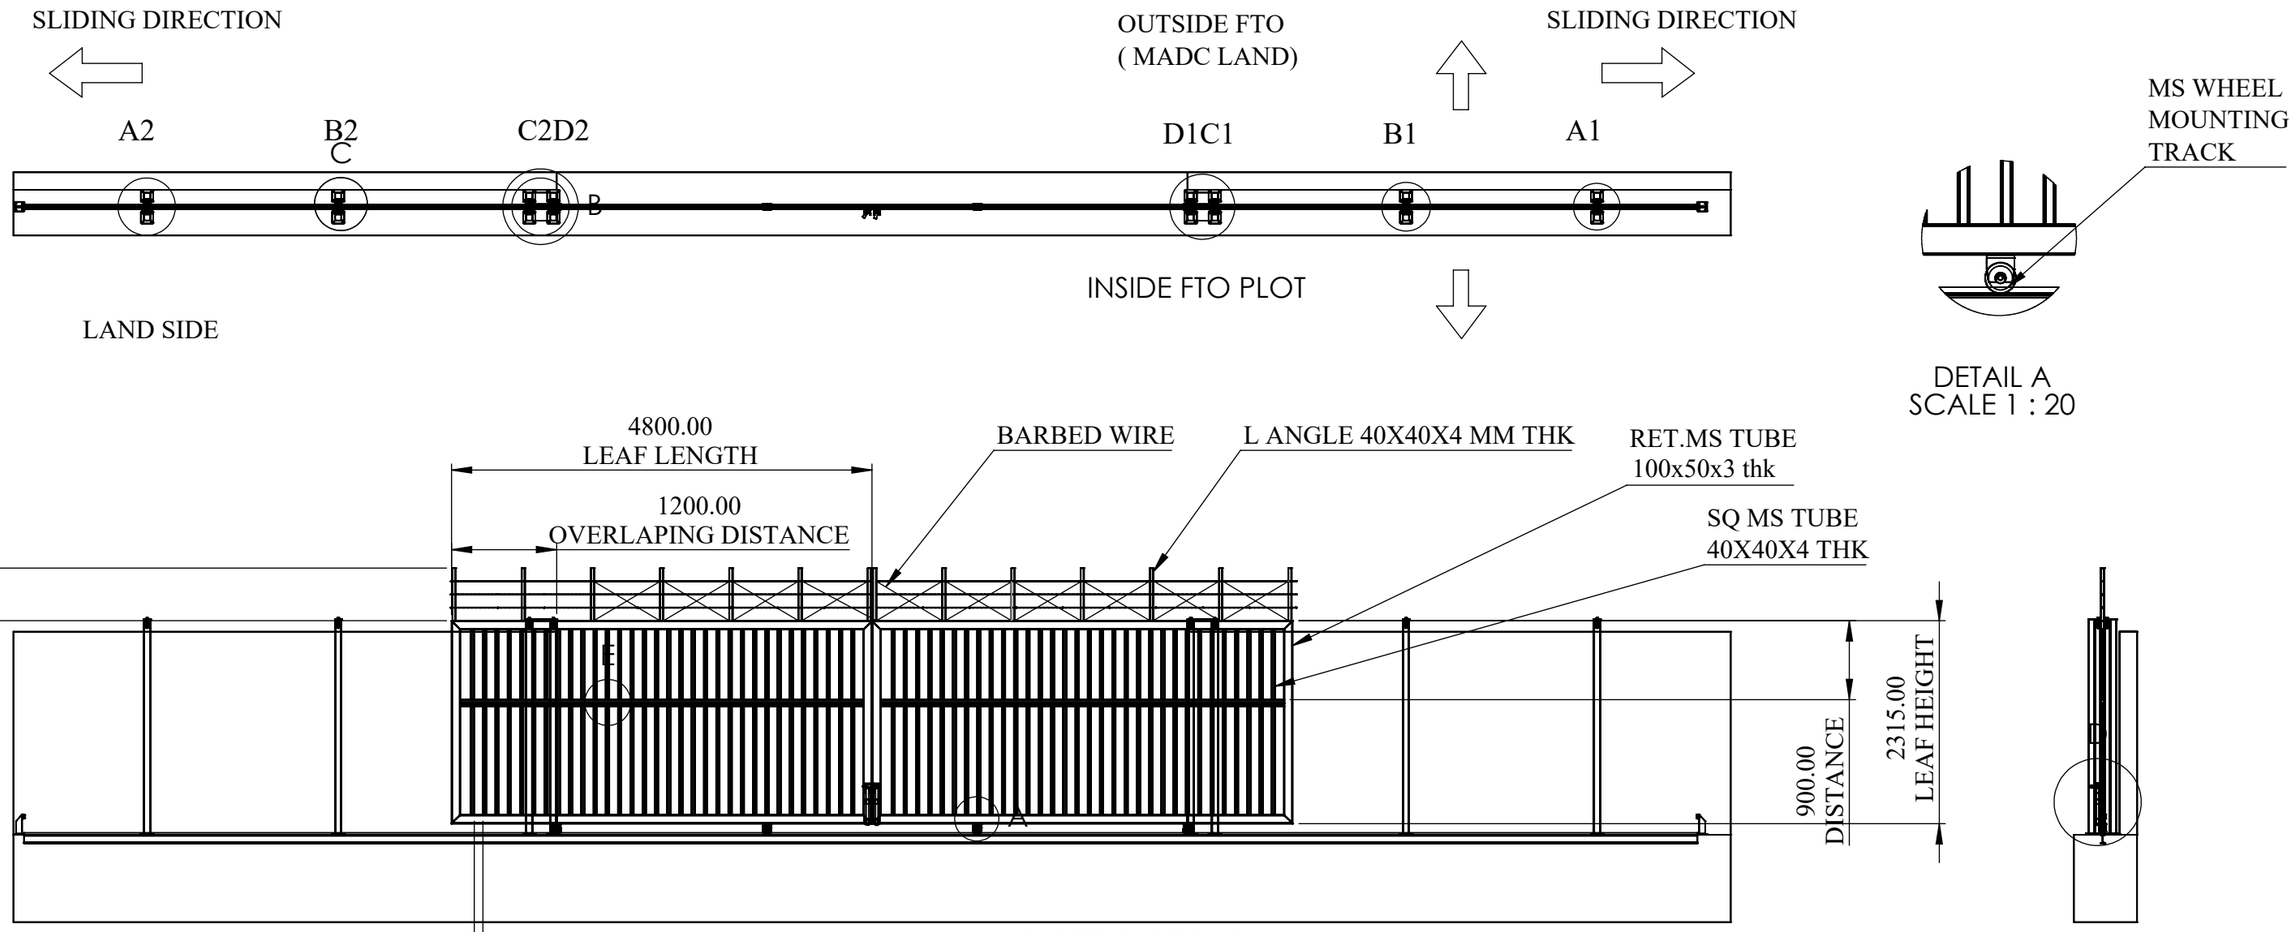


DETAIL A
SCALE 1 : 20

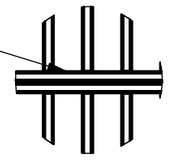


DETAIL E
SCALE 1 : 22

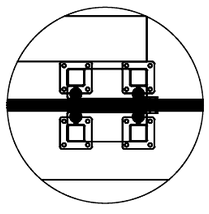


DETAIL B
SCALE 1 : 27

POST AND NYLON
BEARING ASM

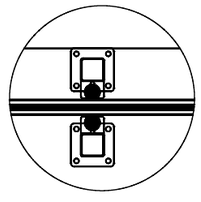

DETAIL C
SCALE 1 : 20

POST2 AND NYLON
BEARING ASM

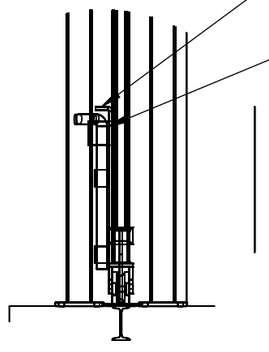


DETAIL D
SCALE 1 : 18


TOWER BOLT LOCKING
ARRANGEMENT

NOTE: 1) GA DRAWING TYPE 02
2) BARBED WIRE DESIGN IS ZIGZAG PATTERN.
3) Total Column-8 (A1,B1,C1,D1 Same as right side add 4 Post)
4) 04 column posts when the gate is in the closed position. (C1,D1) & C2,D2)
5) 08 column posts when the gate is in the open position (A1,B1,C1,D1& A2,B2,C2,D2)

TITLE - GATE AUTOMATION				NIHVA TECHNOLOGIES PVT.LTD.PUNE Website - www.nihva.com
DWG NO - NTPL-290-PM-002			QTY - 1	
	NAME	SIGNATURE	DATE	PROJECT NO - NTPL-290-PM
DRAWN	V.B.		29-07-2025	PRODUCT - BYPARTING SLIDING GATE
CHK'D	B.S.		29-07-2025	SITE LOCATION - AMRAVATI
APPV'D	V.T.		29-07-2025	TYPE 2
if any queries contact - supportautomation@nihva.com				REVISION -00
ALL DIMENSION ARE IN mm			A3	SCALE - SHEET 1 OF 1

ITEM NO.	PART NUMBER	DESCRIPTION	QTY.
1	BY PARTING SLIDING GATE	4800 WX2315 H	2
2	WHEEL AND PLATE ASM	4 INCH WHEEL	4
3	L ANGLE (40X40X4)	(L)- 600	14

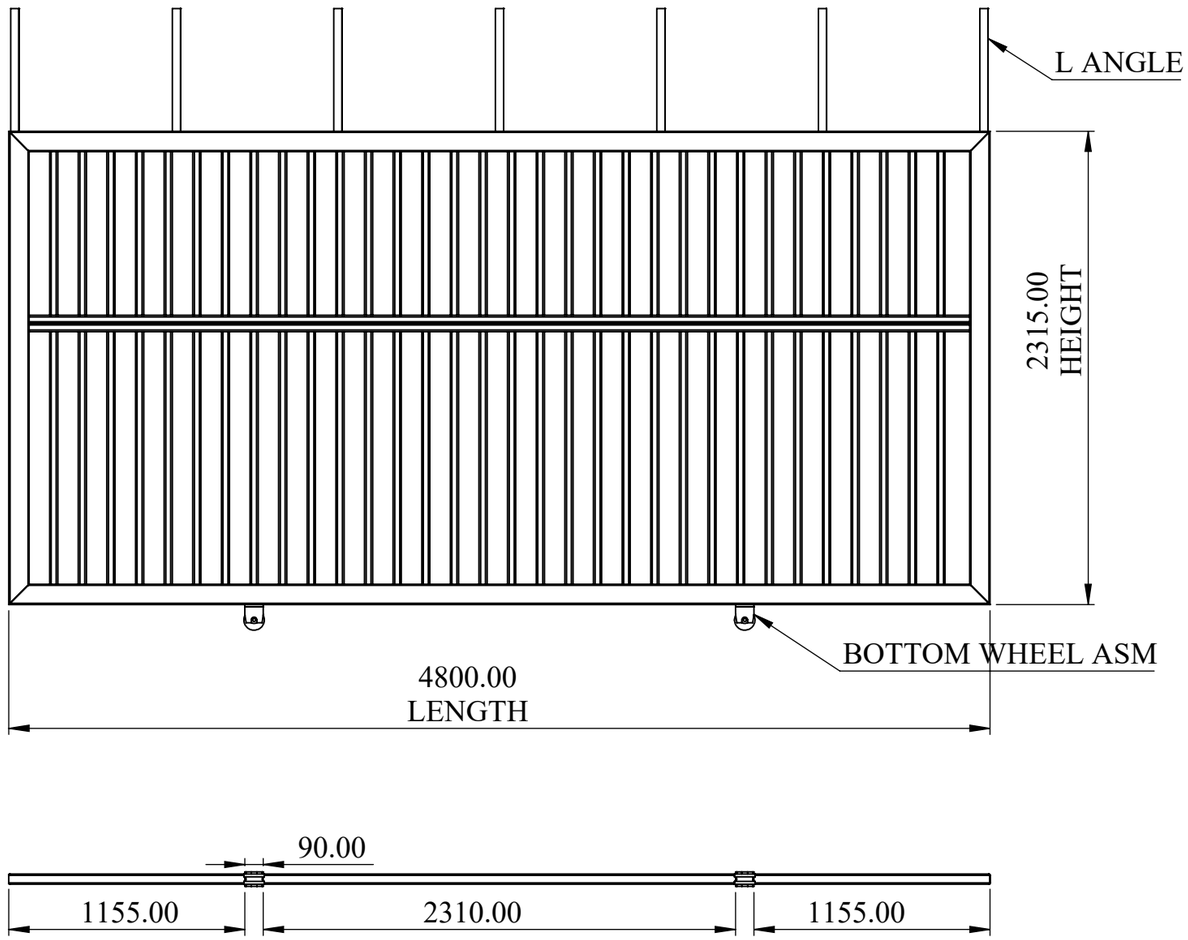


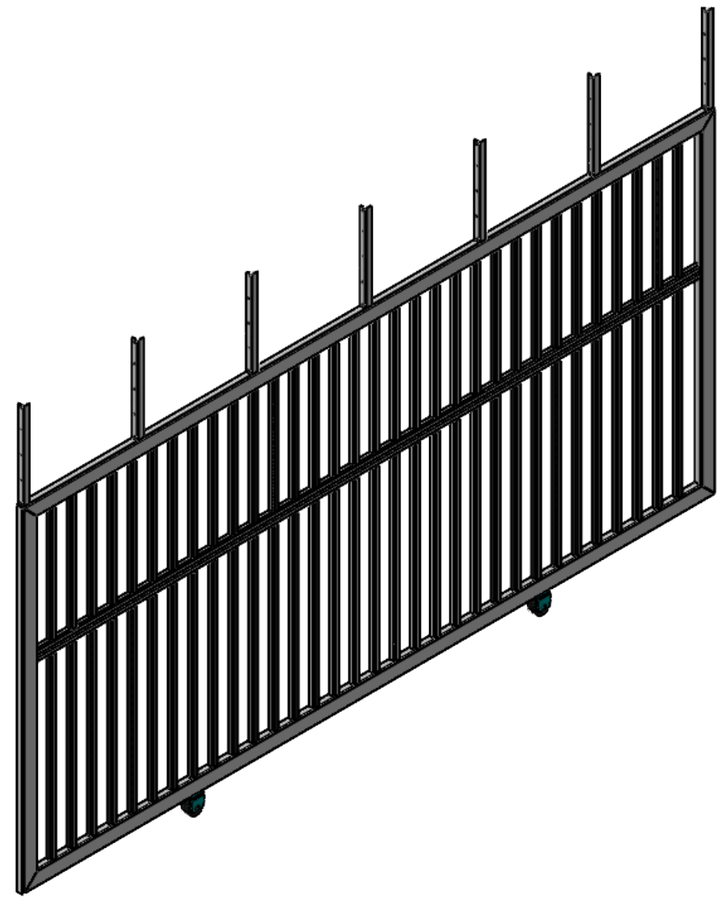


SLIDING LEAF- 2 NOS


TITLE - GATE AUTOMATION				NIHVA TECHNOLOGIES PVT.LTD.PUNE
DWG NO - NTPL-290-PM-002-01				Website - www.nihva.com
	NAME	SIGNATURE	DATE	PROJECT NO - NTPL-290-PM
DRAWN	V.B.		12-08-2025	PRODUCT - BY PARTING SLIDING GATE
CHK'D	B.S.		12-08-2025	SITE LOCATION - AMRAVATI
APPV'D	V.T.		12-08-2025	TYPE 2
if any queries contact - design@nihva.com				REVISION -00 / QTY - 1
ALL DIMENSION ARE IN mm		A3		SCALE - / SHEET 1 OF 19


ITEM NO.	PART NUMBER	DESCRIPTION	QTY.
	OUTER FRAME	100X 50 X 3 THK	8
	VERTICAL INNER TUBE	40X 40 X 4 THK	64
	VERTICAL INNER TUBE	40 X 40 X 4 THK	64
	HORIZONTAL INNER TUBE	40X40X4 THK	4

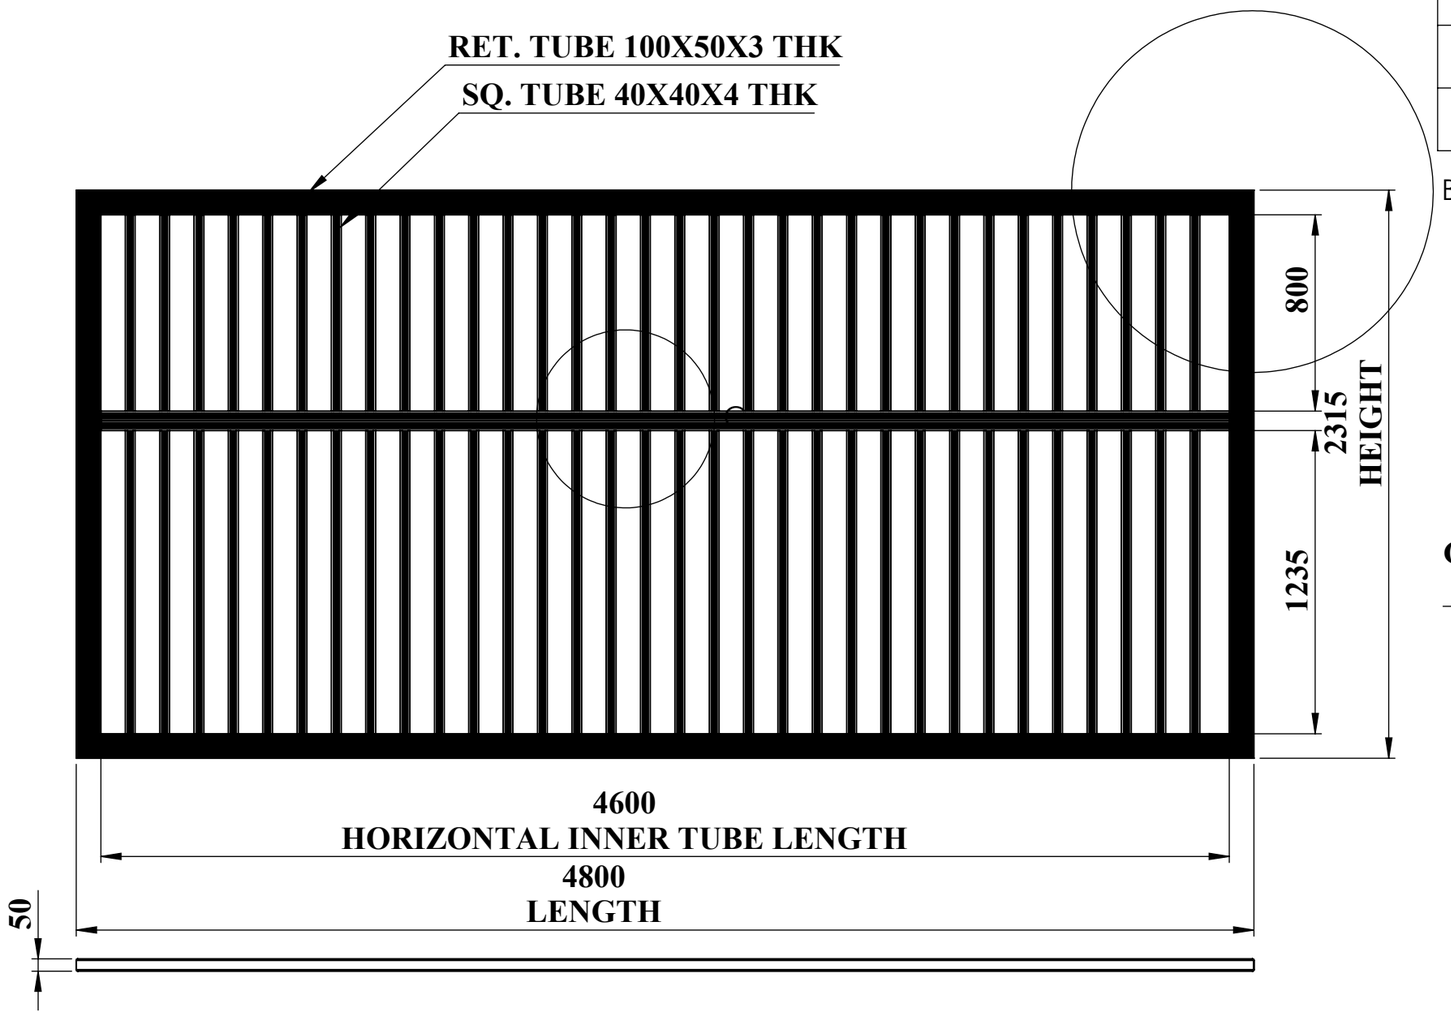

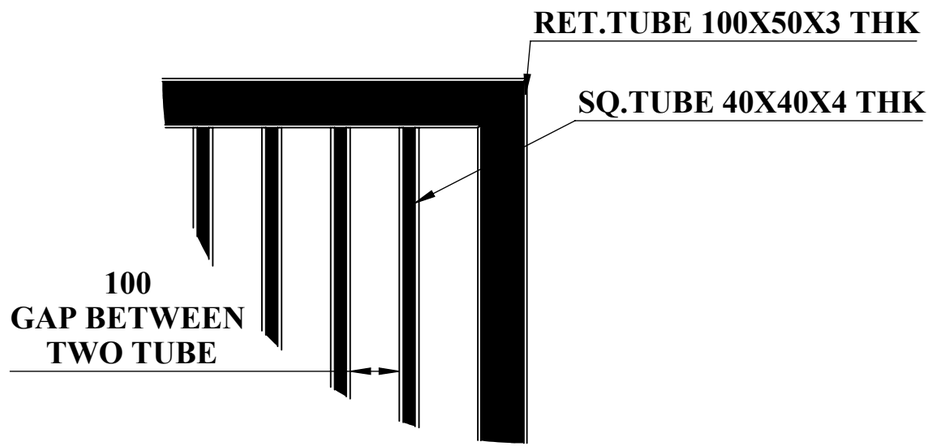

DETAIL B
SCALE 2 : 25

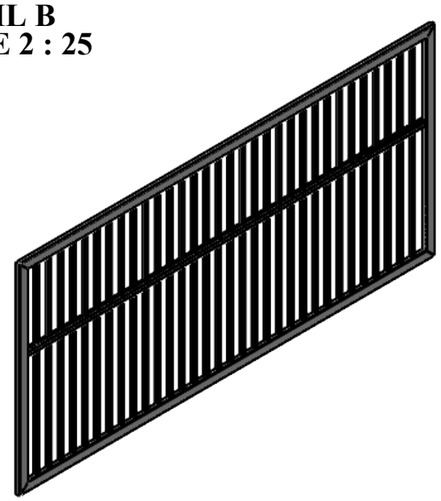


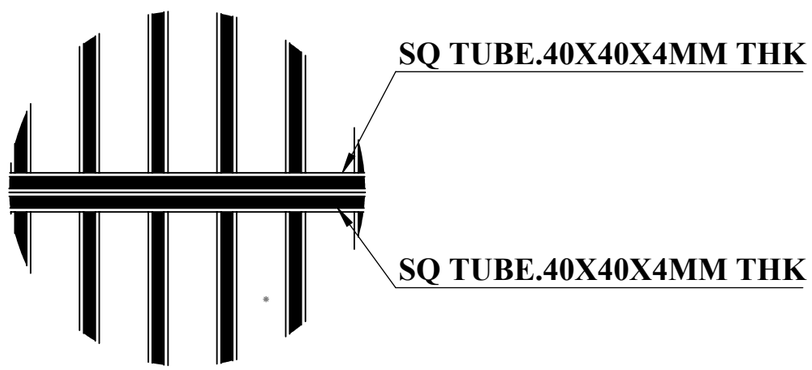


DETAIL C
SCALE 2 : 25

SUPPORT TUBE-
HORIZONTAL SUPPORT TUBE- 4 NOS
VERTICAL SUPPORT TUBE- 64 NOS (800MM)
VERTICAL SUPPORT TUBE - 64 NOS (1235MM)

TITLE - GATE AUTOMATION				NIHVA TECHNOLOGIES PVT.LTD.PUNE
DWG NO - NTPL-290-PM-002-01-01				Website - www.nihva.com
	NAME	SIGNATURE	DATE	PROJECT NO - NTPL-290-PM
DRAWN	V.B.		12-08-2025	PRODUCT - BY PARTING SLIDING GATE
CHK'D	B.S.		12-08-2025	SITE LOCATION - AMRAVATI
APPV'D	V.T.		12-08-2025	TYPE-2
if any queries contact - design@nihva.com				REVISION -00 / QTY - 1
ALL DIMENSION ARE IN mm		A3		SCALE - / SHEET 2 OF 19

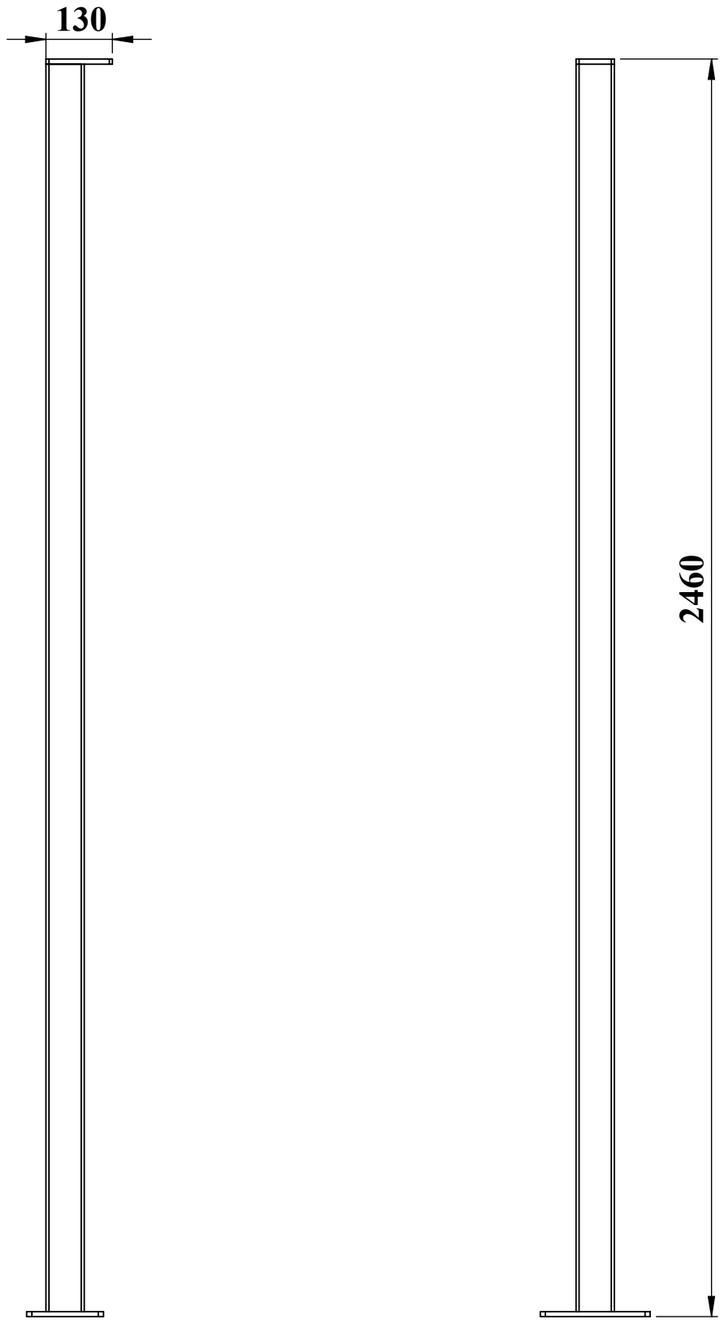

ITEM NO.	PART NUMBER	DESCRIPTION	QTY.
1	BOTTOM PLATE	215X150X10	16
2	SINGLE POST PLATE	130X75X10	8
3	VERTICAL TUBE	75X75X3	16

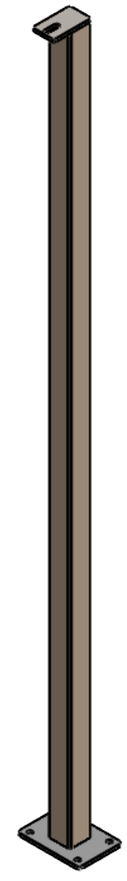



SINGLE POST ASM


QTY- 8 NOS

TITLE -GATE AUTOMATION				NIHVA TECHNOLOGIES PVT.LTD.PUNE Website - www.nihva.com
DWG NO - NTPL-290-PM-002-02				
	NAME	SIGNATURE	DATE	PROJECT NO - NTPL-290-PM
DRAWN	V.B.		12-08-2025	PRODUCT - BY PARTING SLIDING GATE
CHK'D	B.S.		12-08-2025	SITE LOCATION - AMRAVATI
APPV'D	V.T.		12-08-2025	TYPE 2
if any queries contact - design@nihva.com				REVISION -00 / QTY - 1
ALL DIMENSION ARE IN mm		A3		SCALE - / SHEET 3 OF 19

ITEM NO.	PART NUMBER	DESCRIPTION	QTY.
1	SINGLE POST PLATE	130X75X10	8

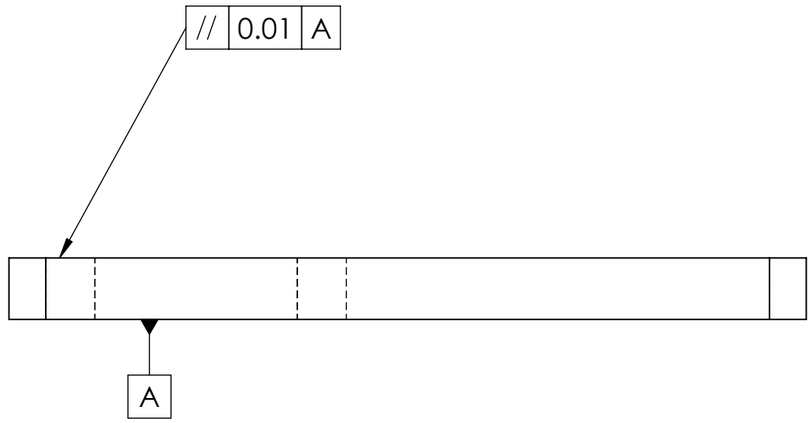

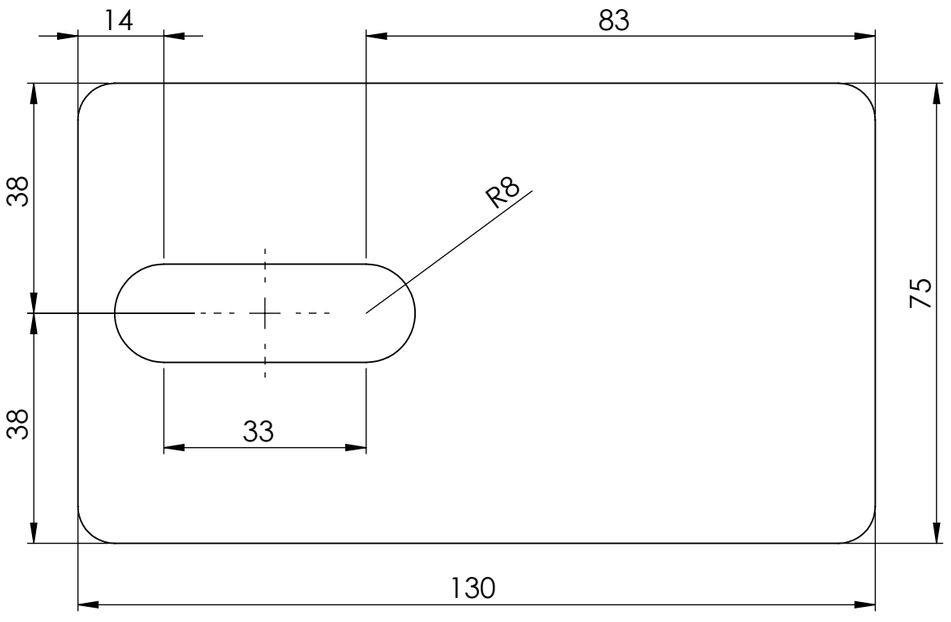


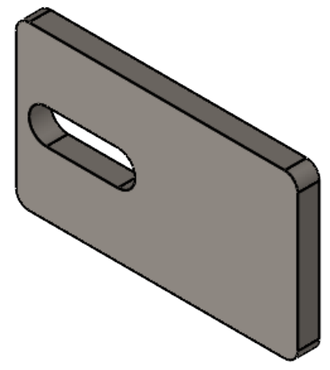


SINGLE POST PLATE
130X75X10 MM THK
QTY-8 NOS

TITLE -GATE AUTOMATION				NIHVA TECHNOLOGIES PVT.LTD.PUNE
DWG NO - NTPL-290-PM-002-02-01				Website - www.nihva.com
	NAME	SIGNATURE	DATE	PROJECT NO - NTPL-290-PM
DRAWN	V.B.		12-08-2025	PRODUCT - BY PARTING SLIDING GATE
CHK'D	B.S.		12-08-2025	SITE LOCATION - AMRAVATI
APPV'D	V.T.		12-08-2025	TYPE 2
if any queries contact - design@nihva.com				REVISION -00 / QTY - 1
ALL DIMENSION ARE IN mm		A3		SCALE - / SHEET 4 OF 19

ITEM NO.	PART NUMBER	DESCRIPTION	QTY.
1	VERTICAL SUPPORT TUBE	75X75X3	16

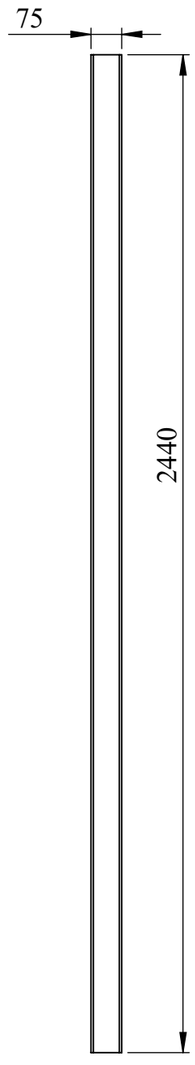


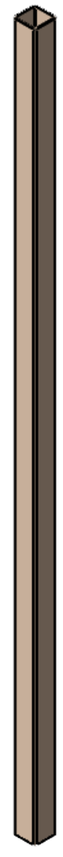



VERTICAL SUPPORT TUBE
75X75X3 MM THK
QTY-16 NOS
THIS VERTICAL SUPPORT TUBE SAME AS USE DOUBLE POST

TITLE -GATE AUTOMATION				NIHVA TECHNOLOGIES PVT.LTD.PUNE	
DWG NO - NTPL-290-PM-002-02-02				Website - www.nihva.com	
	NAME	SIGNATURE	DATE	PROJECT NO - NTPL-290-PM	
DRAWN	V.B.		12-08-2025	PRODUCT - BY PARTING SLIDING GATE	
CHK'D	B.S.		12-08-2025	SITE LOCATION - AMRAVATI	
APPV'D	V.T.		12-08-2025	TYPE 2	
if any queries contact - design@nihva.com				REVISION -00	QTY - 1
ALL DIMENSION ARE IN mm		A3		SCALE -	SHEET 5 OF 19

ITEM NO.	PART NUMBER	DESCRIPTION	QTY.
1	BOTTOM PLATE	215X150X10	16

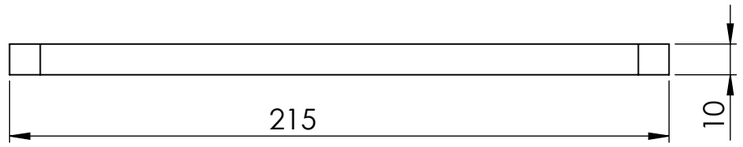

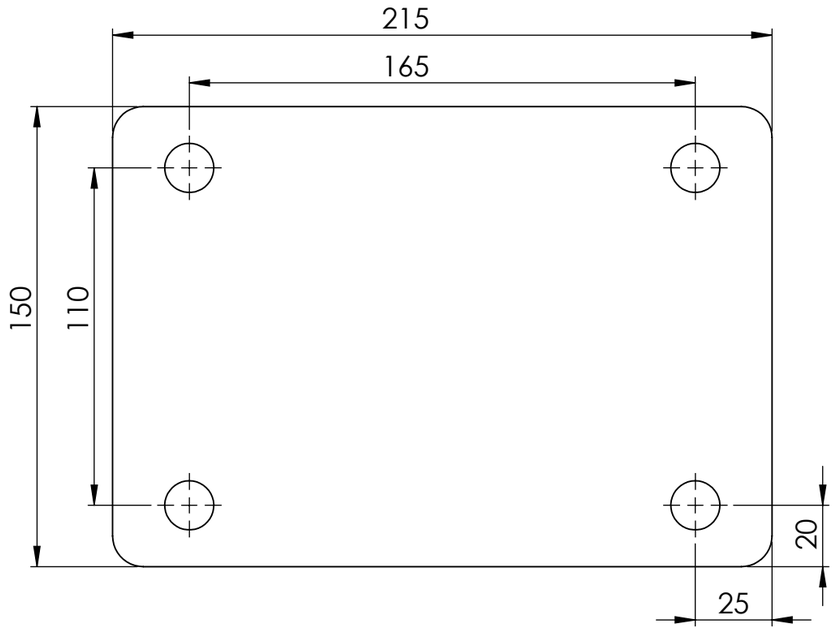


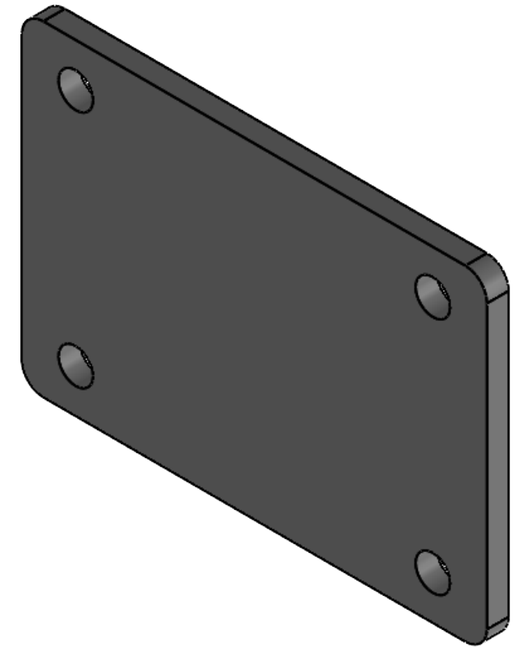


BOTTOM PLATE FOR POST
215X150X10 MM THK
QTY-16 NOS
THIS BOTTOM PLATE SAME AS USE DOUBLE POST

TITLE -GATE AUTOMATION				NIHVA TECHNOLOGIES PVT.LTD.PUNE
DWG NO - NTPL-290-PM-002-02-03				Website - www.nihva.com
	NAME	SIGNATURE	DATE	PROJECT NO - NTPL-290-PM
DRAWN	V.B.		12-08-2025	PRODUCT - BY PARTING SLIDING GATE
CHK'D	B.S.		12-08-2025	SITE LOCATION - AMRAVATI
APPV'D	V.T.		12-08-2025	TYPE 2
if any queries contact - design@nihva.com				REVISION -00 / QTY - 1
ALL DIMENSION ARE IN mm		A3		SCALE - / SHEET 6 OF 19

ITEM NO.	PART NUMBER	DESCRIPTION	QTY.
1	BOTTOM PLATE	215X150X10	16
2	DOUBLE POST PLATE	350X130X10	4
3	VERTICAL TUBE	75X75X3	16

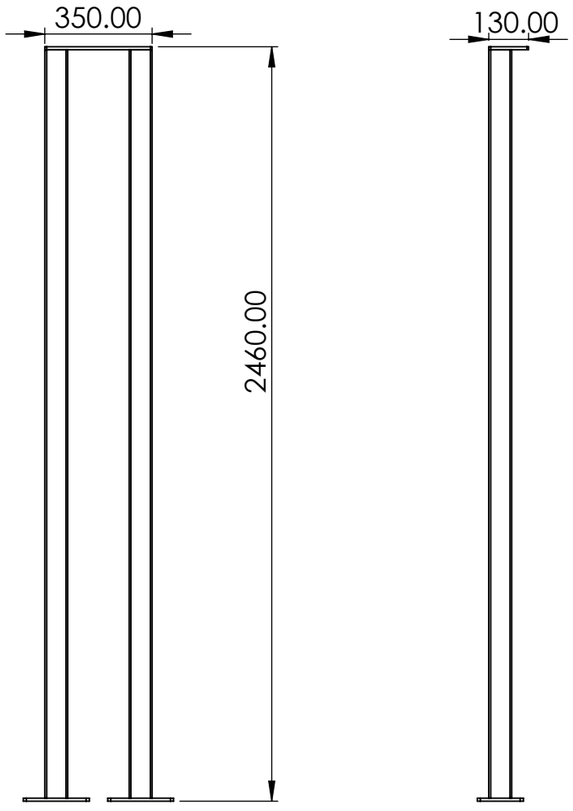


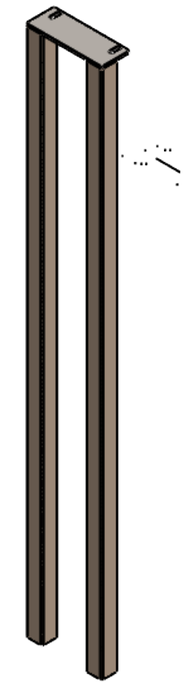


DOUBLE POST ASM
QTY- 4 NOS

TITLE -GATE AUTOMATION				NIHVA TECHNOLOGIES PVT.LTD.PUNE Website - www.nihva.com
DWG NO - NTPL-290-PM-002-03				
	NAME	SIGNATURE	DATE	PROJECT NO - NTPL-290-PM
DRAWN	V.B.		12-08-2025	PRODUCT - BY PARTING SLIDING GATE
CHK'D	B.S.		12-08-2025	SITE LOCATION - AMRAVATI
APPV'D	V.T.		12-08-2025	TYPE 2
if any queries contact - design@nihva.com				REVISION -00 / QTY - 1
ALL DIMENSION ARE IN mm		A3		SCALE - / SHEET 7 OF 19

ITEM NO.	PART NUMBER	DESCRIPTION	QTY.
1	DOUBLE POST PLATE	350X130X10	4

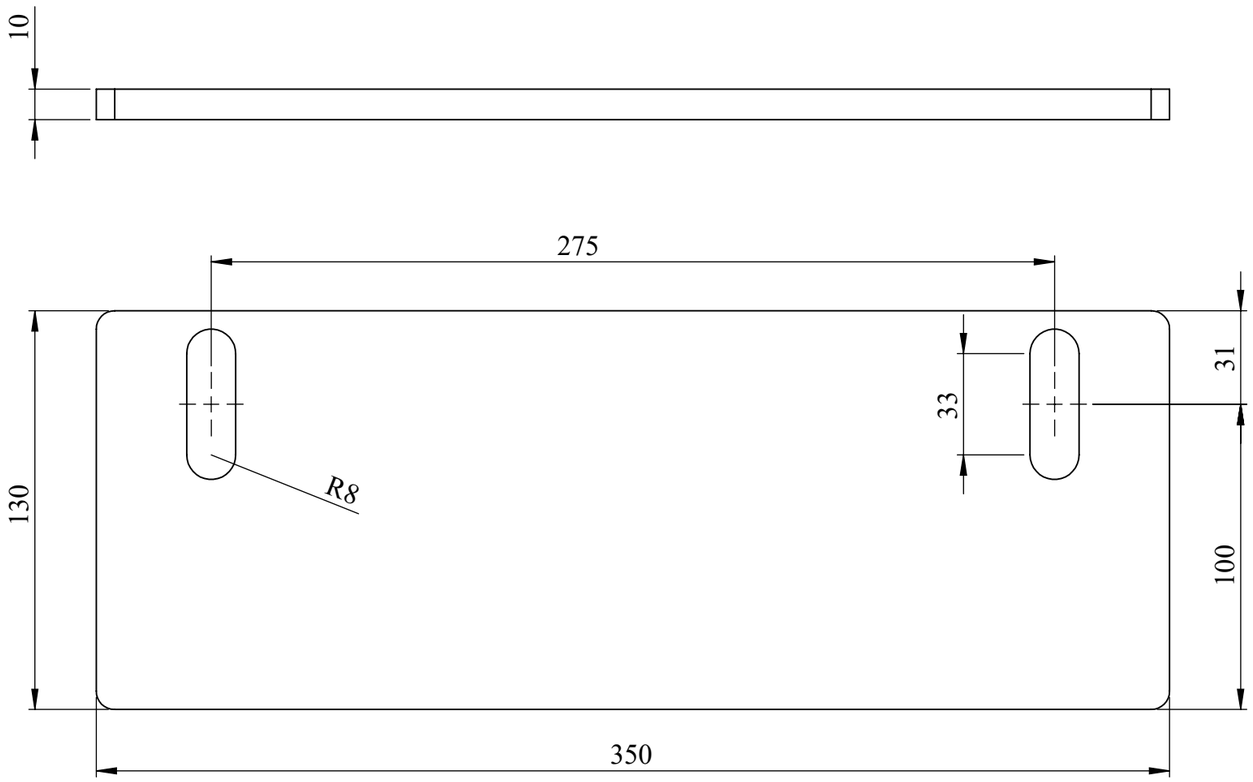


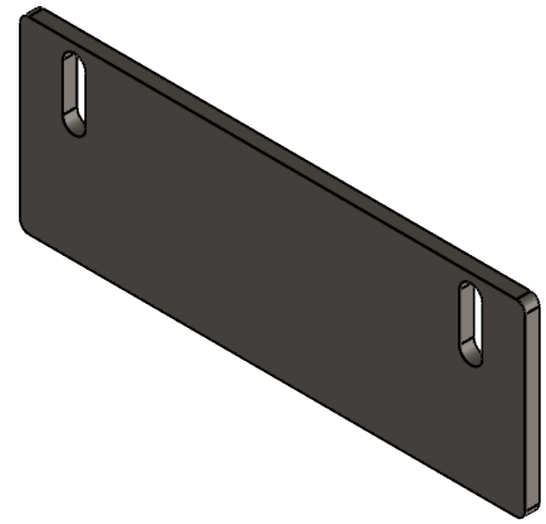



DOUBLE POST PLATE
350X130X10 MM THK
QTY-4 NOS

TITLE -GATE AUTOMATION				NIHVA TECHNOLOGIES PVT.LTD.PUNE
DWG NO - NTPL-290-PM-002-03-01				Website - www.nihva.com
	NAME	SIGNATURE	DATE	PROJECT NO - NTPL-290-PM
DRAWN	V.B.		12-08-2025	PRODUCT - BY PARTING SLIDING GATE
CHK'D	B.S.		12-08-2025	SITE LOCATION - AMRAVATI
APPV'D	V.T.		12-08-2025	TYPE 2
if any queries contact - design@nihva.com				REVISION -00 / QTY - 1
ALL DIMENSION ARE IN mm		A3		SCALE - / SHEET 8 OF 19

ITEM NO.	PART NUMBER	DESCRIPTION	QTY.
1	**GUIDE PLATE**	ID-14 (H)-79 (W)-10	**8**
2	**SUPPORT PLATE**	**90x74x10**	**4**
3	**WHEEL**	100x50	**4**

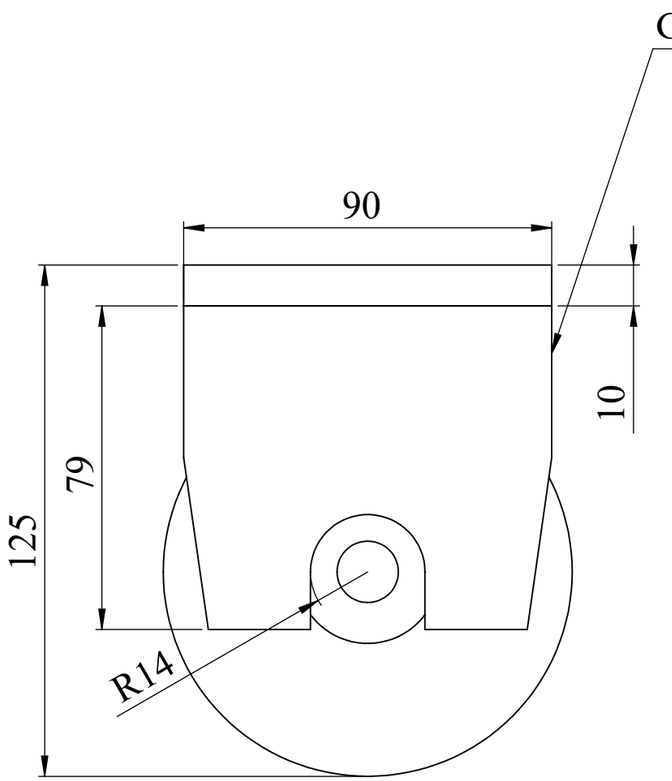

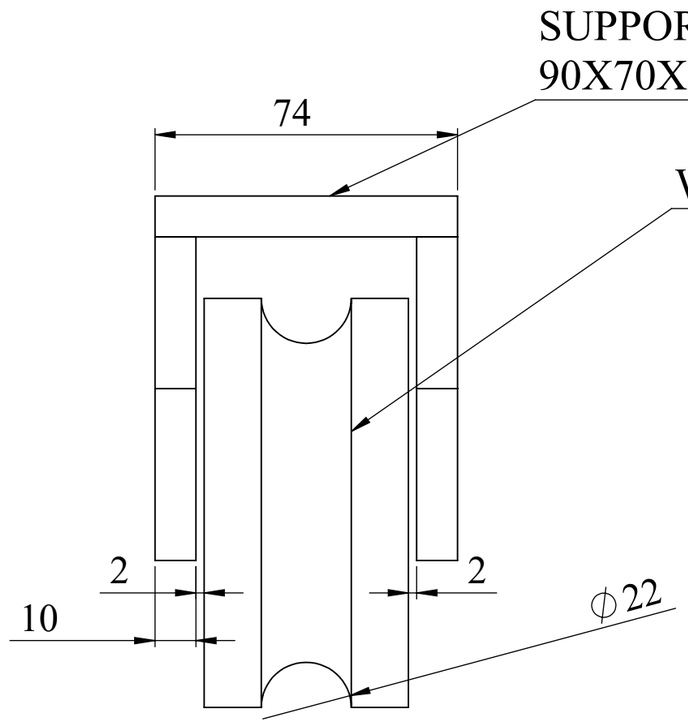


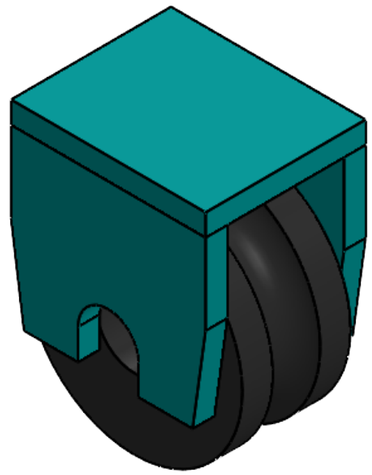


QTY- 4 NOS

TITLE - GATE AUTOMATION				NIHVA TECHNOLOGIES PVT.LTD.PUNE
DWG NO - NTPL-290-PM-002-01-02				Website - www.nihva.com
	NAME	SIGNATURE	DATE	PROJECT NO -NTPL-290-PM
DRAWN	V.B.		12-08-25	PRODUCT - BY PARRTING SLIDING GATE
CHK'D	B.S.		12-08-25	SITE LOCATION - AMRAVATI
APPV'D	V.T.		12-08-25	TYPE 2
if any queries contact - design@nihva.com				REVISION -00 / QTY - 1
ALL DIMENSION ARE IN mm		A3		SCALE - / SHEET 9 OF 19

ITEM NO.	PART NUMBER	DESCRIPTION	QTY.
1	SUPPORT PLATE	90x74x10	**4**

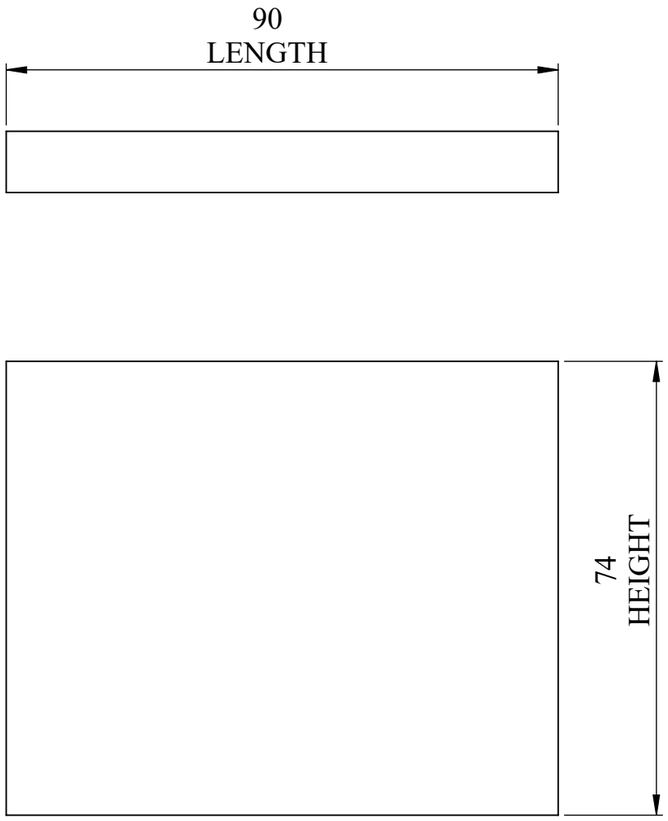


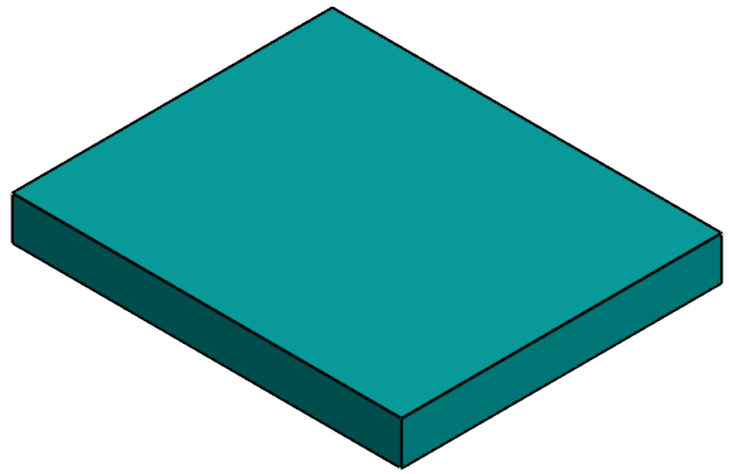



SUPPORT PLATE
QTY- 4 NOS

TITLE - GATE AUTOMATION				NIHVA TECHNOLOGIES PVT.LTD.PUNE
DWG NO - NTPL-290-PM-002-01-02-01				Website - www.nihva.com
	NAME	SIGNATURE	DATE	PROJECT NO - NTPL-290-PM
DRAWN	V.B.		12-08-2025	PRODUCT - BY PARTING SLIDING GATE
CHK'D	B.S.		12-08-2025	SITE LOCATION -AMRAVATI
APPV'D	V.T.		12-08-2025	TYPE 2
if any queries contact - design@nihva.com				REVISION -00 / QTY - 1
ALL DIMENSION ARE IN mm		A3		SCALE - / SHEET 10 OF 19

ITEM NO.	PART NUMBER	DESCRIPTION	QTY.
1	**GUIDE PLATE**	ID-14 (H)-79 (W)-10	**8**

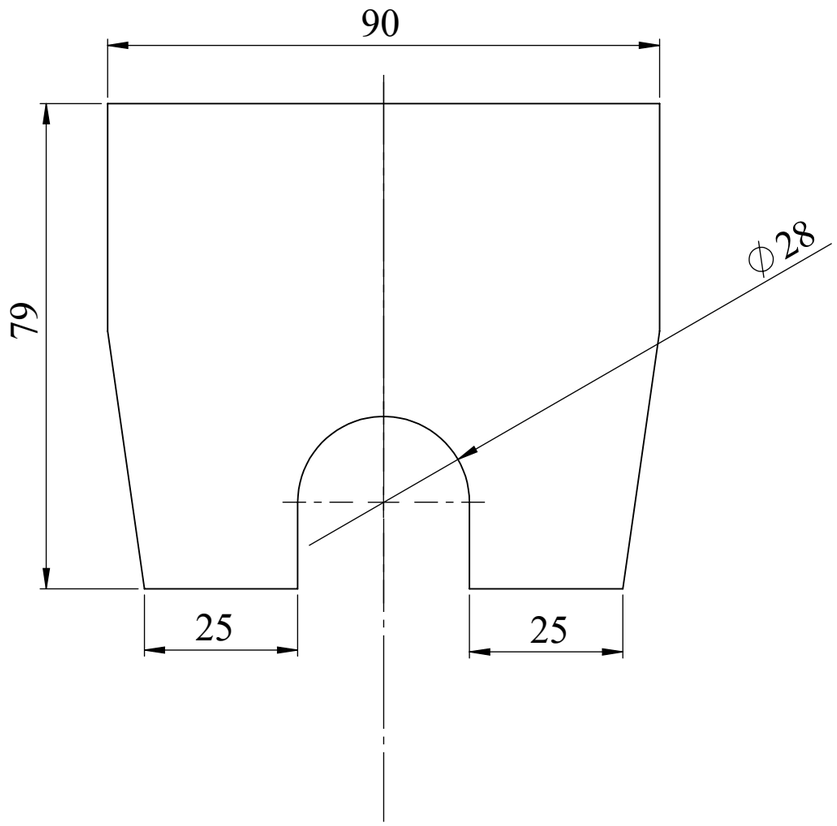

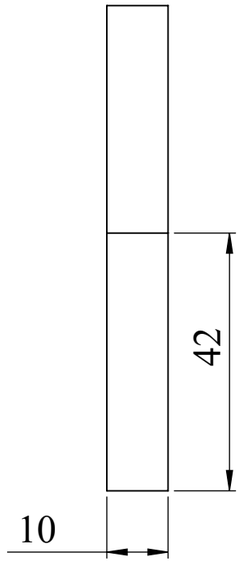


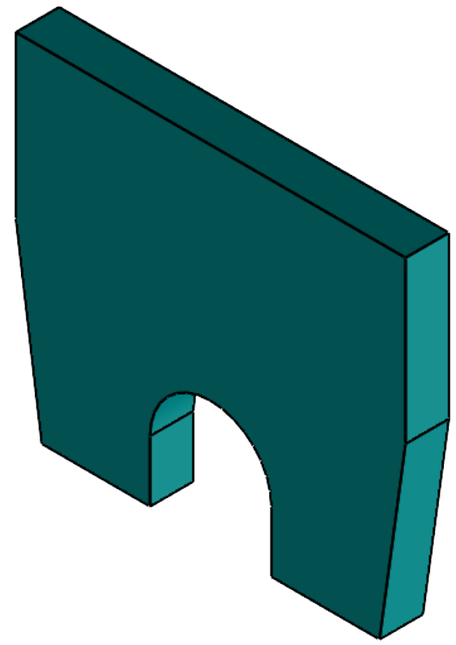


GUIDE PLATE
QTY- 8 NOS

TITLE - GATE AUTOMATION				NIHVA Technologies Pvt. Ltd.	NIHVA TECHNOLOGIES PVT.LTD.PUNE Website - www.nihva.com
DWG NO - NTPL-290-PM-002-01-02-02					
	NAME	SIGNATURE	DATE	PROJECT NO - NTPL-290-PM	
DRAWN	V.B.		12-08-2025	PRODUCT - BY PARTING SLIDING GATE	
CHK'D	B.S.		12-08-2025	SITE LOCATION -AMRAVATI	
APPV'D	V.T.		12-08-2025	TYPE 2	
if any queries contact - design@nihva.com				REVISION -00	QTY - 1
ALL DIMENSION ARE IN mm		A3		SCALE -	SHEET 11 OF 19

ITEM NO.	PART NUMBER	DESCRIPTION	QTY.
1	**WHEEL**	100x50	**4**

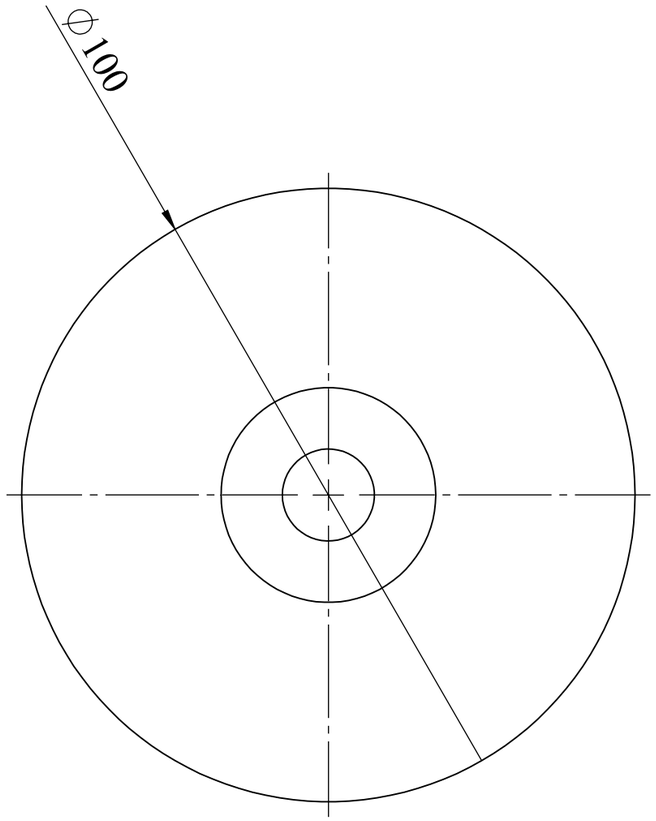

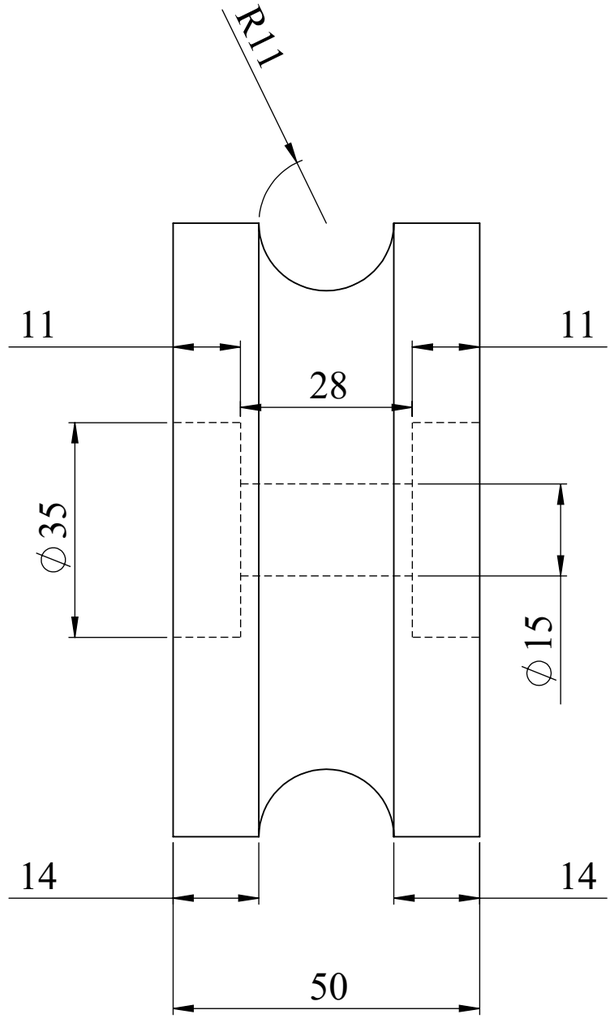






WHEEL
QTY- 4 NOS

TITLE - GATE AUTOMATION				NIHVA TECHNOLOGIES PVT.LTD.PUNE
DWG NO - NTPL-290-PM-002-01-02-03				Website - www.nihva.com
	NAME	SIGNATURE	DATE	PROJECT NO - NTPL -290-PM
DRAWN	V.B.		12-08-2025	PRODUCT -BY PARTING SLIDING GATE
CHK'D	B.S.		12-08-2025	SITE LOCATION -AMRAVATI
APPV'D	V.T.		12-08-2025	TYPE 2
if any queries contact - design@nihva.com				REVISION -00 / QTY - 1
ALL DIMENSION ARE IN mm		A3		SCALE - / SHEET 12 OF 19

ITEM NO.	PART NUMBER	L 40X 40 X 4	QTY.
1	L ANGLE (40X40X4)	(L)- 600	14
		L 40.00 X 40.00 X 4.000	1

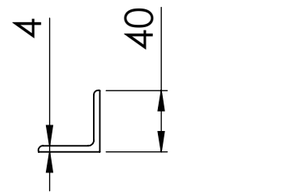

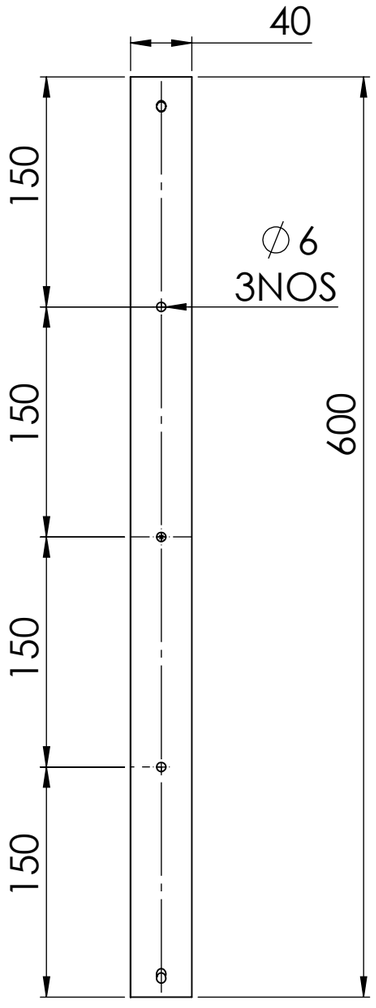


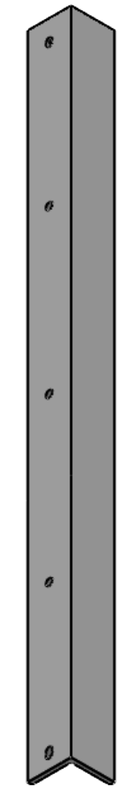



L ANGLE FOR BARBED WIRE
40X40X4 THK

TITLE - GATE AUTOMATION				NIHVA TECHNOLOGIES PVT.LTD.PUNE
DWG NO - NTPL-290-PM-002-01-03				Website - www.nihva.com
	NAME	SIGNATURE	DATE	PROJECT NO - NTPL-290-PM
DRAWN	V.B.		12-08-2025	PRODUCT -BY PARTING SLIDING GATE
CHK'D	P.M.		12-08-2025	SITE LOCATION - AMRAVATI
APPV'D	V.T.		12-08-2025	TYPE 2
if any queries contact - design@nihva.com				REVISION -00 / QTY - 1
ALL DIMENSION ARE IN mm		A3		SCALE - / SHEET 13 OF 19

ITEM NO.	PART NUMBER	DESCRIPTION	QTY.
1	EN8 BAR	OD- 20 MM	1
	ISMB BEAM	SIZE- 100 X 50 19200 MM (L)	1

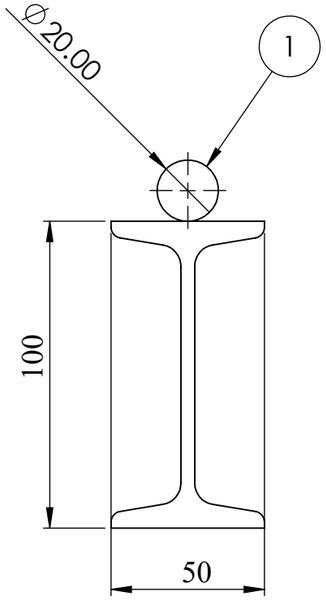

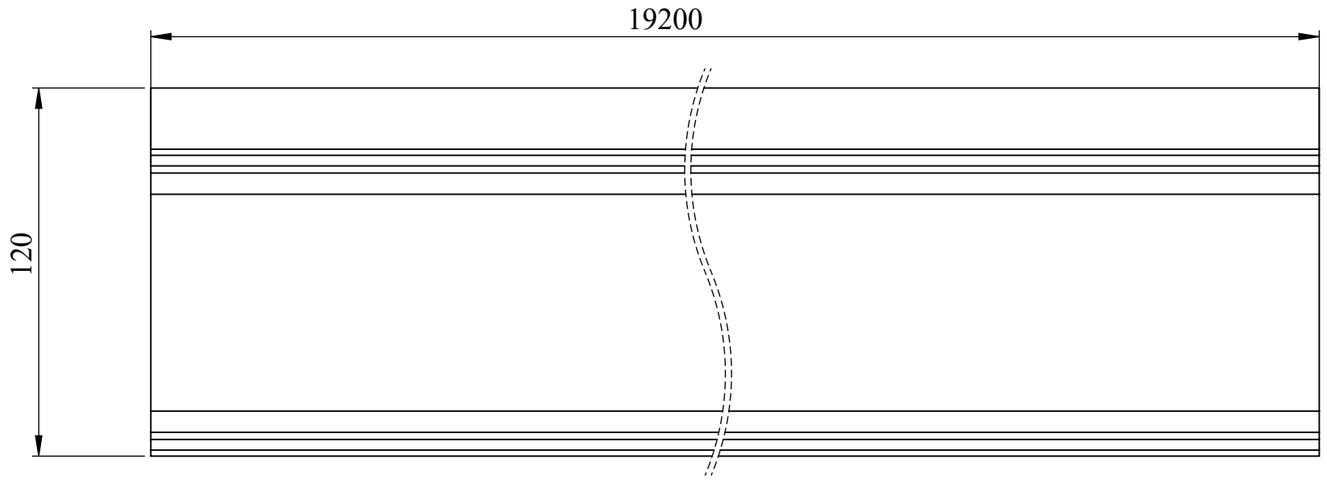


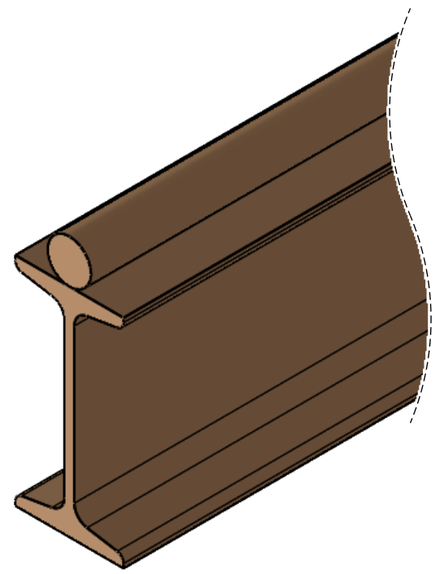


GATE TRACK
QTY-1NOS

TITLE - GATE AUTOMATION				NIHVA TECHNOLOGIES PVT.LTD.PUNE
DWG NO - NTPL-290-PM-002-04				Website - www.nihva.com
	NAME	SIGNATURE	DATE	PROJECT NO - NTPL-290-PM
DRAWN	V.B.		12-08-2025	PRODUCT - BY PARTING SLIDING GATE
CHK'D	B.S.		12-08-2025	SITE LOCATION - AMRAVATI
APPV'D	V.T.		12-08-2025	TYPE-2
if any queries contact - design@nihva.com				REVISION -00 / QTY - 1
ALL DIMENSION ARE IN mm		A3		SCALE - / SHEET 14 OF 19

ITEM NO.	PART NUMBER	DESCRIPTION	QTY.
1	M14 ANCHOR	M14X150	65

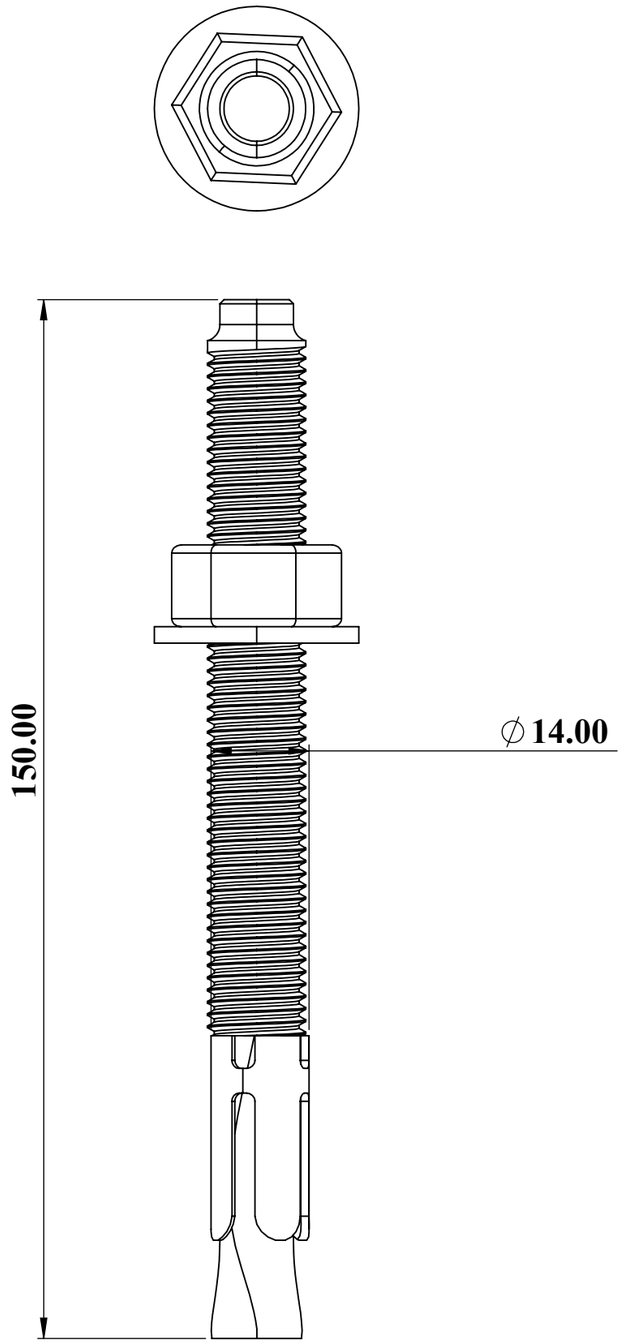


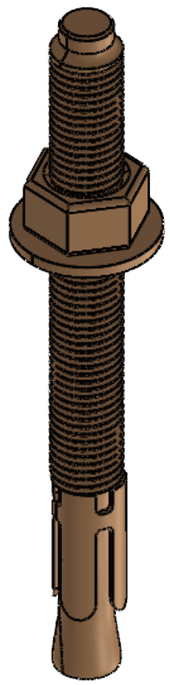



NOTE -
M14 X 150 MM ANCHOR BOLT
QTY- 65 NOS

TITLE -GATE AUTOMATION				NIHVA TECHNOLOGIES PVT.LTD.PUNE Website - www.nihva.com
DWG NO - NTPL-290-PM-002-05				
	NAME	SIGNATURE	DATE	PROJECT NO - NTPL-290-PM
DRAWN	V.B.		12-08-2025	PRODUCT -BYPARTING SLIDING GATE
CHK'D	B.S.		12-08-2025	SITE LOCATION - AMRAVATI
APPV'D	V.T.		12-08-2025	TYPE 2
if any queries contact - design@nihva.com				REVISION -00 / QTY - 1
ALL DIMENSION ARE IN mm		A3		SCALE - / SHEET 15 OF 19

ITEM NO.	PART NUMBER	DESCRIPTION	QTY.
1	NYLON STOPPER		2
2	NYLON STOPPER PLATE	135X135X10	2

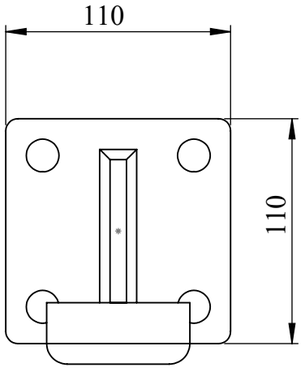

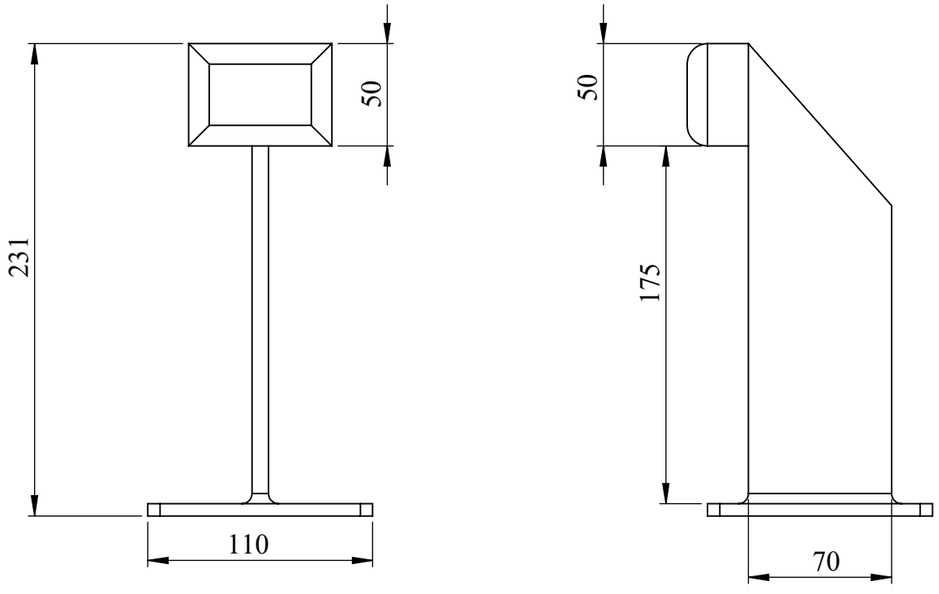


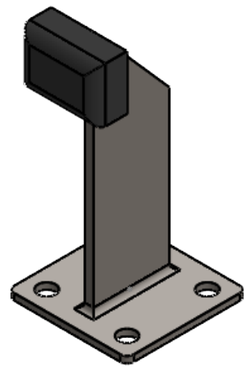



NOTE -
NYLON STOPPER
QTY- 2 NOS

TITLE -GATE AUTOMATION				NIHVA TECHNOLOGIES PVT.LTD.PUNE
DWG NO - NTPL-290-PM-002-06				Website - www.nihva.com
	NAME	SIGNATURE	DATE	PROJECT NO - NTPL-290-PM
DRAWN	V.B.		12-08-2025	PRODUCT - BY PARTING SLIDING GATE
CHK'D	B.S.		12-08-2025	SITE LOCATION - AMRAVATI
APPV'D	V.T.		12-08-2025	TYPE 2
if any queries contact - design@nihva.com				REVISION -00 / QTY - 1
ALL DIMENSION ARE IN mm		A3		SCALE - / SHEET 16 OF 19


ITEM NO.	PART NUMBER	DESCRIPTION	QTY.
2	NYLON STOPPER PLATE	135X135X10	2

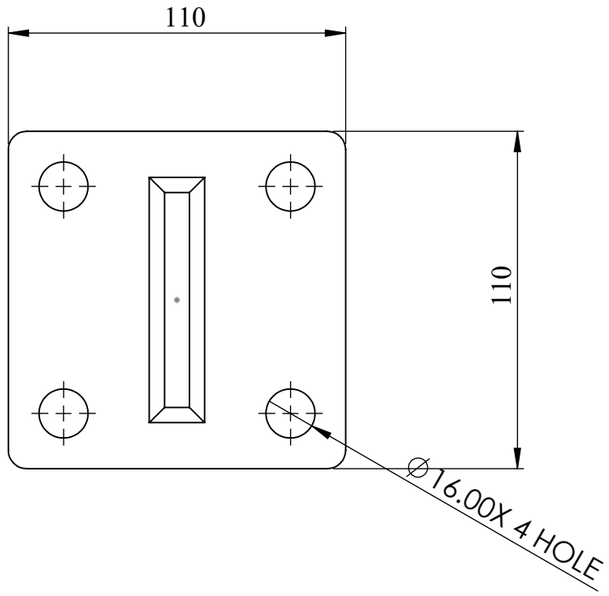

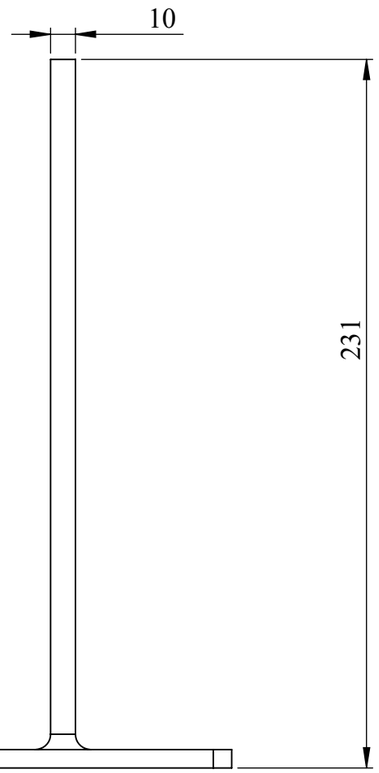

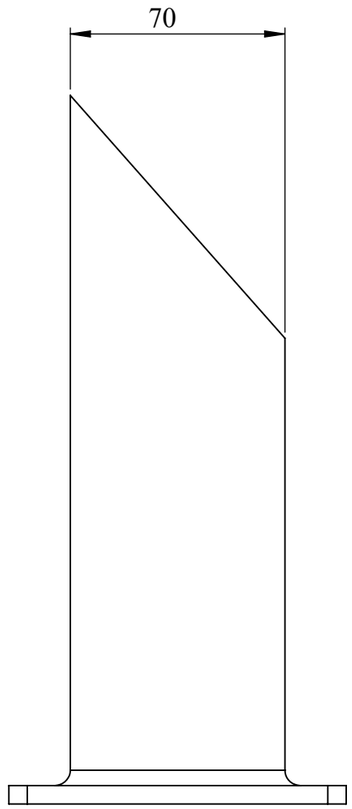



NOTE -
NYLON STOPPER
QTY- 2 NOS

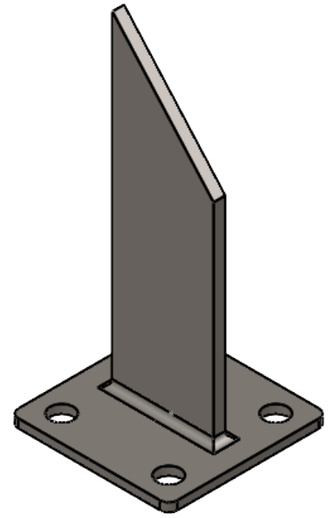


TITLE -GATE AUTOMATION				NIHVA TECHNOLOGIES PVT.LTD.PUNE
DWG NO - NTPL-290-PM-002-06-01				Website - www.nihva.com
	NAME	SIGNATURE	DATE	PROJECT NO - NTPL-290-PM
DRAWN	V.B.		12-08-2025	PRODUCT - BY PARTING SLIDING GATE
CHK'D	B.S.		12-08-2025	SITE LOCATION - AMRAVATI
APPV'D	V.T.		12-08-2025	TYPE 2
if any queries contact - design@nihva.com				REVISION -00 / QTY - 1
ALL DIMENSION ARE IN mm		A3		SCALE - / SHEET 17 OF 19

ITEM NO.	PART NUMBER	DESCRIPTION	QTY.
1	NYLON STOPPER		2

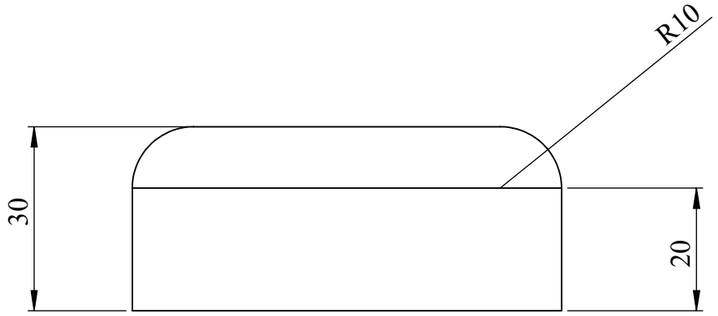

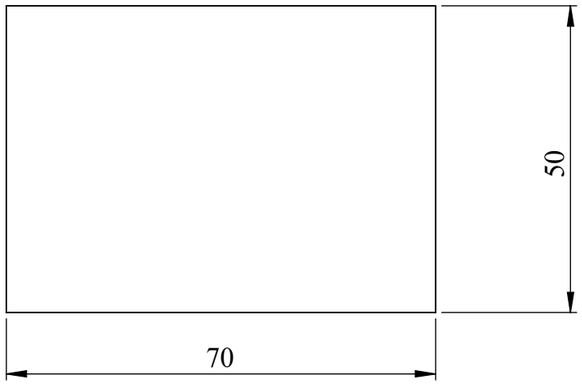


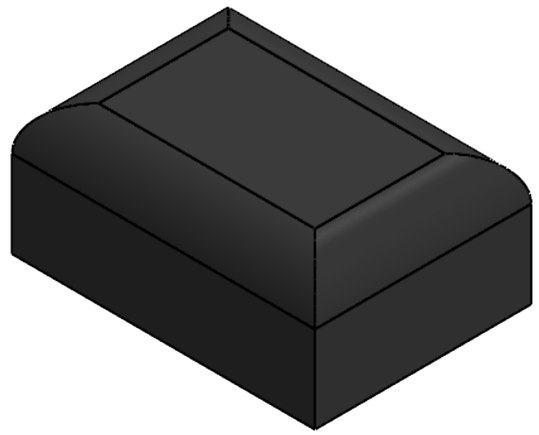


NOTE -
NYLON STOPPER
QTY- 2 NOS

TITLE -GATE AUTOMATION				NIHVA TECHNOLOGIES PVT.LTD.PUNE
DWG NO - NTPL-290-PM-002-07				Website - www.nihva.com
	NAME	SIGNATURE	DATE	PROJECT NO - NTPL-290-PM
DRAWN	V.B.		12-08-2025	PRODUCT - BY PARTING SLIDING GATE
CHK'D	B.S.		12-08-2025	SITE LOCATION - AMRAVATI
APPV'D	V.T.		12-08-2025	TYPE 2
if any queries contact - design@nihva.com				REVISION -00 / QTY - 1
ALL DIMENSION ARE IN mm		A3		SCALE - / SHEET 18 OF 19

ITEM NO.	PART NUMBER	DESCRIPTION	QTY.
1	TOWER BOLT HOLLOW PIPE	DIA- 18MM (3 MM THK)	2
2	Tower Bolt	DIA- 15MM 300(L)	2

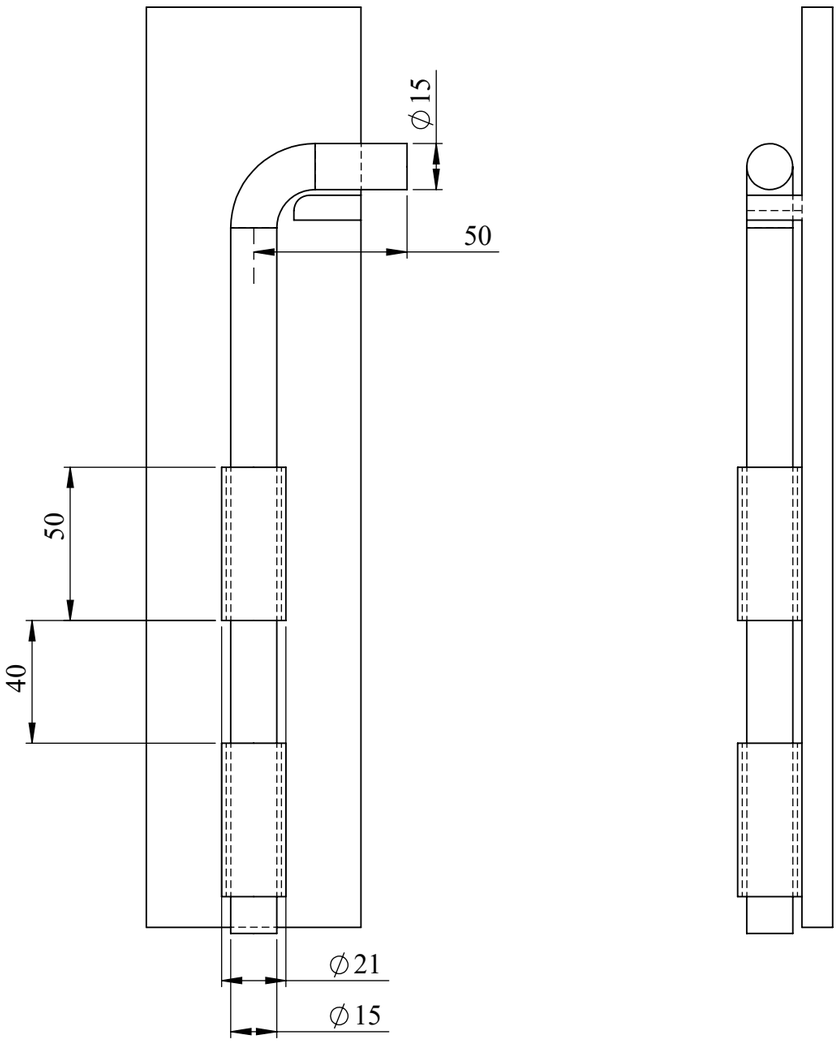

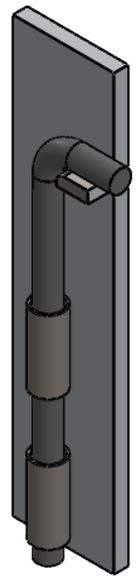

NOTE -
TOWER BOLT
QTY- 2 NOS

TITLE -GATE AUTOMATION				NIHVA TECHNOLOGIES PVT.LTD.PUNE
DWG NO - NTPL-290-PM-002-08				Website - www.nihva.com
	NAME	SIGNATURE	DATE	PROJECT NO - NTPL-290-PM
DRAWN	V.B.		12-08-2025	PRODUCT - BY PARTING SLIDING GATE
CHK'D	B.S.		12-08-2025	SITE LOCATION - AMRAVATI
APPV'D	V.T.		12-08-2025	TYPE 2
if any queries contact - design@nihva.com				REVISION -00 / QTY - 1
ALL DIMENSION ARE IN mm		A3		SCALE - / SHEET 19 OF 19