

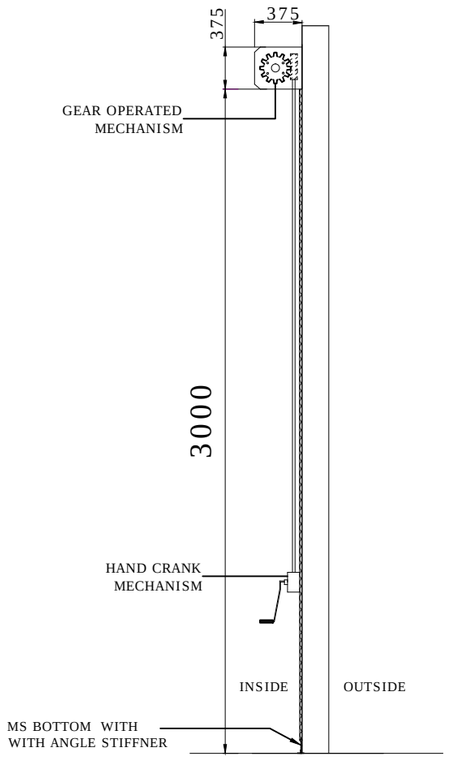


SIDE VIEW

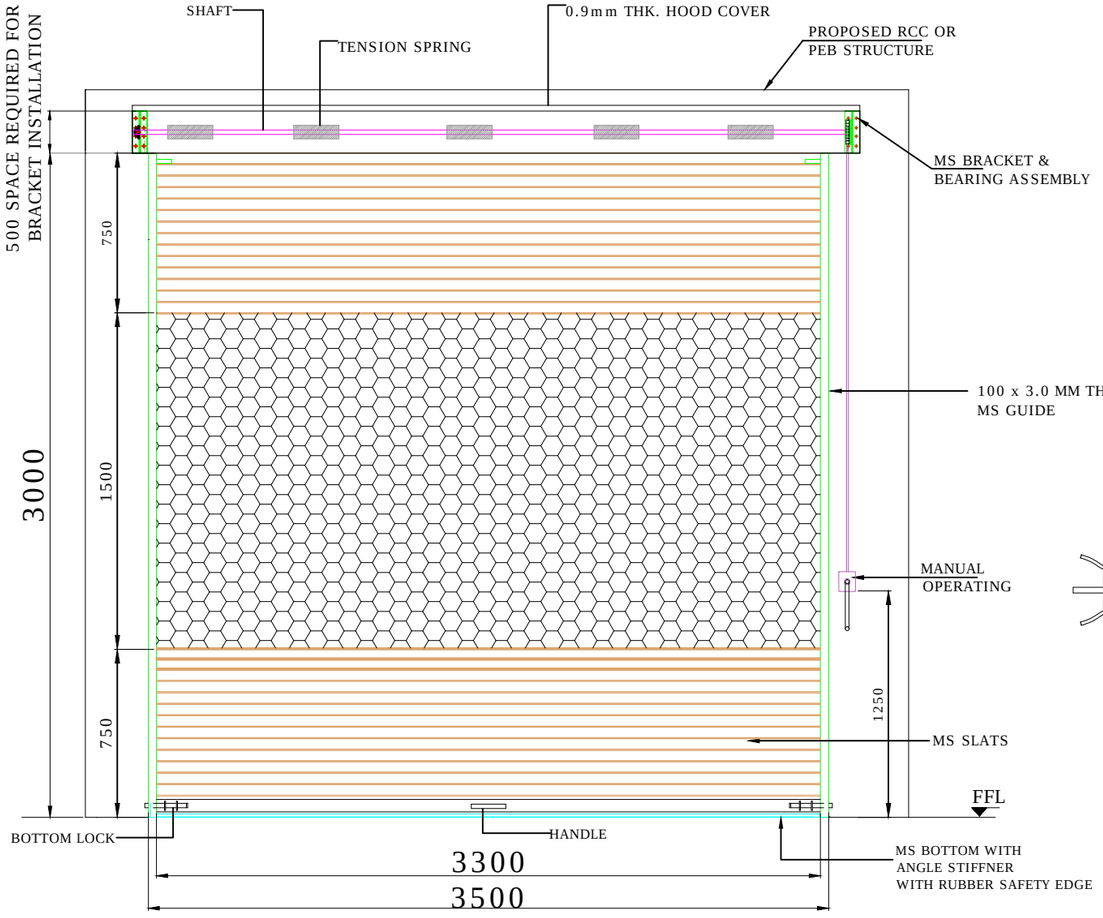


INSIDE ELEVATION

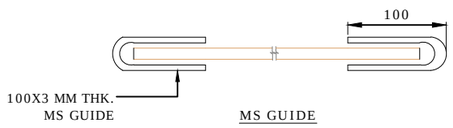


MS GUIDE




PLAN

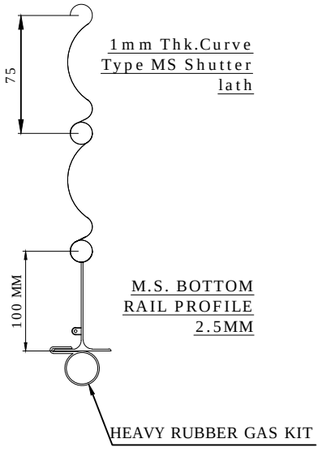

M.S. BOTTOM RAIL PROFILE 2.5MM

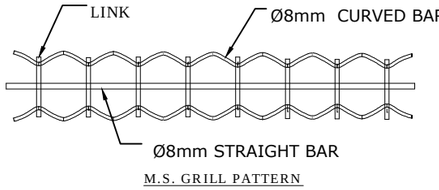

M.S. GRILL PATTERN

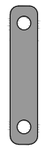

LINK

CLEAR WIDTH (CW)	CLEAR HEIGHT (CH)	GUIDE SIZE	GRILL SIZE	QUANTITY
3300	3000	100X3mm	1500X3300mm	01 NOS

DIMENSION :

CLEAR WIDTH	CLEAR HEIGHT	QUANTITY
3300mm	3000mm	01 NOS

MATERIAL:

THICKNESS :

NOTE:
1.REQUIRED STRUCTURE FOR ROLLING SHUTTER WILL BE CLIENT'S SCOPE.
2. SHUTTER WILL BE POWDER COATED CLIENT SHOULD CONFIRM RAL COLOR SHADE.

NIHVA TECHNOLOGIES PVT. LTD.
NIHVA TECHNOLOGIES
PVT. LTD. PUNE
Email:- info@nihva.com
Website:- www.nihva.com

TITLE:

GEAR OPERATED ROLLING SHUTTER 3X3m

CLIENT'S APPROVAL :

CLIENT - RAVIRAJ REALTY

PROJECT -

SITE LOCATION - PUNE

DWG. NO. : NIHVA/17-18/0409 | REV.:- 0

SCALE: NTS | WT: | SHEET:1 OF 1

		DATE	SIGN.
DRAWN	SURAJ	30-03-2018	
CHECK	OMKAR	30-03-2018	
APPRD	PRADEEP	30-03-2018	

If any queries contact : design@nihva.com

NOTE: ALL DIMENSIONS ARE IN mm

THIS DRAWING & DESIGN IS THE PROPERTY OF NIHVA TECHNOLOGIES. NOT TO BE SOLD OR COPIED TO ANY OTHER CONCERN.