

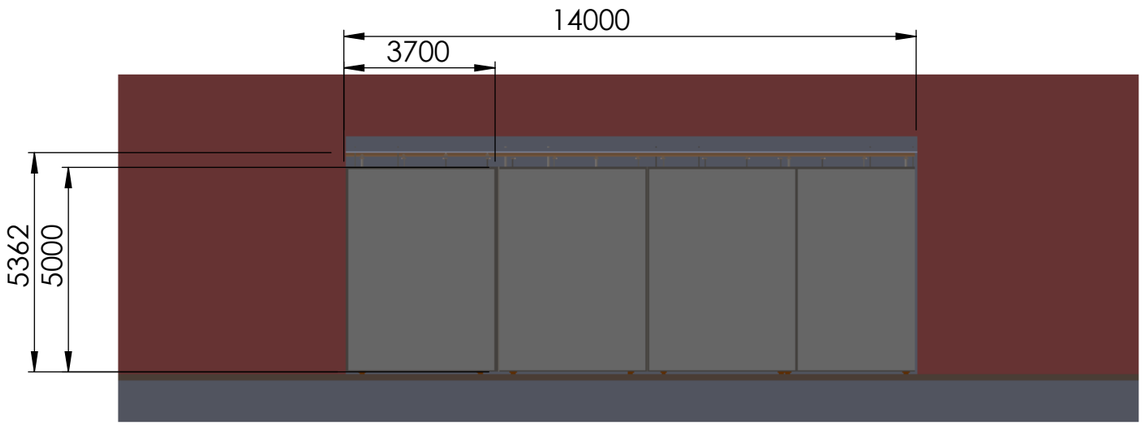



CLOSE POSITION

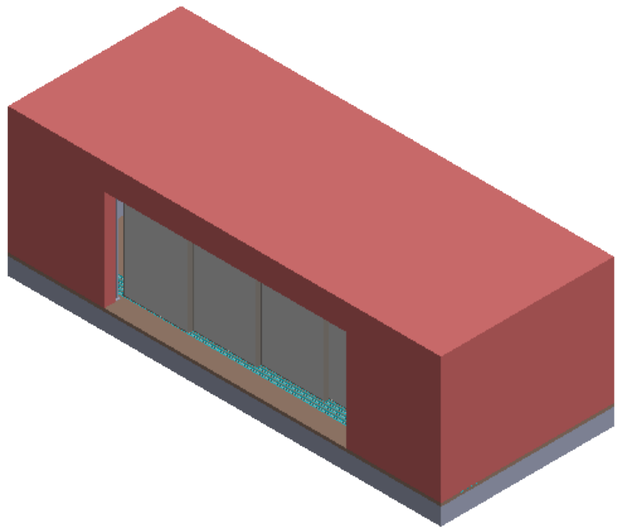


ISOMETRIC

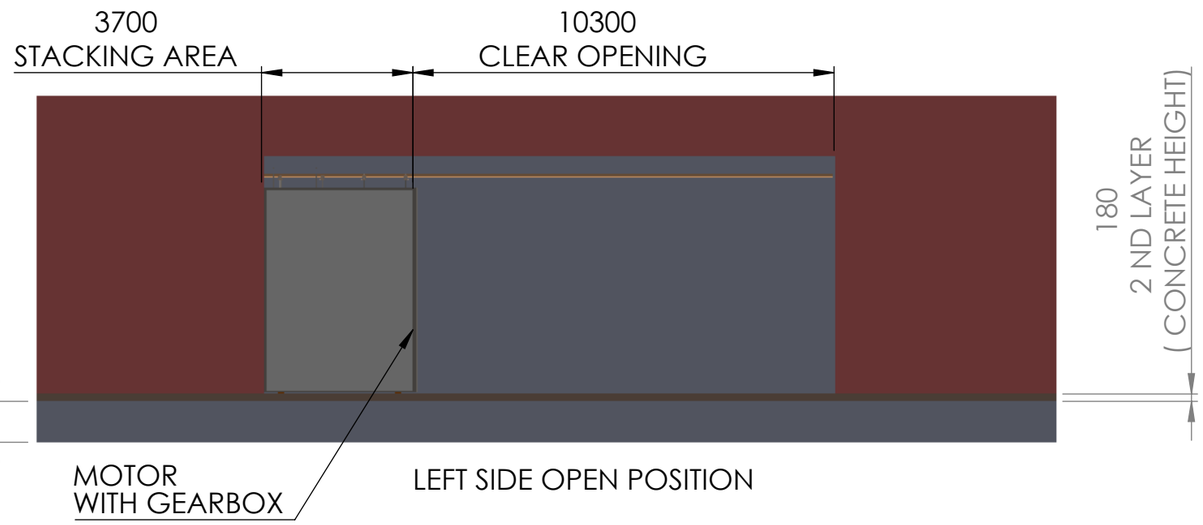

LEFT SIDE OPEN POSITION

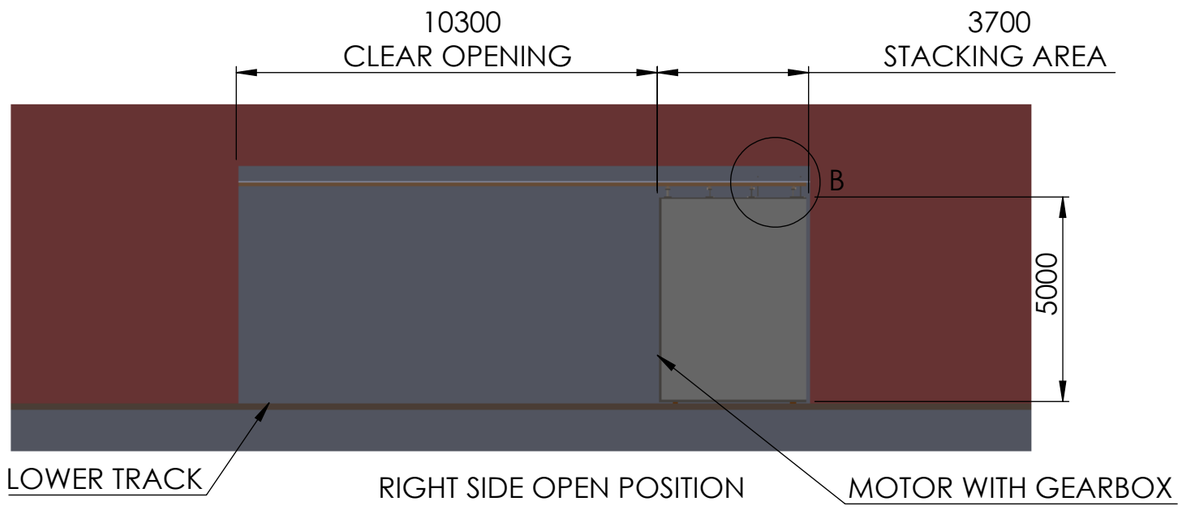

RIGHT SIDE OPEN POSITION

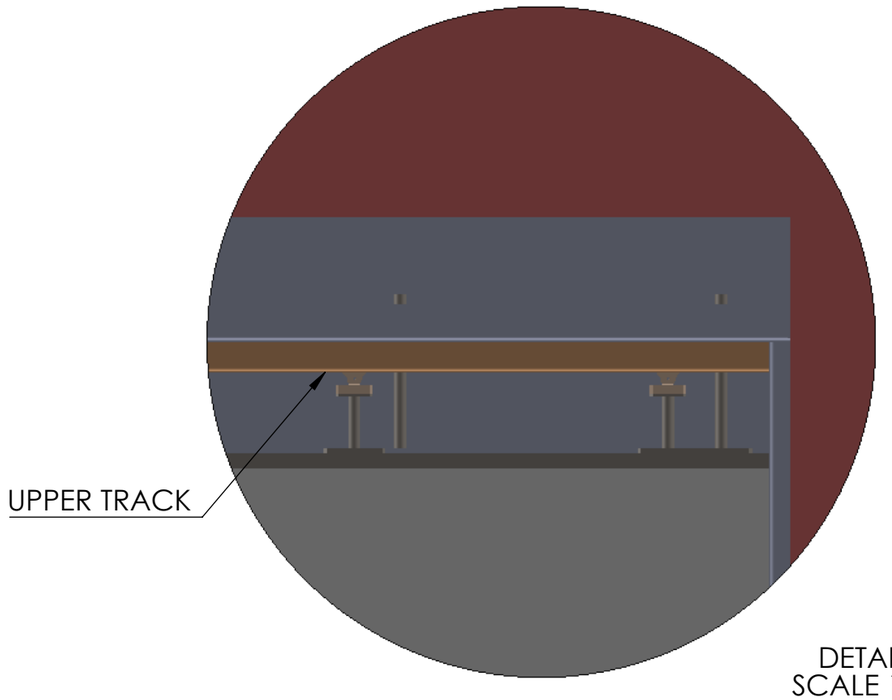

DETAIL B
SCALE 1 : 20

TITLE :	**HANGING SLIDING DOOR**		
	NAME	**SIGN**	**DATE**
DRAWN	BHARATI SABALE		23-12-2024
CHK'D	SURAJ WARALE		23-12-2024
APPV'D	VIJAY T.		23-12-2024
	DIMENSIONS ARE IN MILLIMETERS		

NIHVA Technologies Pvt. Ltd.

NIHVA TECHNOLOGIES PVT LTD

CLIENT NAME : ISRO

PRODUCT NAME : HANGING SLIDING DOOR

SITE LOCATION : ALUVA, KERALA

DWG NO. GA

A3

REVISION : 0

SCALE:

SHEET 1 OF 1