


GA DRAWING

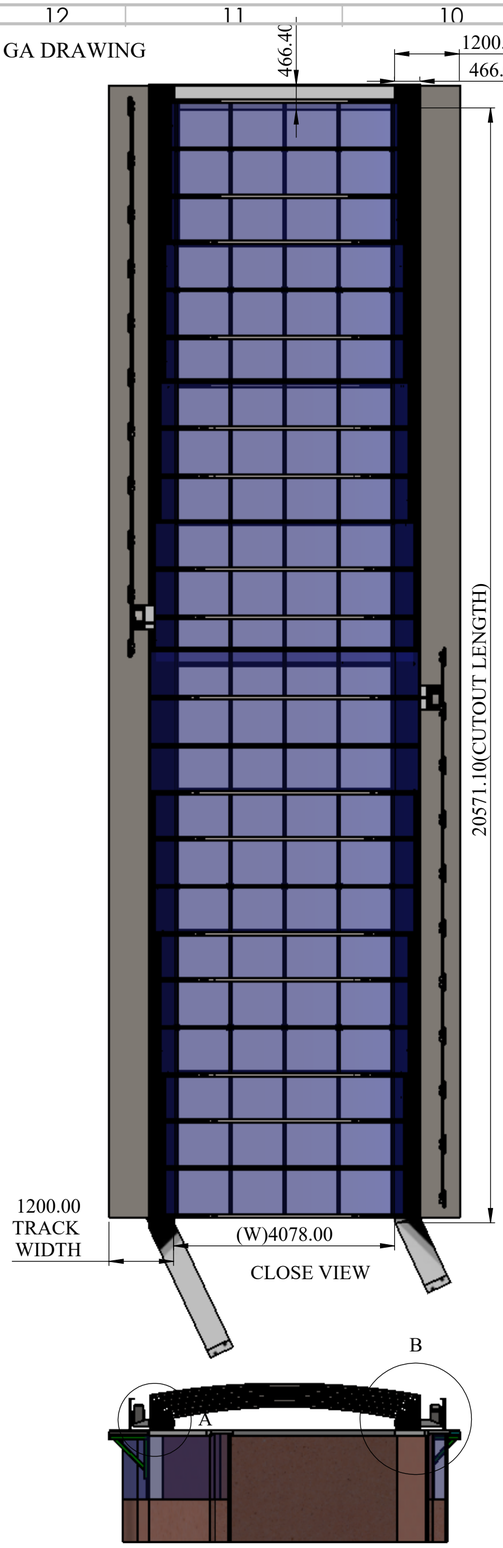


SLIDING
DIRECTION

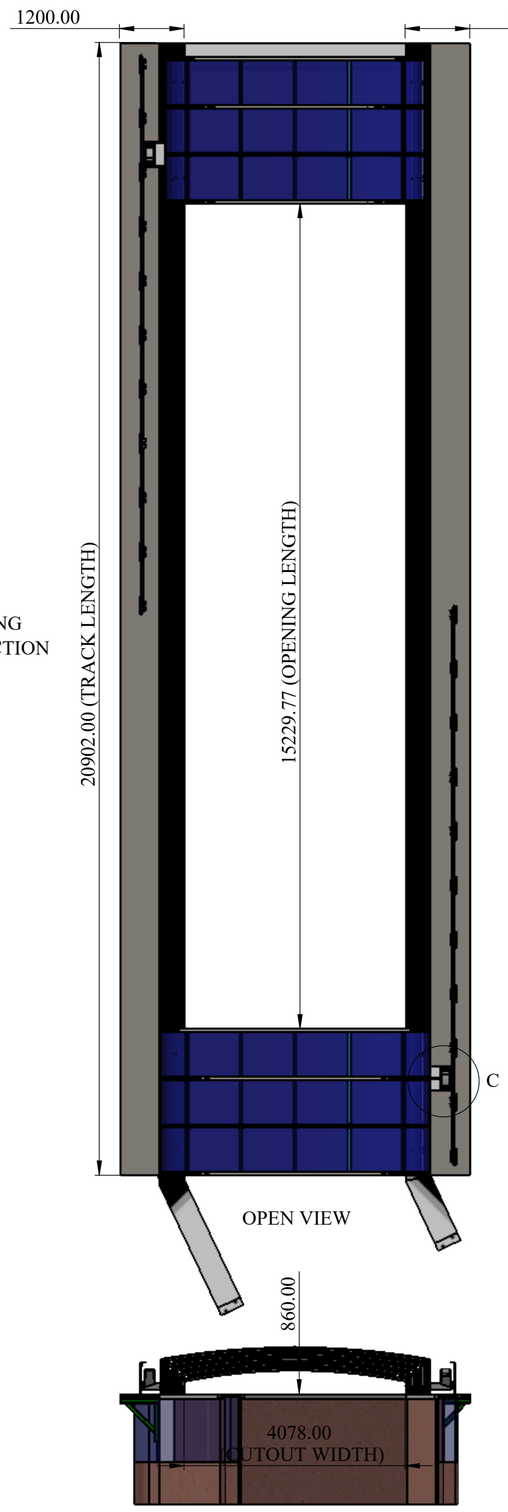

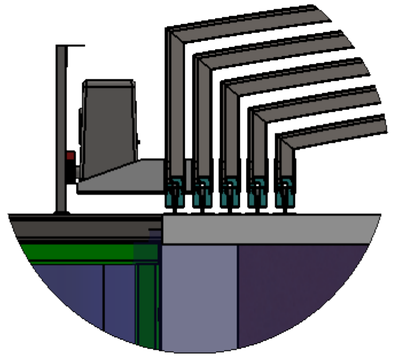


MOTOR+TRACK
ARRANGEMENT

DETAIL A
SCALE 1 : 15

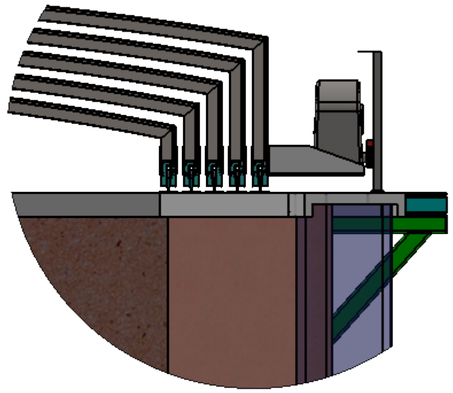

MOTOR+TRACK
ARRANGEMENT

DETAIL B
SCALE 1 : 18

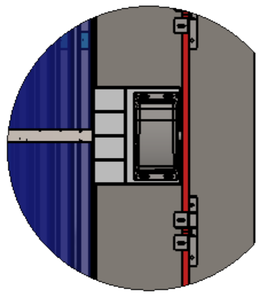

MOTOR
ARRANGEMENT

DETAIL C
SCALE 1 : 20

REV DESCRIPTION	DATE	REV NO
	16-07-2026	REV 00
1.		

NOTE :

GA DRAWING
THIS DRAWING IS FOR CLIENT SCOPE.

SPECIAL INSTRUCTION'S :

This drawing & design is the property of NIHVA TECHONOLOGIES PVT. LTD. Not to be sold or copied to any other concern

TITLE - RETRACTABLE ROOF

DWG NO - NTPL


NIHVA TECHNOLOGIES PVT.LTD.PUNE
Website - www.nihva.com


	NAME	SIGNATURE	DATE
DRAWN	V.W.		16-07-2026
CHK'D	S.P.		19-07-2026
APPV'D	V.T.		19-07-2026

PRODUCT - CENTER OPENING RETRACTABLE ROOF
CLIENT NAME - YASHWANT
SITE LOCATION - CHENNAI
MATRIAL -
QTY - 1
If any queries contact - info@nihva.com
PROJECTION METHOD:
SCALE :
ALL DIMENSION ARE IN mm
A2
SHEET 1 OF 2

CIVIL DRAWING

REV DESCRIPTION	DATE	REV NO
	16-07-2026	REV 00
1.		

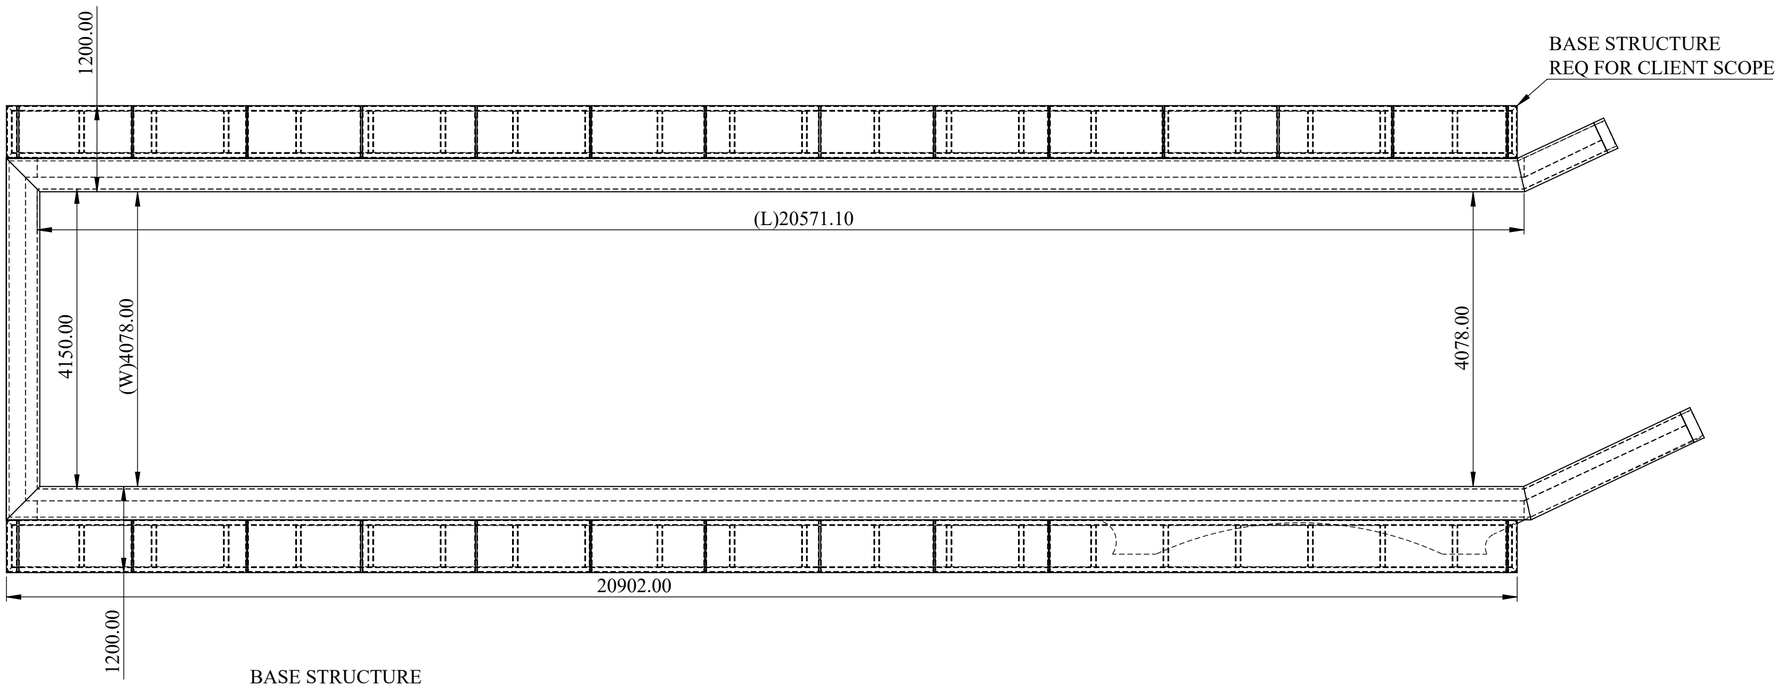

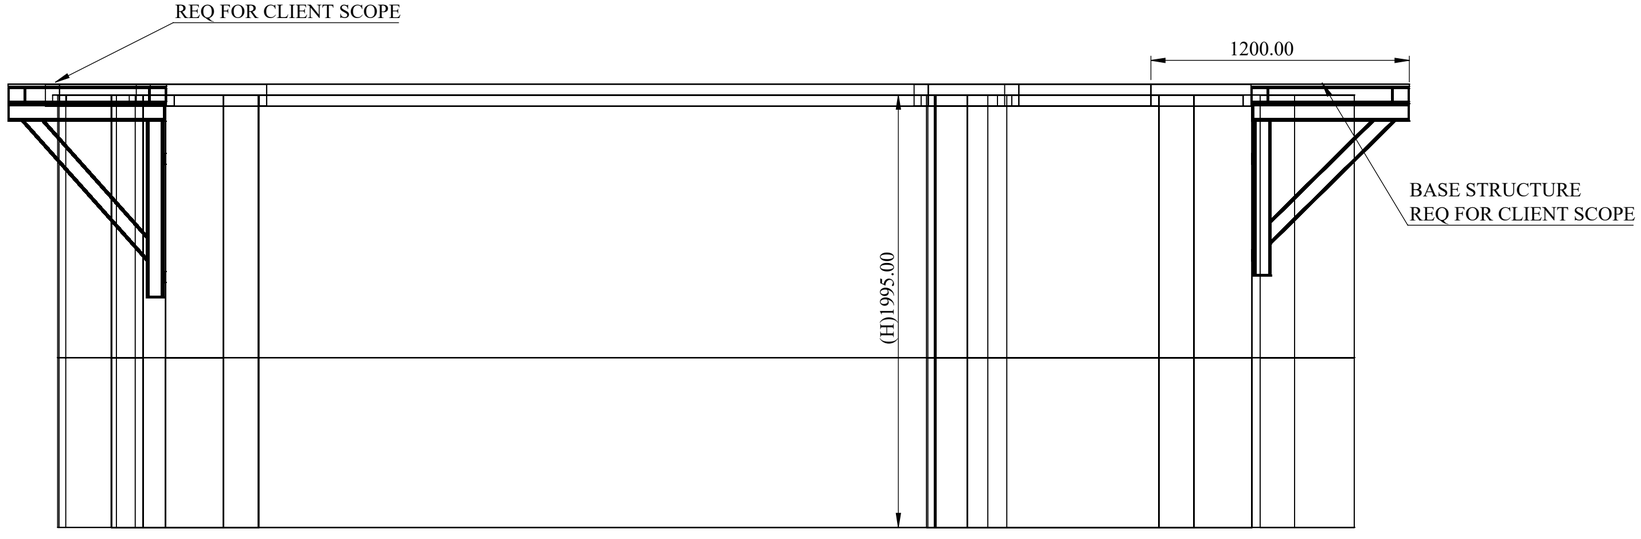

NOTE :
CIVIL DRAWING
BASE STRUCTURE IN CLIENT SCOPE.

SPECIAL INSTRUCTION'S :

This drawing & design is the property of NIHVA TECHONOLOGIES PVT. LTD. Not to be sold or copied to any other concern

TITLE - RETRACTABLE ROOF

DWG NO - NTPL

NIHVA TECHNOLOGIES PVT.LTD.PUNE
Website - www.nihva.com

	NAME	SIGNATURE	DATE
DRAWN	V.W.		16-07-2026
CHK'D	S.P.		19-07-2026
APPV'D	V.T.		19-07-2026

PRODUCT - CENTER OPENING RETRACTABLE ROOF
CLIENT NAME - YASHWANT
SITE LOCATION - CHENNAI
MATRIAL -
QTY - 1
SCALE :
SHEET 2 OF 2

If any queries contact - info@nihva.com
ALL DIMENSION ARE IN mm
A2
PROJECTION METHOD: