

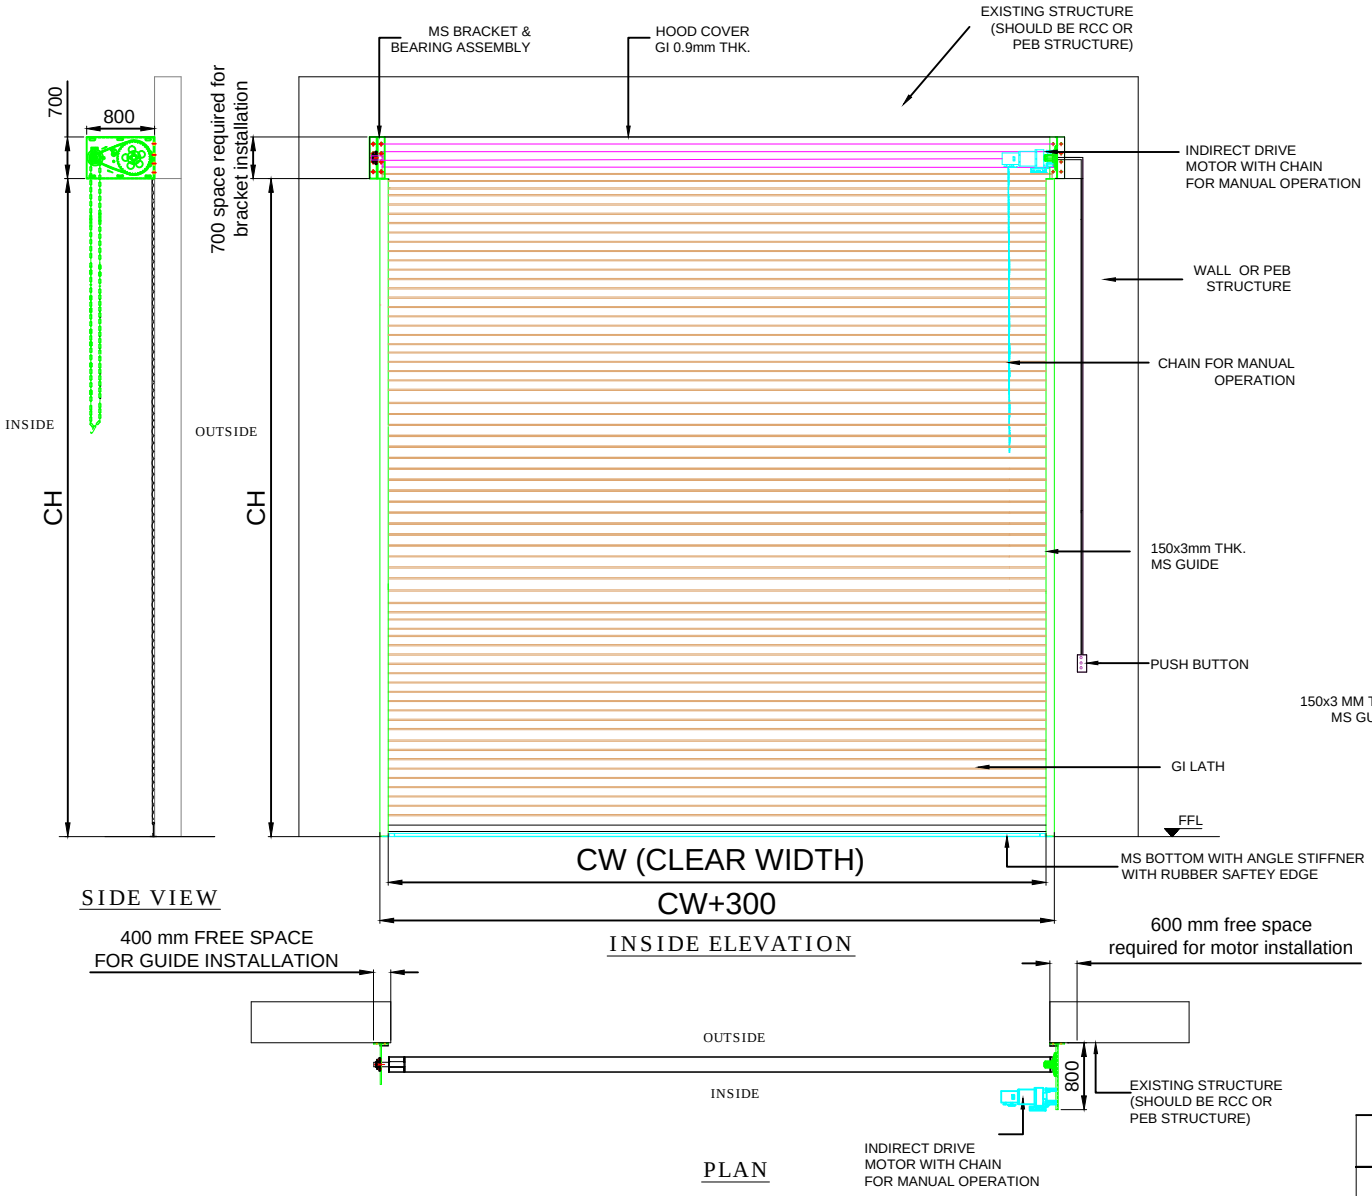


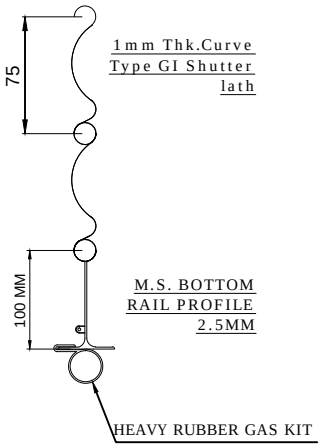

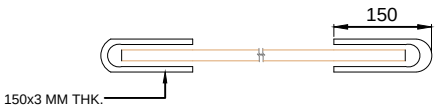

CLEAR WIDTH (CW)	CLEAR HEIGHT (CH)	QUANTITY
6500	7000	1
5000	6000	1

DIMENSION :

CLEAR WIDTH	CLEAR HEIGHT	QUANTITY
6500 mm	7000 mm	01 NOS.
5000 mm	6000 mm	01 NOS.

NOTE:
1. REQUIRED STRUCTURE FOR SHUTTER SHALL BE IN CLIENT SCOPE.
2. ONE COAT OF RED OXIDE PRIMER WILL BE GIVEN TO NON GI COMPONENT OF SHUTTER.

MATERIAL :

THICKNESS :

NOTE: REQUIRED STRUCTURE FOR DOOR SHOULD BE IN CLIENT SCOPE.

NIHVA TECHNOLOGIES PVT. LTD. PUNE
Email:- info@nihva.com
Website:- www.nihva.com

TITLE:

MOTORIZED ROLLING SHUTTER

CLIENT'S APPROVAL :

CLIENT - S.S.GHORPADE

PROJECT - ROSS PROCESS EQUIPMENT

SITE LOCATION - CHAKAN

DWG. NO. : NIHVA/16-17/189

SCALE: NTS	WT:	SHEET:1 OF 1

DRAWN BY: SURAJ	DATE: 20-03-2017
CHECK : SAGAR P	DATE: 20-03-2017
APPROVED BY- R.K.	DATE: 20-03-2017

If any queries contact : projects@nihva.com

NOTE: ALL DIMENSIONS ARE IN mm

THIS DRAWING & DESIGN IS THE PROPERTY OF NIHVA TECHNOLOGIES. NOT TO BE SOLD OR COPY TO ANY OTHER CONCERN.