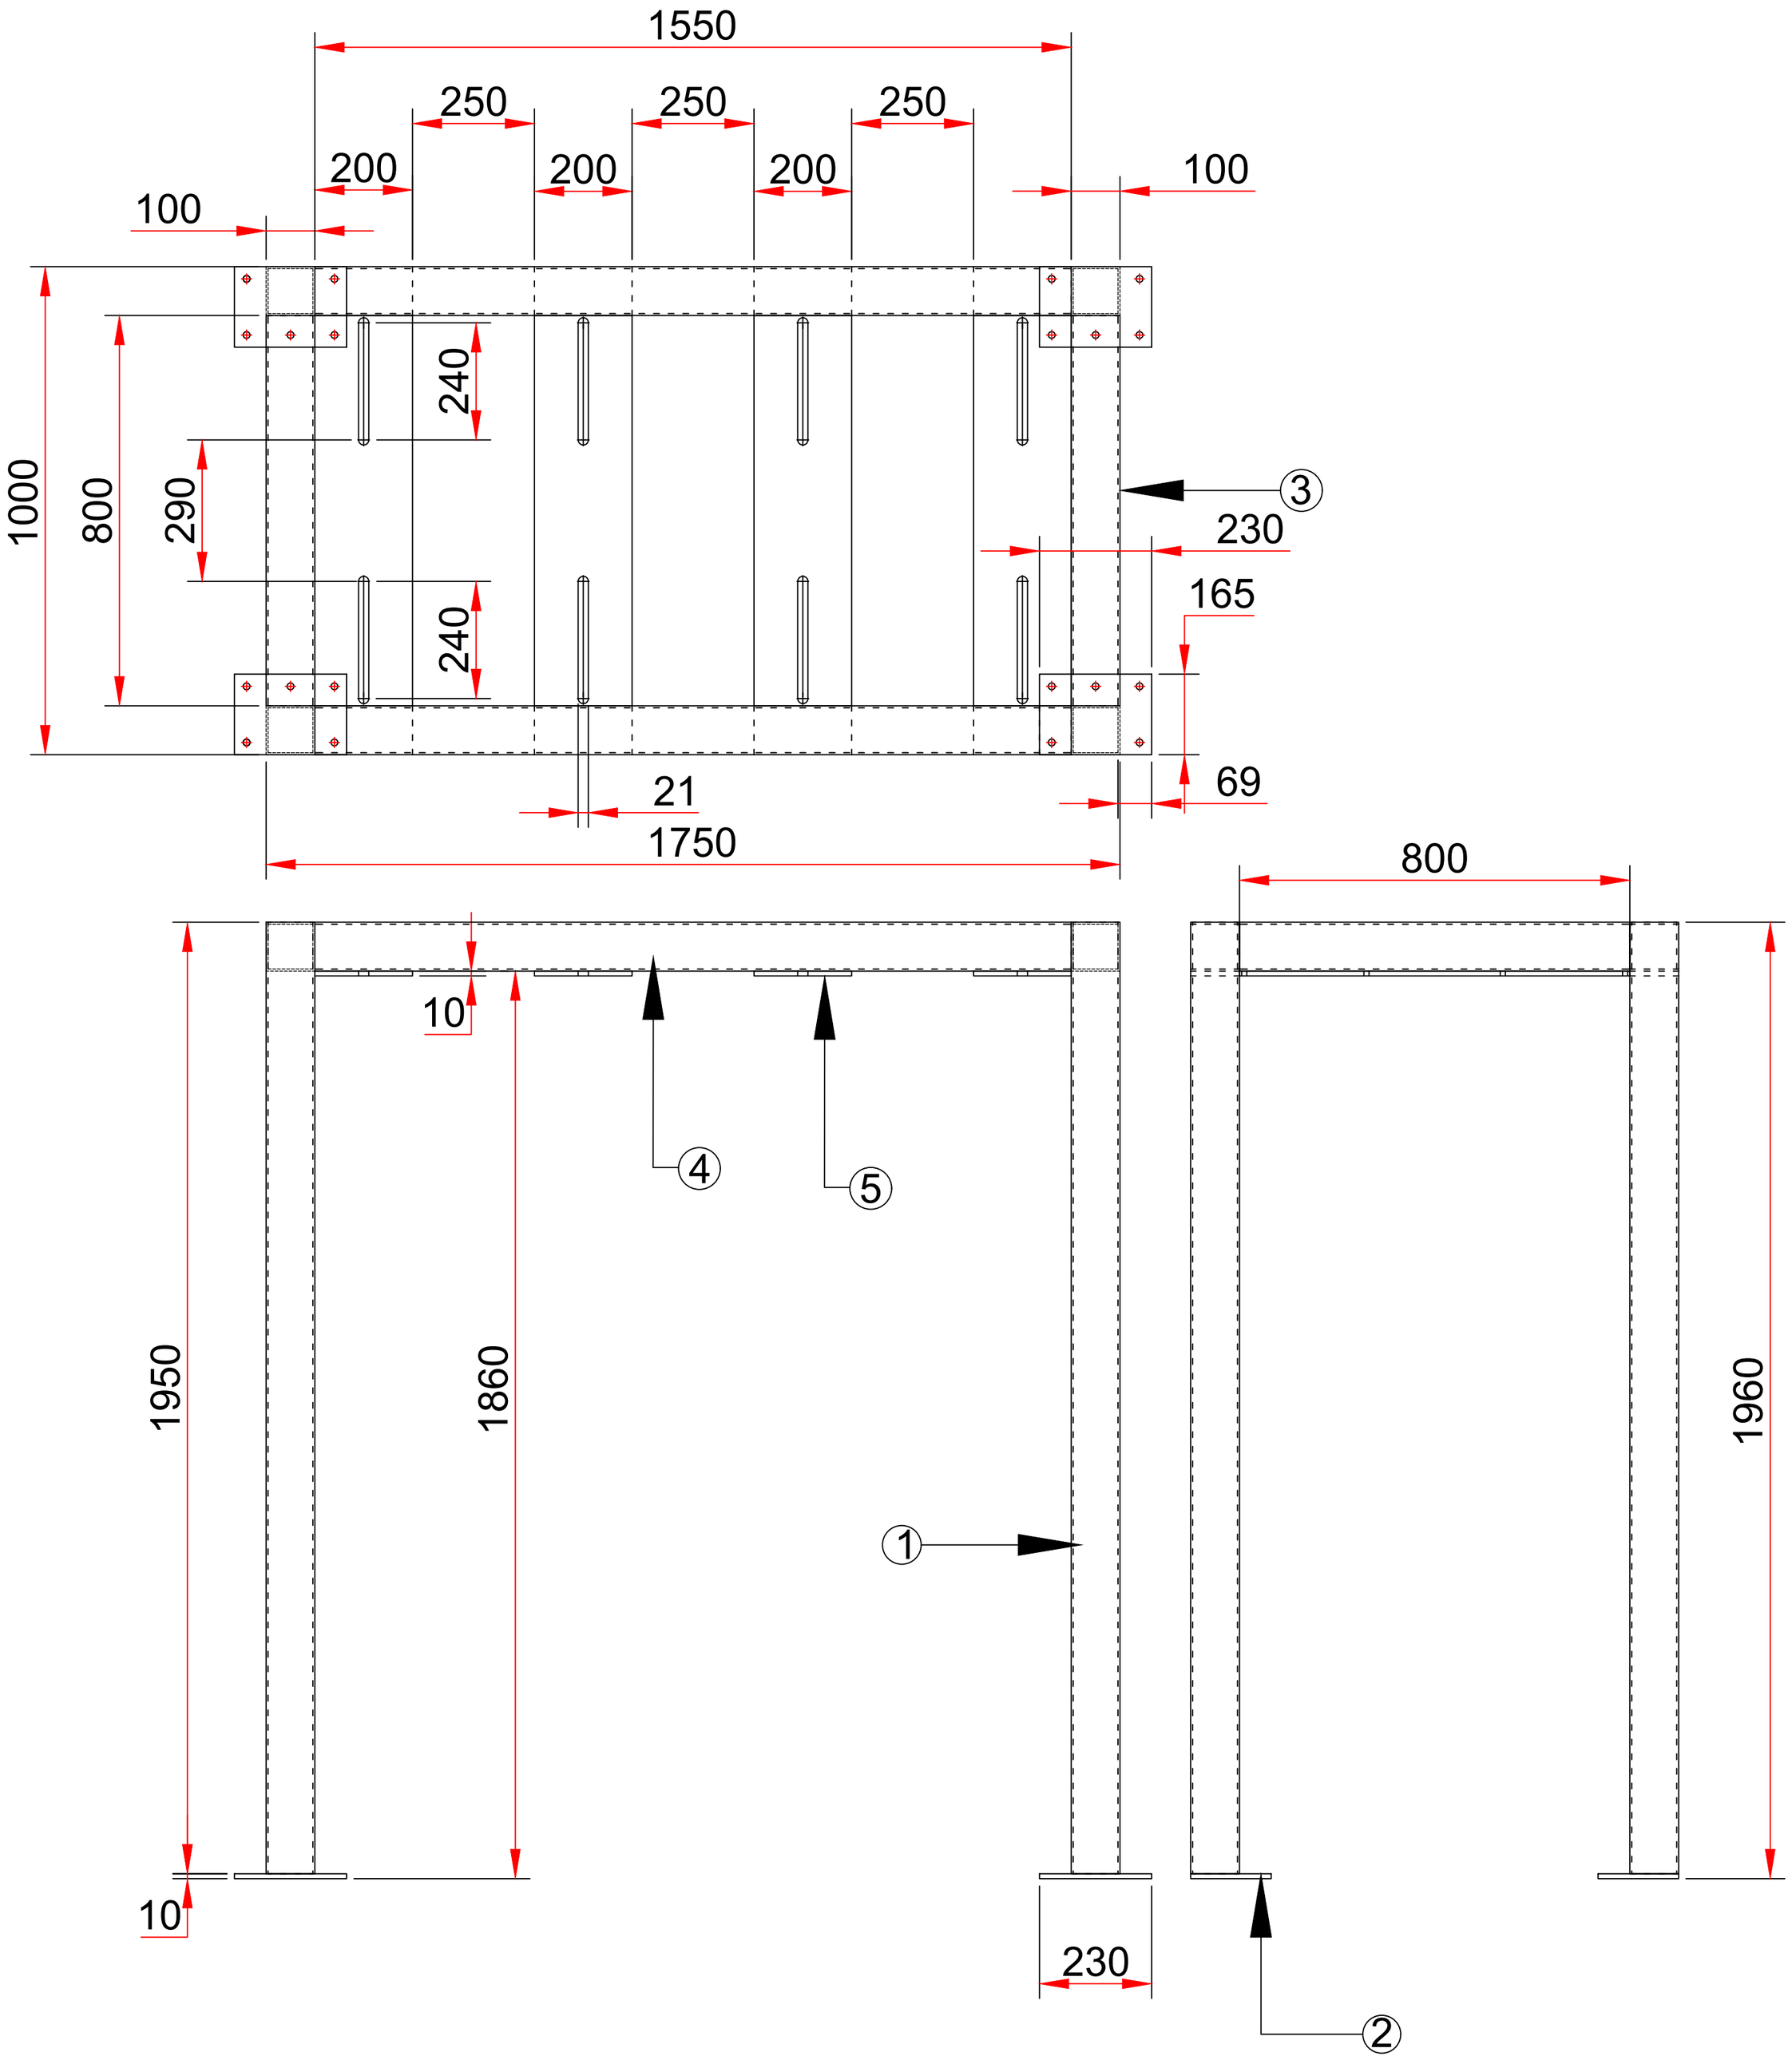


BOM FOR POST			
SL NO.	DESCRIPTION	SPECIFICATION	QTY
1	MS SQ. TUBE	100X100X5X1950L	4 NOS
2	POST SUPPORT PLATE	165X230X10THK	4 NOS
3	MS SQ. TUBE	100X100X5X800L	2 NOS
4	MS SQ. TUBE	100X100X5X1550L	2 NOS
5	ROLLER MNTG PLATE	200 X 1000 X10THK	4 NOS

Rev No.	Revision	Date	Revised By

This drawing & design is the property of NIHVA TECHNOLOGIES. Not to be sold or copied to any other concern.

	NAME	DATE	SIGN
DRAWN	MAHESH S.	13/08/2022	
CHECK	MAHESH S.	13/08/2022	
APPRD.	AMIT K.	13/08/2022	

TITLE:- POST MAIN

NIHVA TECHNOLOGIES PVT. LTD.
NIHVA TECHNOLOGIES PVT. PUNE
Tel : 020 66304033
Email:- info@nihva.com
Website:- www.nihva.com

CLIENT - NAVNEET EDUCATION LTD.

LOCATION - PALGHAR

PRODUCT - | QTY:-1 NO

If any queries contact : design@nihva.com | DWG NO:-NIHVA/22-23/MFG/0062 | REV- 0

ALL DIMENSION ARE IN mm | SCALE: NTS | SCALE:-- 1:1 | SHEET: 01 OF 01