
LOCATION AREA :- SEZ 1 C -GROUND FLOOR- ENTRY

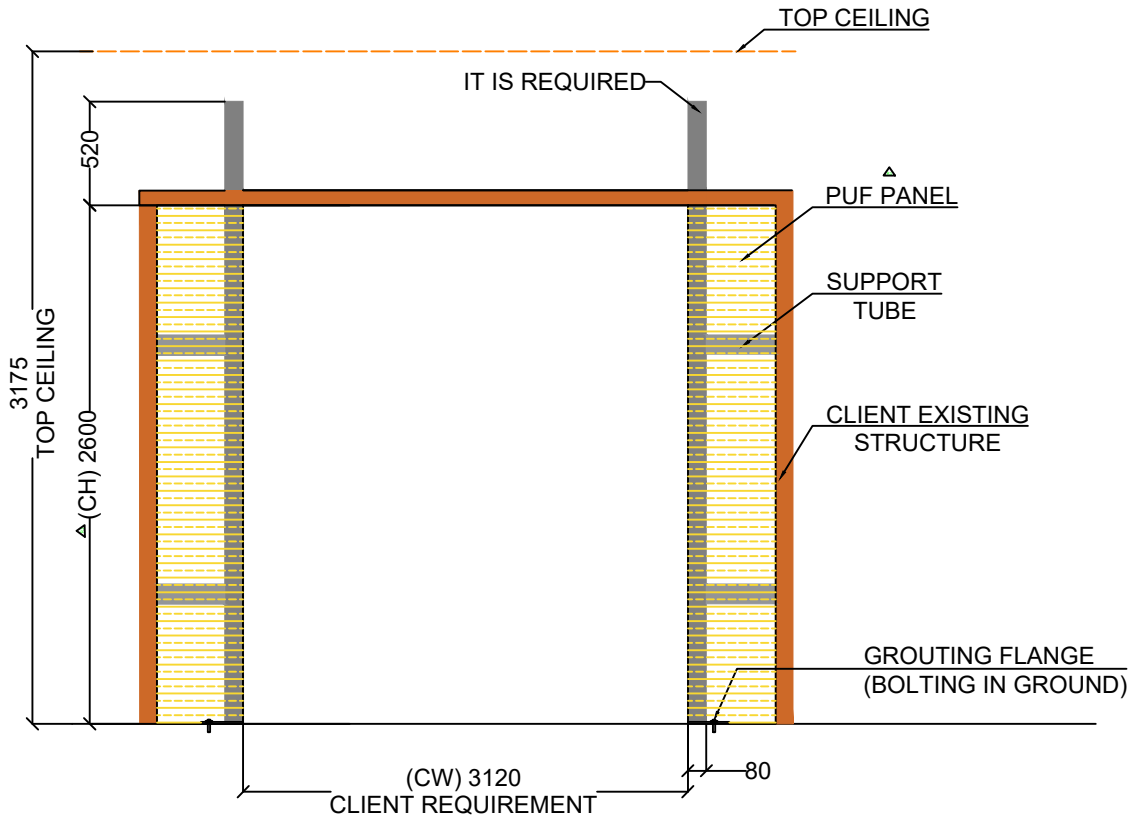

M.S. STRUCTURE DETAILS

Clear Width (CW)	Clear Height (CH)	QTY
3120	**2600**	02

NOTE :-
1. ALL DIMENSIONS ARE IN MM
2. THIS DRAWING IS SOLELY MEANT TO BE UNDERSTOOD.

Sr.No	DESCRIPTION	REV.NO	DRAWN	DATE
1.	HEIGHT CHANGE 2460 mm TO 2600mm	REV.01	S.J.	02.12.2024
2.	PUF PANEL ADD	REV.01	S.J.	02.12.2024

This drawing & design is the property of NIHVA TECHNOLOGIES. Not to be sold or copied to any other concern.

TITLE:- HIGH SPEED DOOR STRUCTURE DRAWING

	NAME	SIGN	DATE
DRAWN	S.J		14.11.2024
CHECK	S.W.		14.11.2024
APPRD.	V.T		14.11.2024

If any queries contact : projectsupport@nihva.com

ALL DIMENSION ARE IN mm

NIHVA TECHNOLOGIES PVT. LTD. PUNE
Tel : 020 66304033
Email:- info@nihva.com
Website:- www.nihva.com

CLIENT - SERUM INSTITUTE OF INDIA PVT.LTD

PROJECT - HIGH SPEED DOOR ST.

FORMAT NO - NIHVA-DD-F-03

DWG. NO. : NIHVA/24-25/SM/24100101 | REV- 01

SCALE: NTS | WT: | SHEET: