
LOCATION AREA :- SEZ 6 - SECOND FLOOR- ENTRY

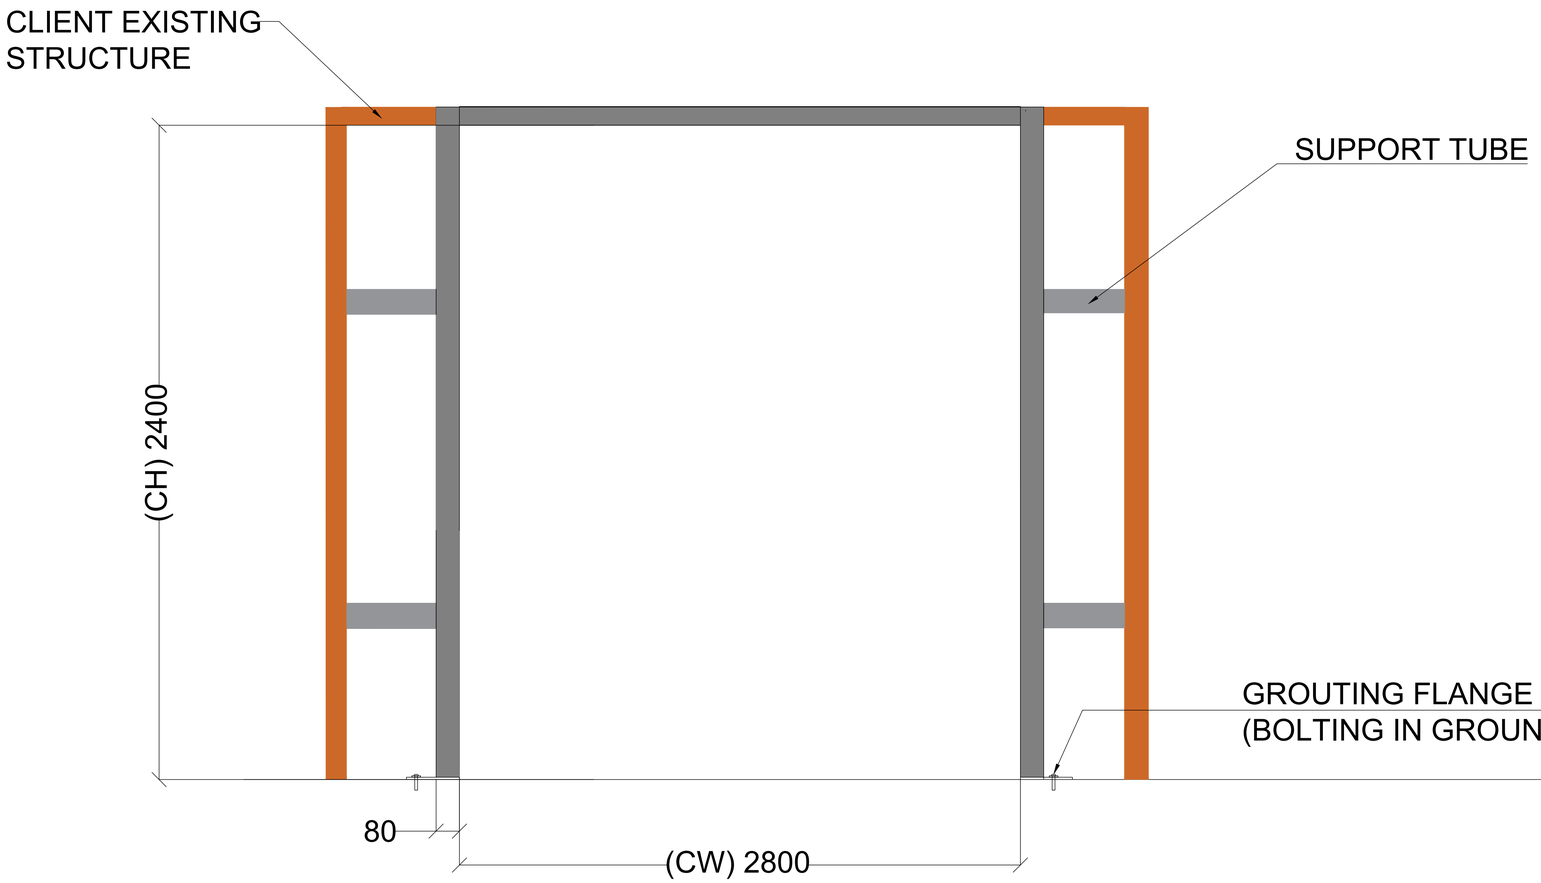

M.S. STRUCTURE DETAILS

Note:-
1. All Dimensions are in mm
2.This drawing is solely meant to be understood.
3. ACP sheet RAL Code Confirm by client

Clear Width (CW)	Clear Height (CH)	QTY
2800	**2400**	02

This drawing & design is the property of NIHVA TECHNOLOGIES. Not to be sold or copied to any other concern.

TITLE:-	HIGH SPEED DOOR STRUCTURE DRAWING			NIHVA TECHNOLOGIES PVT. LTD. PUNE Tel : 020 66304033 Email:- info@nihva.com Website:- www.nihva.com	
	NAME	SIGN	DATE		
DRAWN	S.J		22.10.2024	CLIENT - SERUM INSTITUTE OF INDIA PVT.LTD	
CHECK	S.W.		23.10.2024	PROJECT - HIGH SPEED DOOR ST.	
APPRD.	V.T		23.10.2024	FORMAT NO - NIHVA-DD-F-03	
If any queries contact : projectsupport@nihva.com				DWG. NO. : NIHVA/24-25/SM/24100601	REV- R00
ALL DIMENSION ARE IN mm				SCALE: NTS	WT: SHEET: