


TOP VIEW

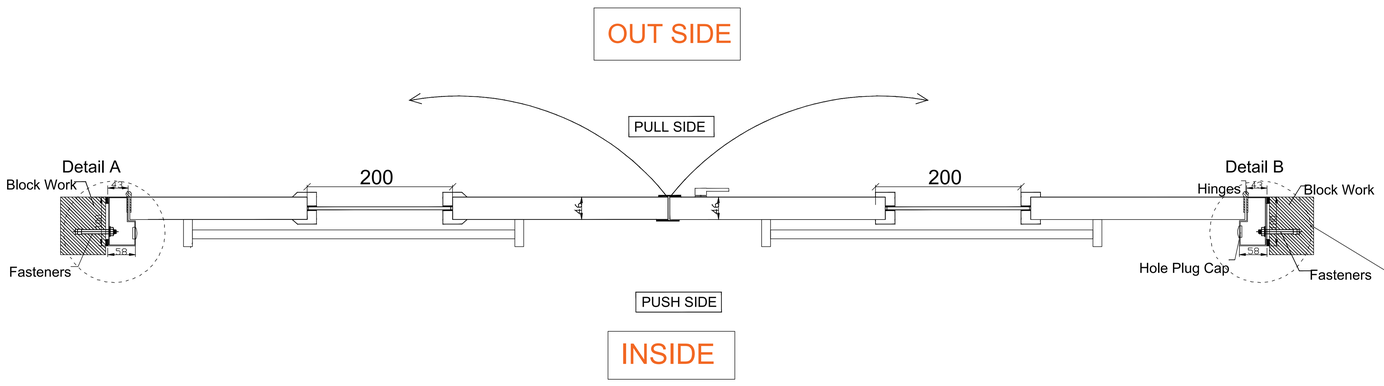


SECTION 'X'-'X'

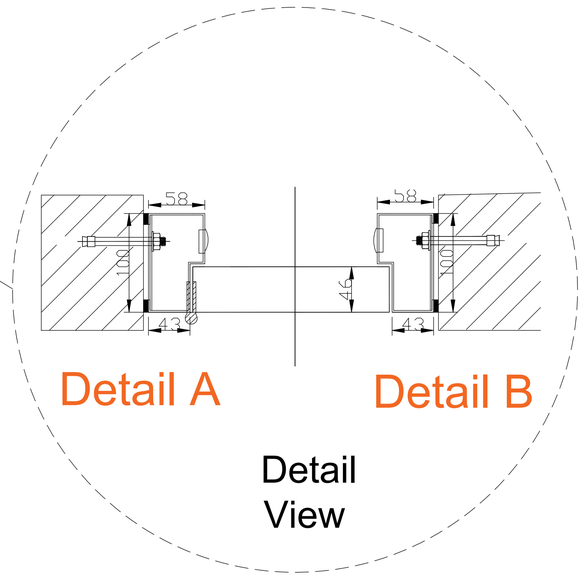

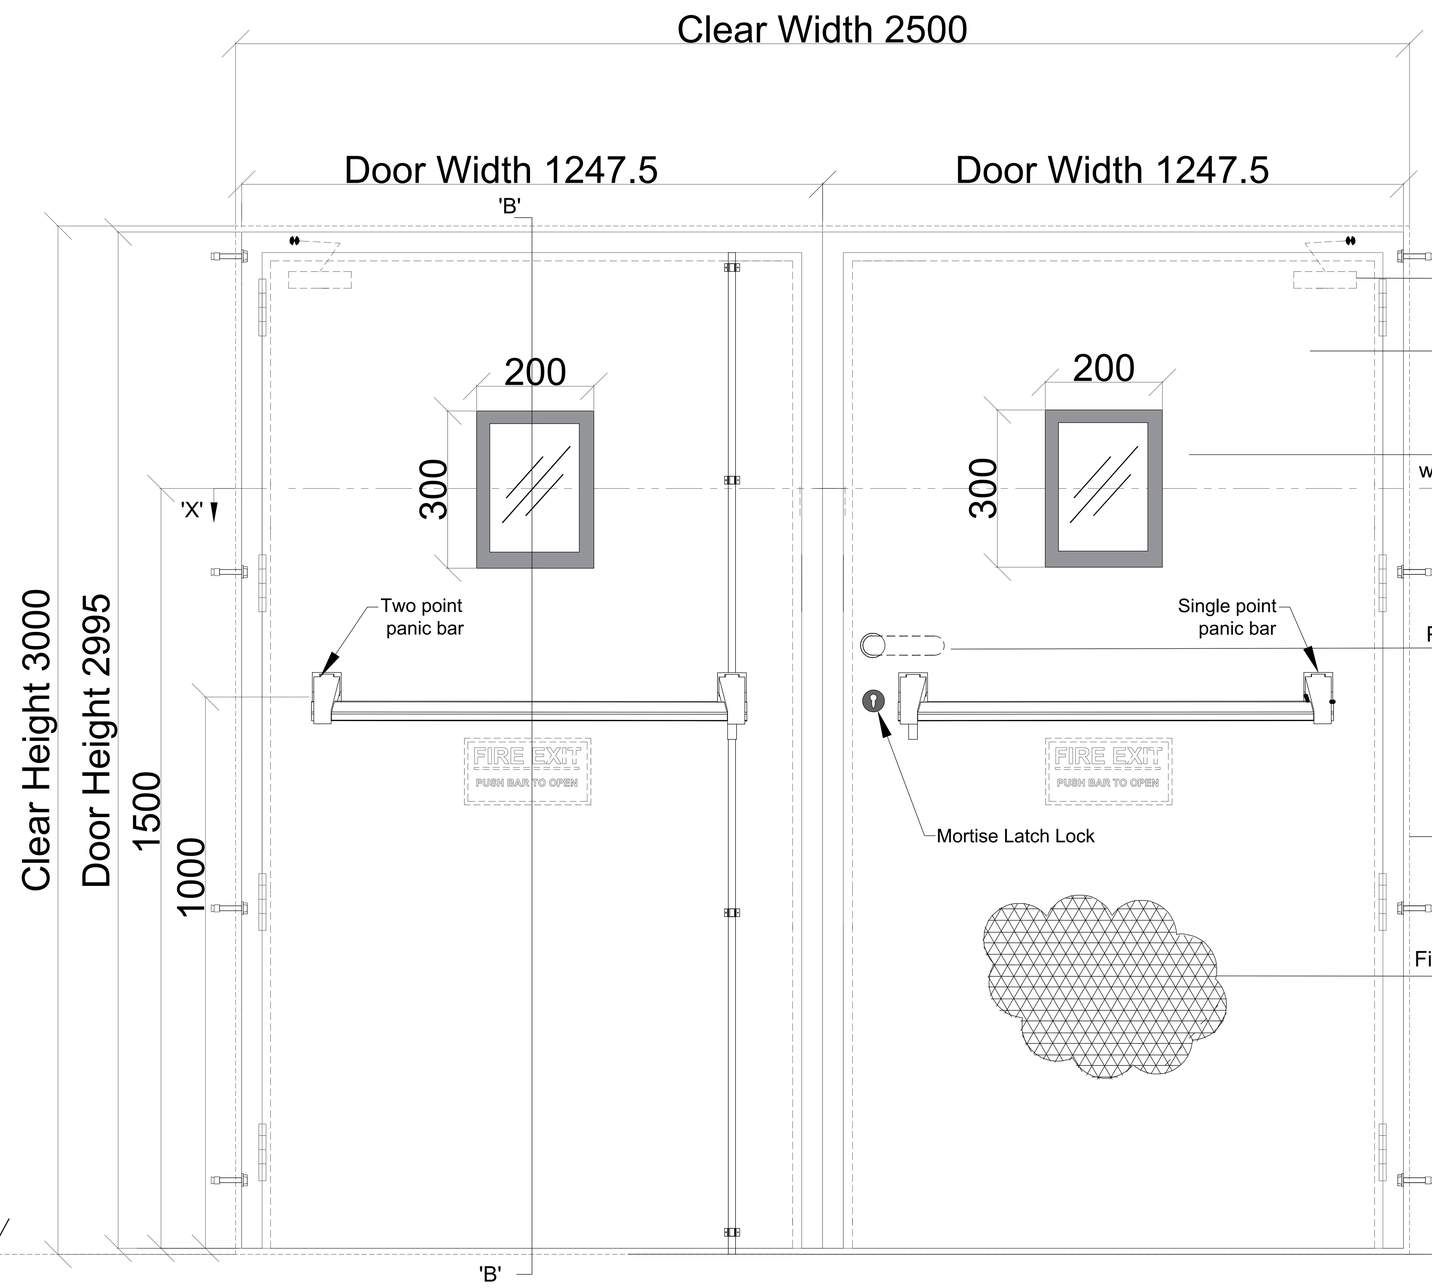

ELEVATION

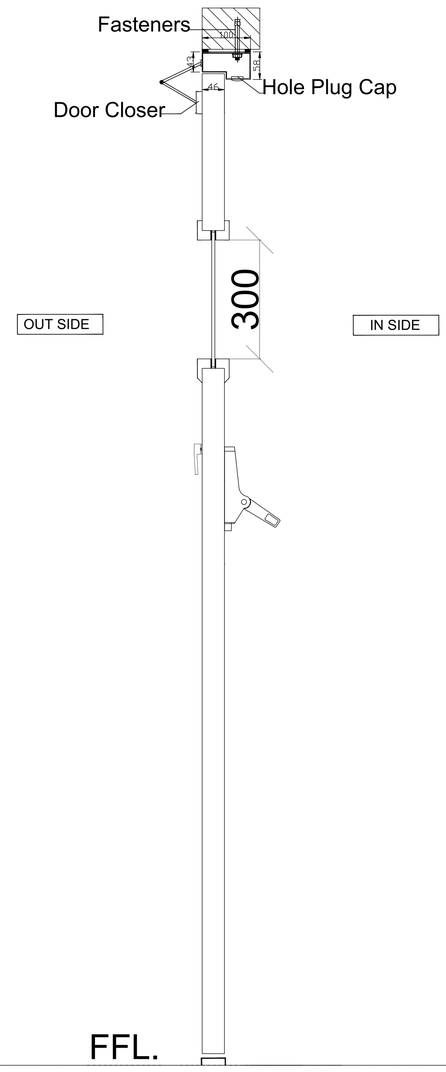

SECTION B-B

TECHNICAL SPECIFICATION :

Sr.	DESCRIPTION & DETAILS
01	Door frame - 100X58 mm x1.6mm thick G.I. Sheet
02	Door Shutter - 46 mm x1.2mm thick G.I. Sheet
03	SS Ball Bearing Hinges 4"x3"x3mm
04	Single Point Panic Bar
05	Tow Point Panic Bar
06	External Panic Trim
07	Anchor Fasteners (M10x100mm Dia)
08	Heavy Duty Door Closer (TS 1000)
09	Vision Window With 6mm fire Rated Glass
10	Fire Rating - 120 Minutes
11	Mortise Latch Lock

Note :-

1. All Dimension are in mm
2. This drawing is only for understanding purpose
3. RAL code confirm by client

SIZE:

Sr.	Clear Width	Clear Height	Qty
01	2500	3000	02

This Drawing & Design is the property of NIHVA TECHNOLOGIES. Not to be sold or copied to any other concern.

TITLE :- FIRE DOOR			NIHVA TECHNOLOGIES PVT. LTD. PUNE
NAME	DATE	SIGN	
S.J.	18/10/2024		CLIENT -
S.M.	18/10/2024		LOCATION -
V.T.	18/10/2024		PRODUCT - FIRE DOOR / QTY-02
If any queries contact : design1@nihva.com			DWG NO - NIHVA/23-24/00XX / REV- 0
MENSION ARE IN mm			SCALE : NTS / SHEET : 01 OF 01

NIHVA TECHNOLOGIES PVT. LTD.
Tel : 020 66304033
Email:- info@nihva.com
Website:- www.nihva.com