
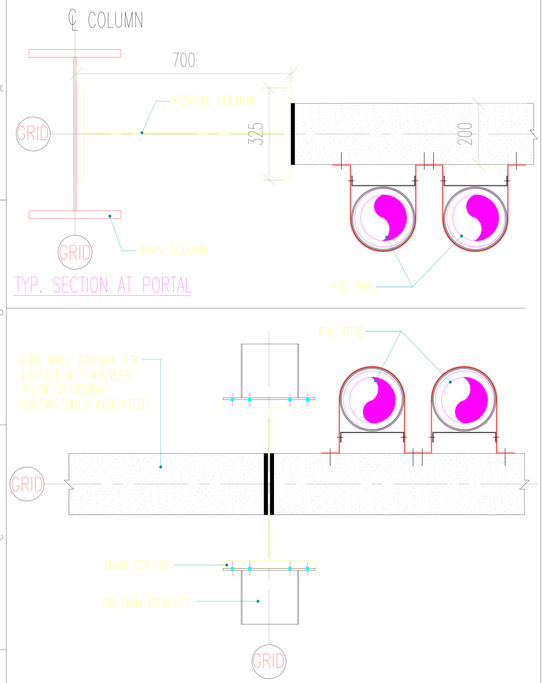



TYP. SECTION AT PORTAL

TYP. SECTION AT COLUMN

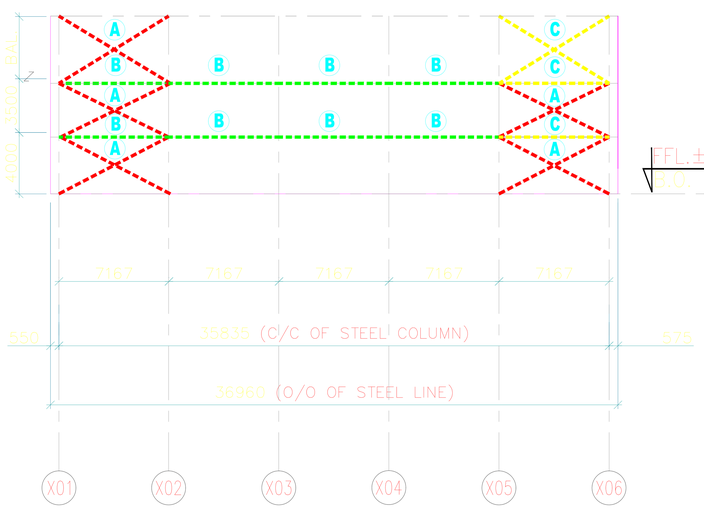

SIDE WALL BRACING ELEVATION ALONG GRID Y01

FOR PIPE BRACING CONNECTION DETAILS REFER GA-008

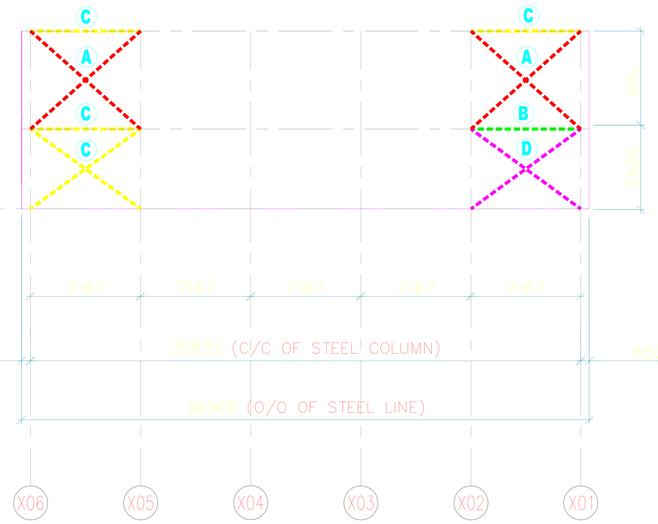


SIDE WALL BRACING ELEVATION ALONG GRID Y25

FOR PIPE BRACING CONNECTION DETAILS REFER GA-008


MARK NO.	PIPE BRACING DIA. (A)
A	100 NB (M) PIPE
B	175 NB (M) PIPE
C	150 NB (M) PIPE
D	125 NB (M) PIPE

GOOD FOR RECORDS

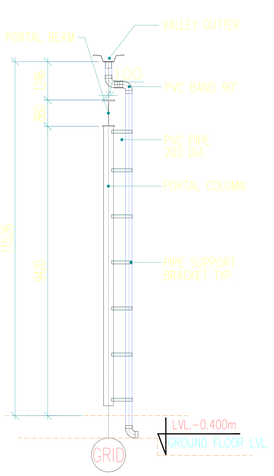


SECTION-X

PORTAL COLUMN LOCATION

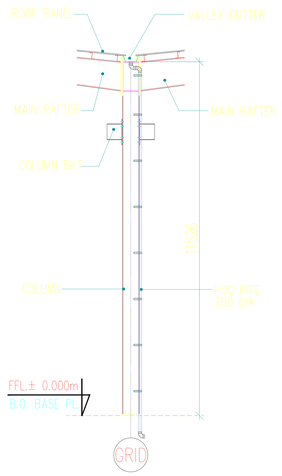


SECTION-Y


NON PORTAL COLUMN

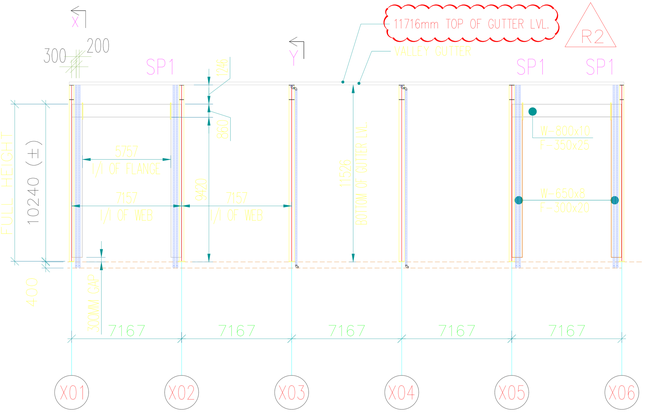


PORTAL ELEVATION AT GRID-Y07

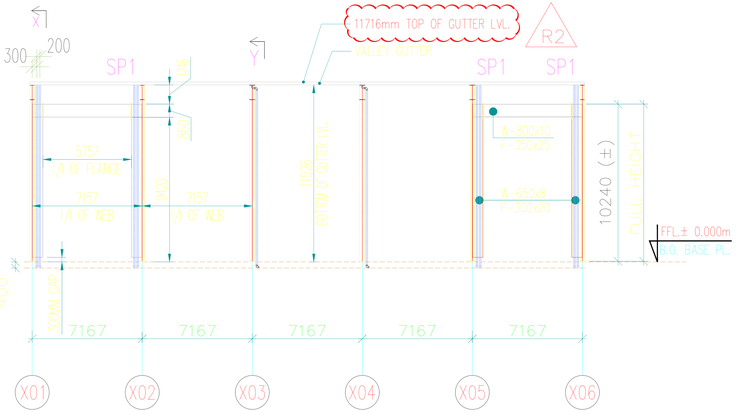


PORTAL ELEVATION AT GRID-Y13

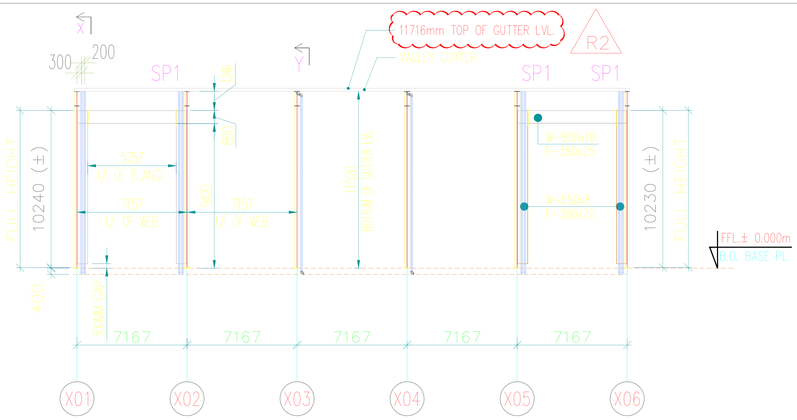


PORTAL ELEVATION AT GRID-Y19

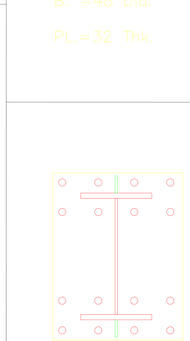

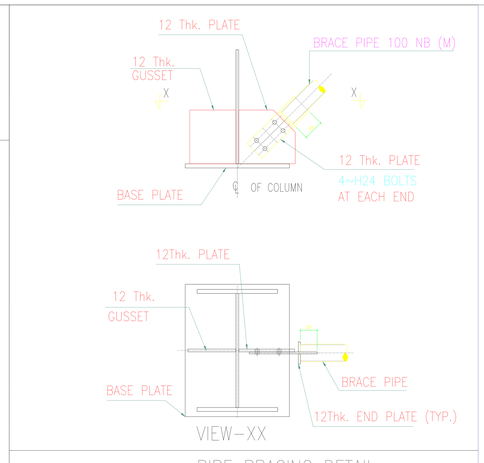

PIPE BRACING DETAIL (@COLUMN BASE)

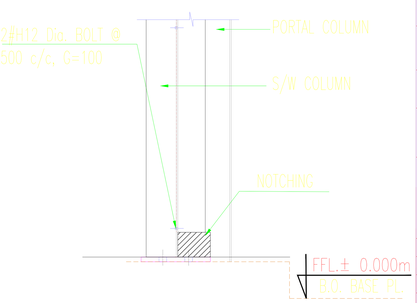

TYP. PORTAL COLUMN BOTTOM DETAIL

ISSUED FOR APPROVAL

SENT ON .....

IN ORDER TO SCHEDULE THIS PROJECT IN THE MOST EFFIDIENT MANNER, RETURN THESE DOCUMENTS, MARKED WITH YOUR COMMENTS, WITHIN TWO WEEKS FROM THE ABOVE MENTIONED DATE. ANY CHANGES MADE AFTER APPROVAL OF THESE DRAWINGS MAY DELAY THE FABRICATION AND DELIVERY PROCESS.

THESE DRAWINGS ARE NOT FOR CONSTRUCTION.

1. ☐ APPROVED
   NO CHANGES, PROCEED WITH FABRICATION.
2. ☐ APPROVED AS NOTED
   FABRICATION MAY PROCEED ON THE BASIS OF CORRECTIONS INDICATED.
3. ☐ NOT APPROVED, RE-SUBMIT FOR APPROVAL.

REVIEWED BY: .....

NAME .....

SIGNATURE ..... DATE .....

Rev.	Description	Name	Checked	Date
R2	GOOD FOR RECORDS	P.B./B.B.	A.A./U.S.	28/07/2023
R1	REVISED AS PER CLIENT COMMENT	P.B./B.B.	A.A./U.S.	18/05/2023
R0	ISSUED FOR APPROVAL	P.B.	A.A./U.S.	30/03/2023

REVISIONS

Project: Pre Engineering Building At GMR-DELHI INTERNATIONAL AIRPORT LTD. NEW DELHI

NOTE:-

Client: GMR-DELHI INTERNATIONAL AIRPORT LTD. NEW DELHI

Process Consultant:

Detailed Engineering Consultant:

Building: GA PARKING

Drawing Title: SIDE WALL BRACING & PORTAL ELEVATION

Everest Industries Limited
ESBS Division, Level 3, Tower T4, Solitaire Corporate Park, Chakala, Andheri (E) Mumbai-400093,India.
Website : www.everestind.com

Drawn by:	P.B.	Scale:	N.T.S.	Date:	30/03/2023	
Checked by:	A.A./U.S.	Project No:		Drawing No:		Revision:
Design By	A.A.	ESBS/PB-02434:01.01.01		GA-009		R2

NOTE:-
1. All rights reserved. This drawing contains proprietary information which is protected by copyright. No part of this drawing may be reproduced, translated in computer language, or transmitted in any form whatsoever without the prior written consent of EVEREST INDUSTRIES LIMITED

SHEET SIZE-A3