PO NO: 206

DOOR NO:- D1 TO D3

QTY- 03 NOS

MATERIAL:-G.I

DOOR HANDLING:
DOUBLE LEAF DOOR? HAND ACTIVE

INFILL: HONEY COMB

RAL NO FRAME:- ????
RAL NO LEAF:- ????

PANIC BAR :
MODEL NO.- LOCKWOOD MAKE
PE RM501P
PHT LOCK :
MODEL NO. LOCKWOOD MAKE
PE ACC004


DOOR CLOSER : STD ARM - MODEL NO-YADC 6003 -YALE MAKE

ACCESSORIES:-
1.SS BALL BEARING HINGES 3S2BB403030-CE-M =YALE MAKE
2.SMOKE SEAL-S88BL-PEMKO MAKE


FRAME SHEET THIK.1.2mm
LEAF SHEET THIK.0.8 mm

POWDER COATED METAL CAP WITH RAL


2 HRS FIRE RATED

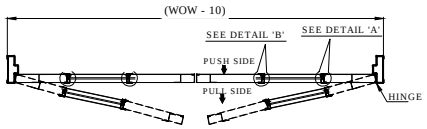

TOP VIEW

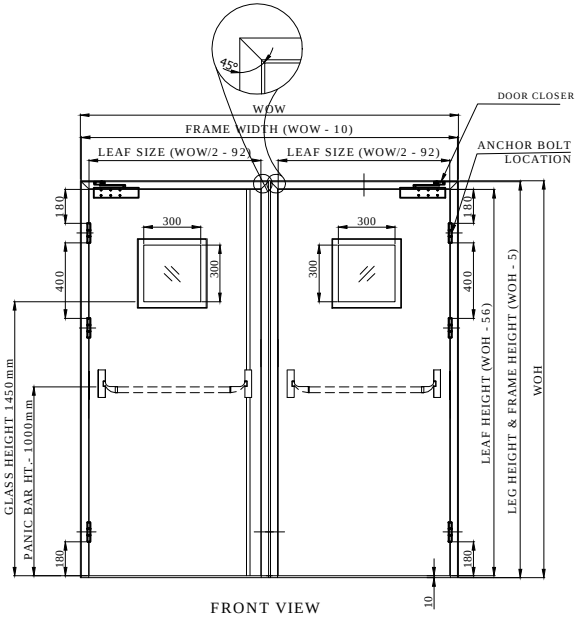


FRONT VIEW

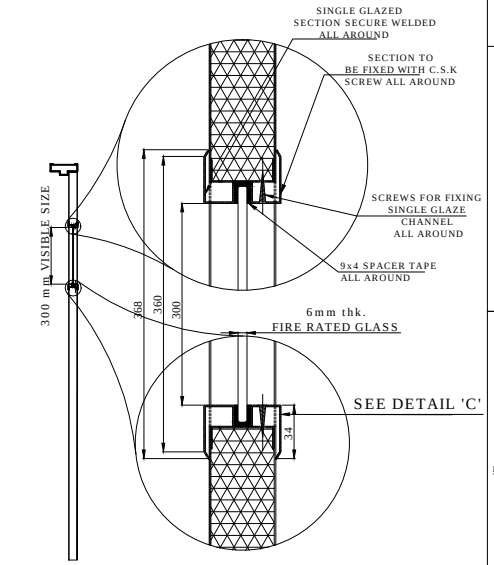


SIDE VIEW SECTION A-A'

SINGLE GLAZE FIXING DETAIL

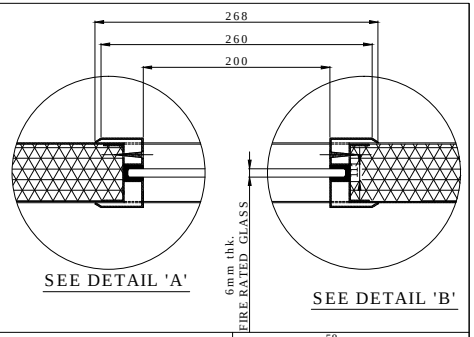



SEE DETAIL 'A'

SEE DETAIL 'B'

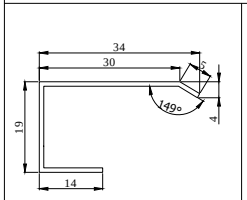


SEE DETAIL 'C'

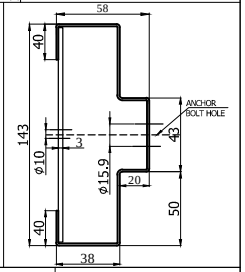

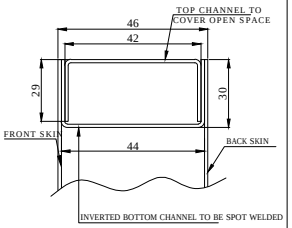

DOOR TOP SECTION DETAIL

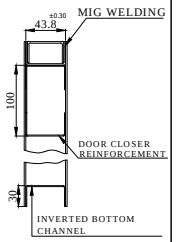

DOOR BOTTOM & TOP DETAIL

SR. NO	WALL OPENING WIDTH	WALL OPENING HEIGHT	QTY	RAL	LOCATION	HARDWARE
03	1500	2140	01	9002	Admin Building (FD5B) - Stair Entry	Double leaf Fire door with Glass vision panel, Panic bar Inside and Pull handle outside
02	1500	2130	01	9002	Admin Building (GD5A) - Security Room	Double leaf Metal door with Glass vision panel, and Tream Handle both side
01	1500	2215	01	9002	Admin Building (GD5B) - Stair Exit	Double leaf metal door with glass vision panel , Panic bar inside , pull handle outside

TOLERANCE - ±05mm

This drawing & design is the property of NIHVA TECHNOLOGIES. Not to be sold or copied to any other concern.

TITLE: FIRE RATED DOUBLE LEAF STEEL DOOR

NIHVA TECHNOLOGIES PVT. LTD. PUNE
Tel : 020 66304033
Email:- info@nihva.com
Website:- www.nihva.com

	NAME	SIGN	DATE
DRAWN	P.V.A		16.03.2019
CHECK	V.M.T		16.03.2019
APPRD.			

CLIENT - SYNERGY
PROJECT - EMBASSY
SITE LOCATION - CHAKAN, PUNE.

If any queries contact : design@nihva.com
DWG. NO. : NIHVA/18-19/0292 REV- 0
ALL DIMENSION ARE IN mm
SCALE: NTS WT: SHEET: 01 OF 01