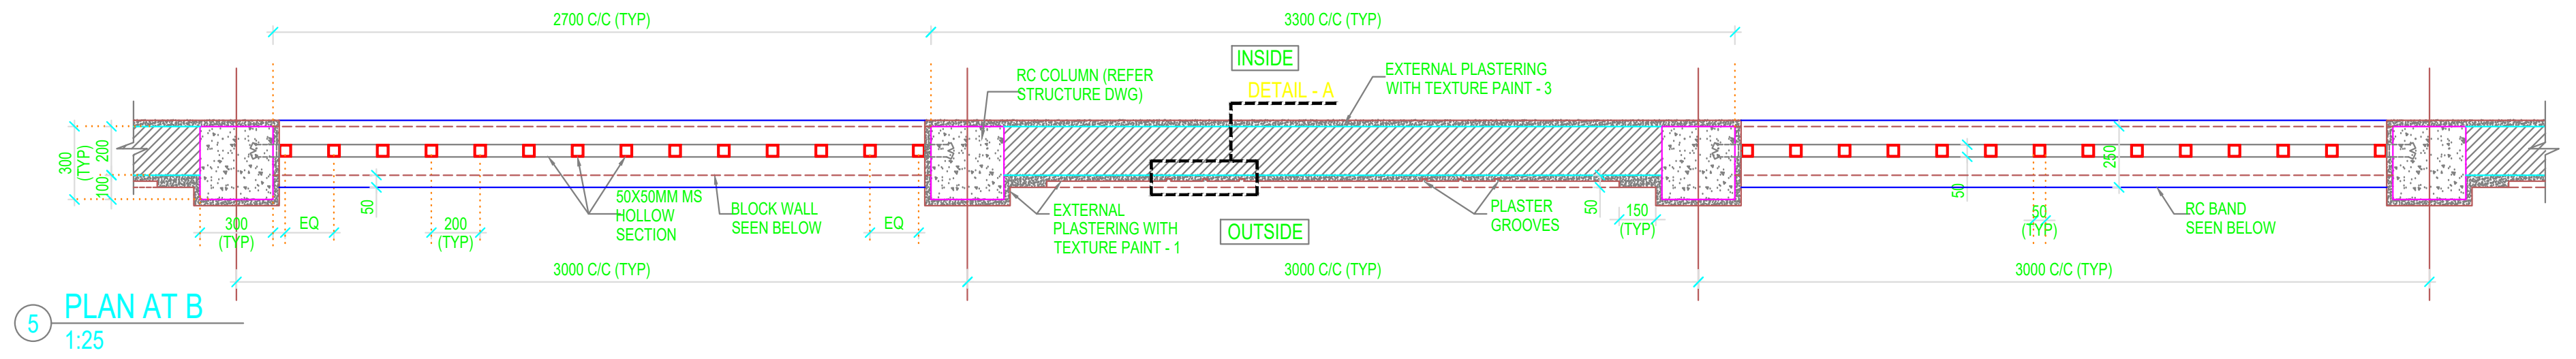
2700 C/C (TYP)
3300 C/C (TYP)
RC COLUMN (REFER STRUCTURE DWG)
INSIDE
DETAIL - A
EXTERNAL PLASTERING WITH TEXTURE PAINT - 3
300 (TYP)
200
100
50X50MM MS HOLLOW SECTION
BLOCK WALL SEEN BELOW
EQ
200 (TYP)
EXTERNAL PLASTERING WITH TEXTURE PAINT - 1
OUTSIDE
PLASTER GROOVES
150 (TYP)
50 (TYP)
RC BAND SEEN BELOW
3000 C/C (TYP)

5 PLAN AT B
1:25

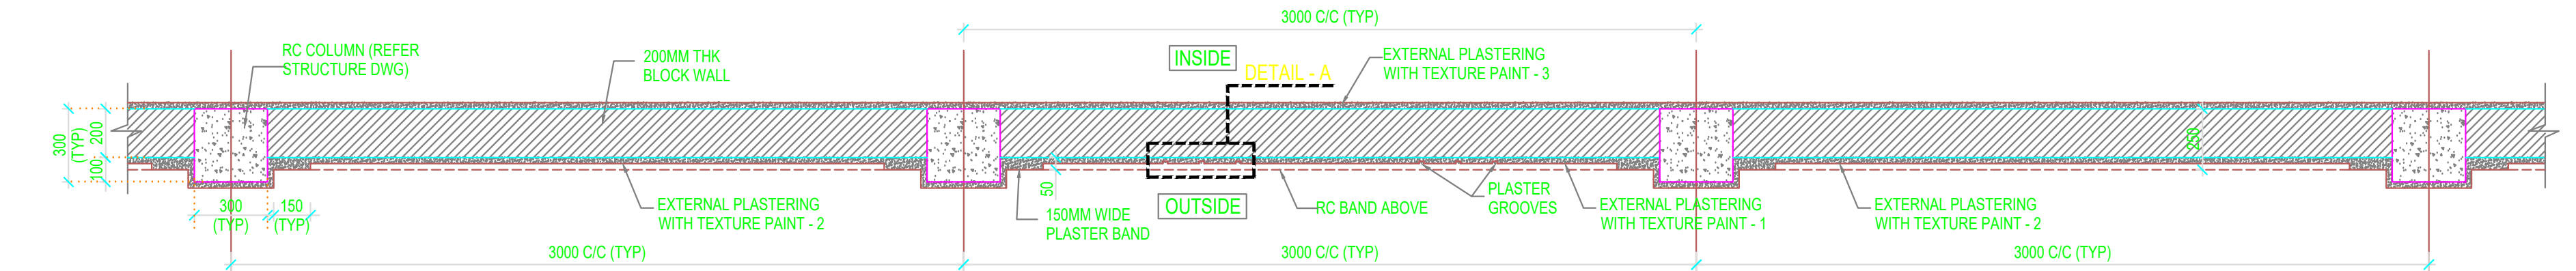
3000 C/C (TYP)
RC COLUMN (REFER STRUCTURE DWG)
200MM THK BLOCK WALL
INSIDE
DETAIL - A
EXTERNAL PLASTERING WITH TEXTURE PAINT - 3
EXTERNAL PLASTERING WITH TEXTURE PAINT - 2
150MM WIDE PLASTER BAND
OUTSIDE
RC BAND ABOVE
PLASTER GROOVES
EXTERNAL PLASTERING WITH TEXTURE PAINT - 1
300 (TYP)
150 (TYP)
3000 C/C (TYP)

4 PLAN AT A
1:25

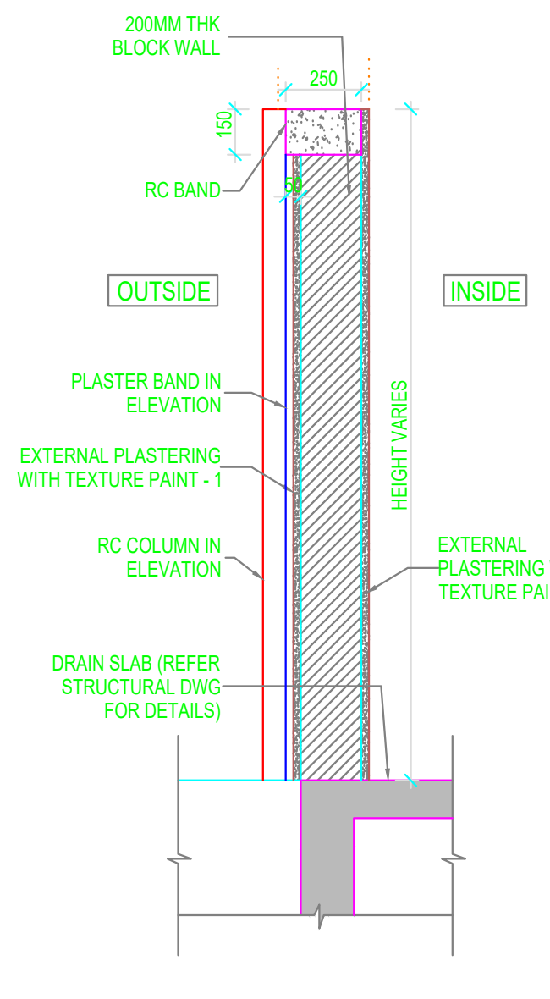
200MM THK BLOCK WALL
250
150
RC BAND
50
OUTSIDE
INSIDE
PLASTER BAND IN ELEVATION
EXTERNAL PLASTERING WITH TEXTURE PAINT - 1
RC COLUMN IN ELEVATION
HEIGHT VARIES
EXTERNAL PLASTERING WITH TEXTURE PAINT - 3
DRAIN SLAB (REFER STRUCTURAL DWG FOR DETAILS)

6 SECTION - 1
1:25

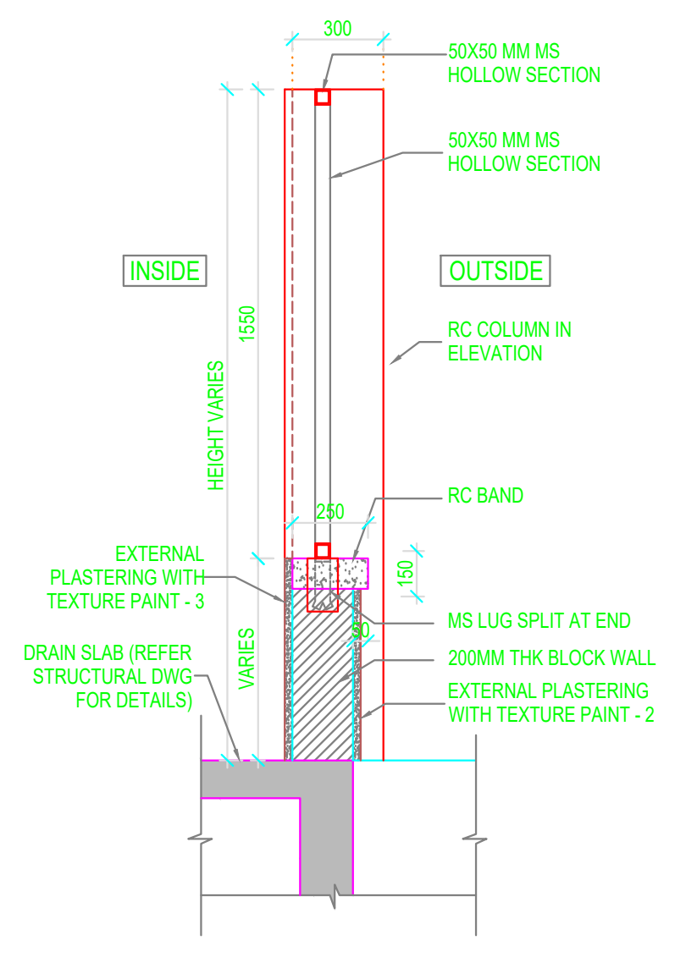
300
50X50 MM MS HOLLOW SECTION
50X50 MM MS HOLLOW SECTION
INSIDE
OUTSIDE
1550
HEIGHT VARIES
RC COLUMN IN ELEVATION
RC BAND
250
150
EXTERNAL PLASTERING WITH TEXTURE PAINT - 3
MS LUG SPLIT AT END
DRAIN SLAB (REFER STRUCTURAL DWG FOR DETAILS)
VARIES
200MM THK BLOCK WALL
EXTERNAL PLASTERING WITH TEXTURE PAINT - 2

7 SECTION - 2
1:25

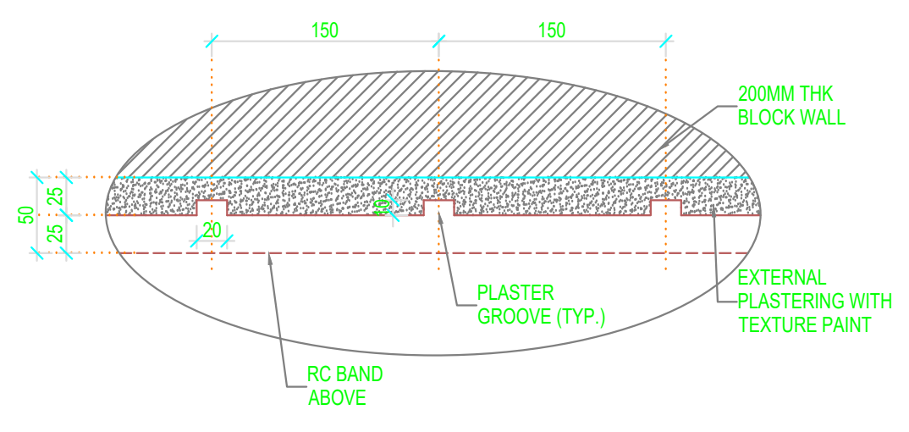
150
150
200MM THK BLOCK WALL
50
25
25
20
PLASTER GROOVE (TYP.)
RC BAND ABOVE
EXTERNAL PLASTERING WITH TEXTURE PAINT

8 DETAIL-A
1:5

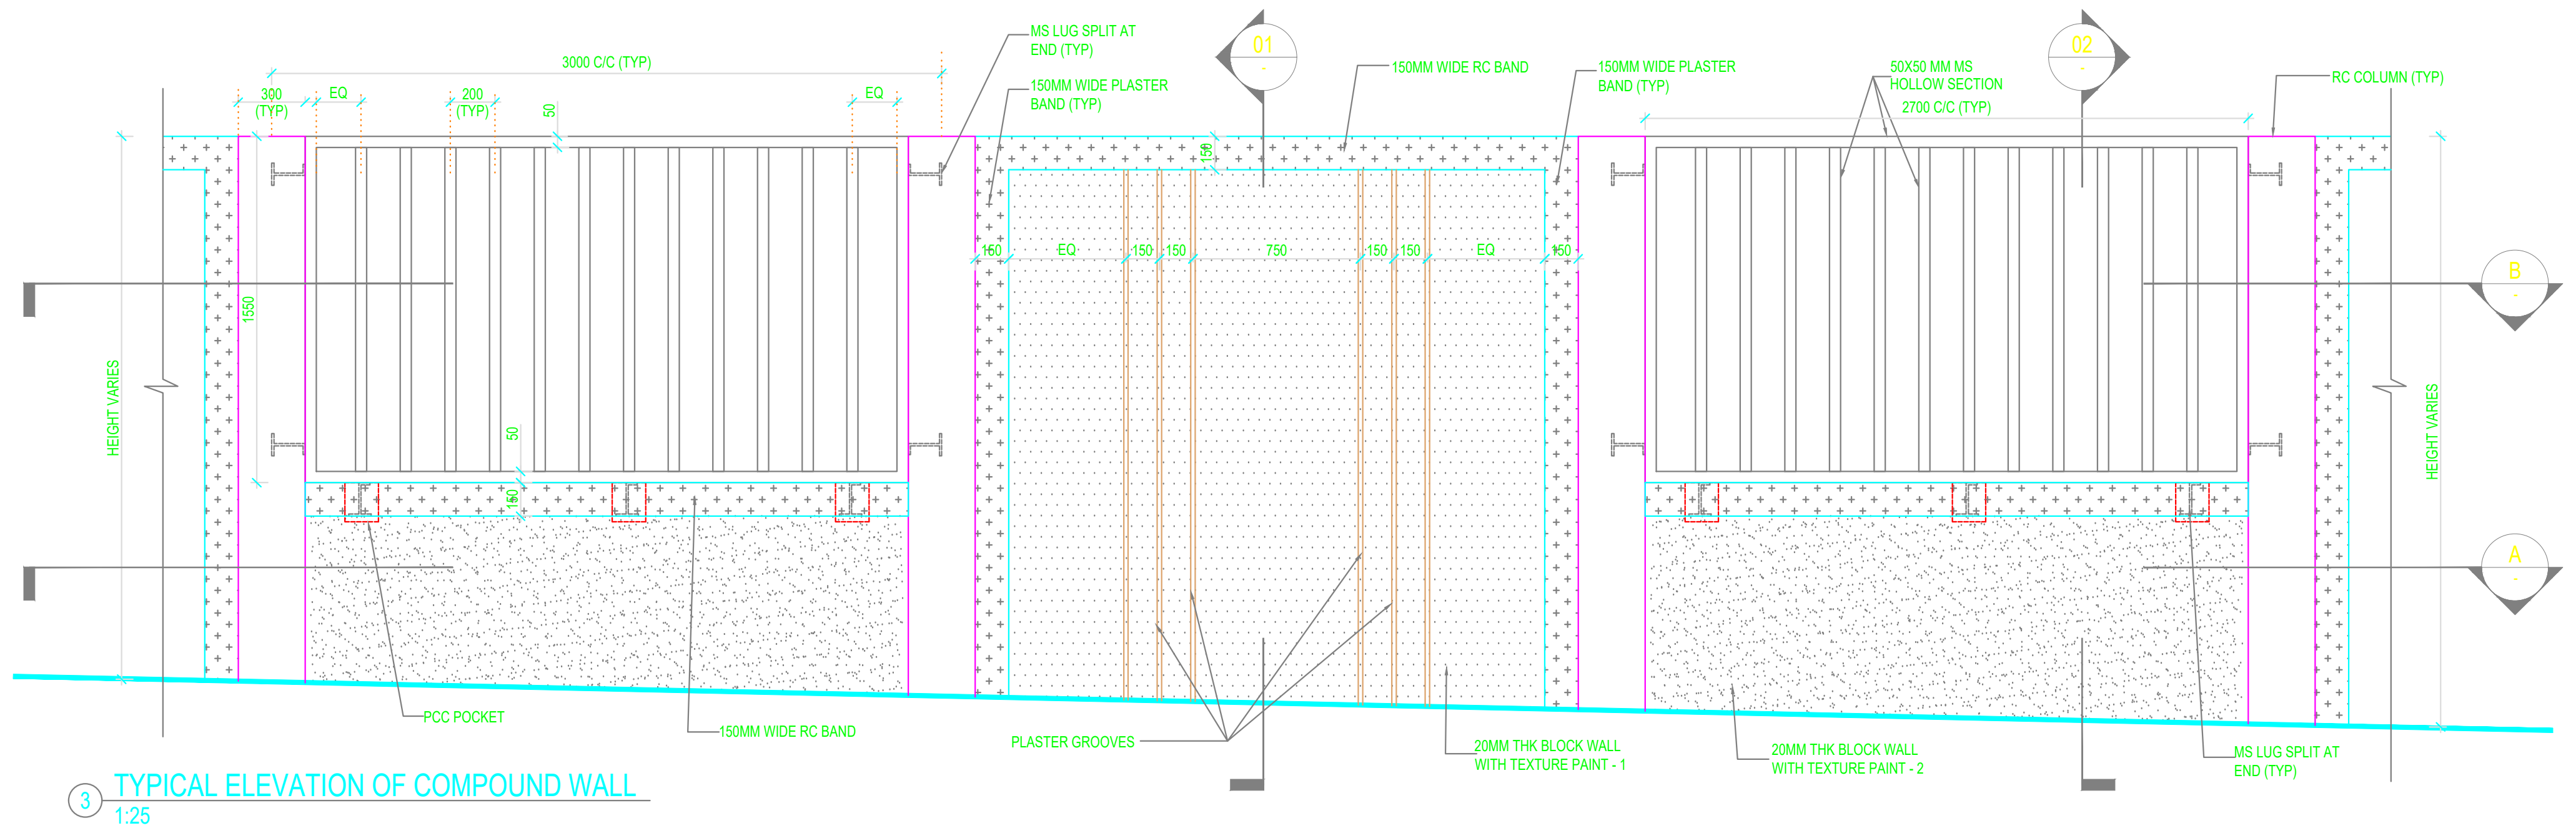
3000 C/C (TYP)
300 (TYP)
EQ
200 (TYP)
MS LUG SPLIT AT END (TYP)
150MM WIDE PLASTER BAND (TYP)
01
150MM WIDE RC BAND
150MM WIDE PLASTER BAND (TYP)
50X50 MM MS HOLLOW SECTION
02
2700 C/C (TYP)
RC COLUMN (TYP)
1550
HEIGHT VARIES
150
750
B
A
PCC POCKET
150MM WIDE RC BAND
PLASTER GROOVES
20MM THK BLOCK WALL WITH TEXTURE PAINT - 1
20MM THK BLOCK WALL WITH TEXTURE PAINT - 2
MS LUG SPLIT AT END (TYP)

3 TYPICAL ELEVATION OF COMPOUND WALL
1:25

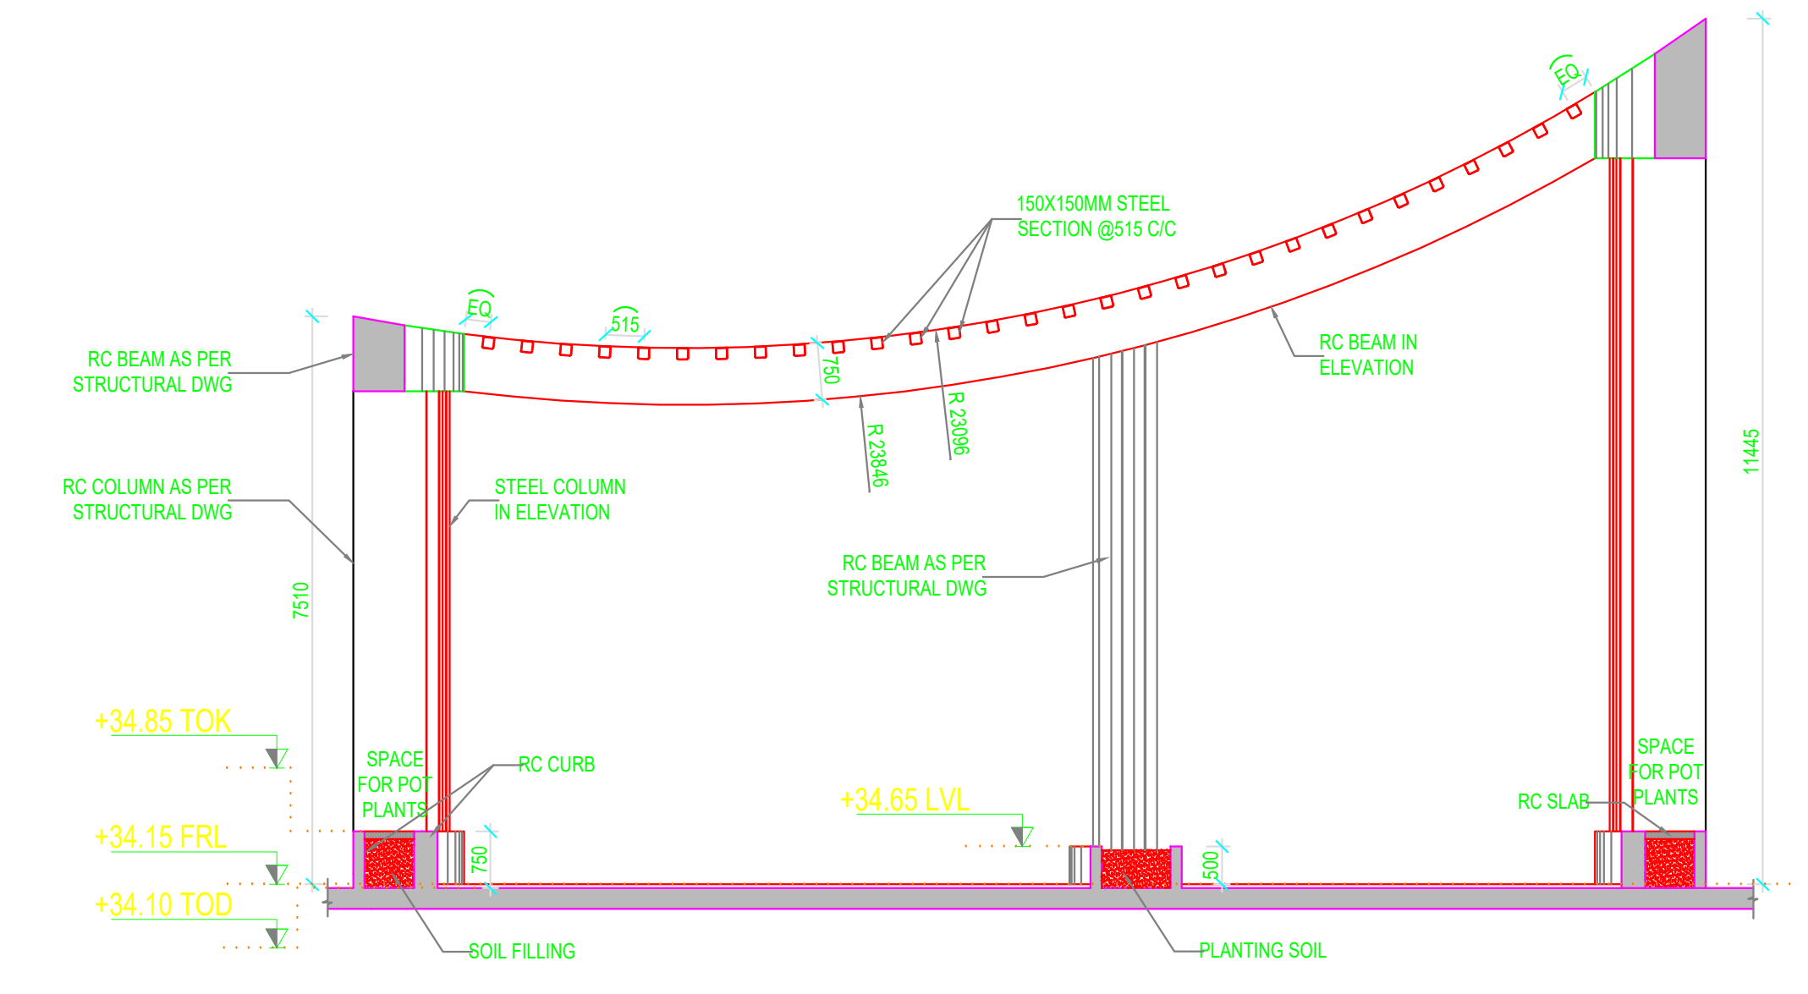
150X150MM STEEL SECTION @515 C/C
RC BEAM AS PER STRUCTURAL DWG
RC COLUMN AS PER STRUCTURAL DWG
EQ
515
750
R 23846
R 23096
RC BEAM IN ELEVATION
STEEL COLUMN IN ELEVATION
RC BEAM AS PER STRUCTURAL DWG
7510
11445
+34.85 TOK
+34.15 FRL
+34.10 TOD
+34.65 LVL
SPACE FOR POT PLANTS
RC CURB
RC SLAB
500
SOIL FILLING
PLANTING SOIL

10 ELEVATION OF ENTRANCE PORTAL - 1
1:100

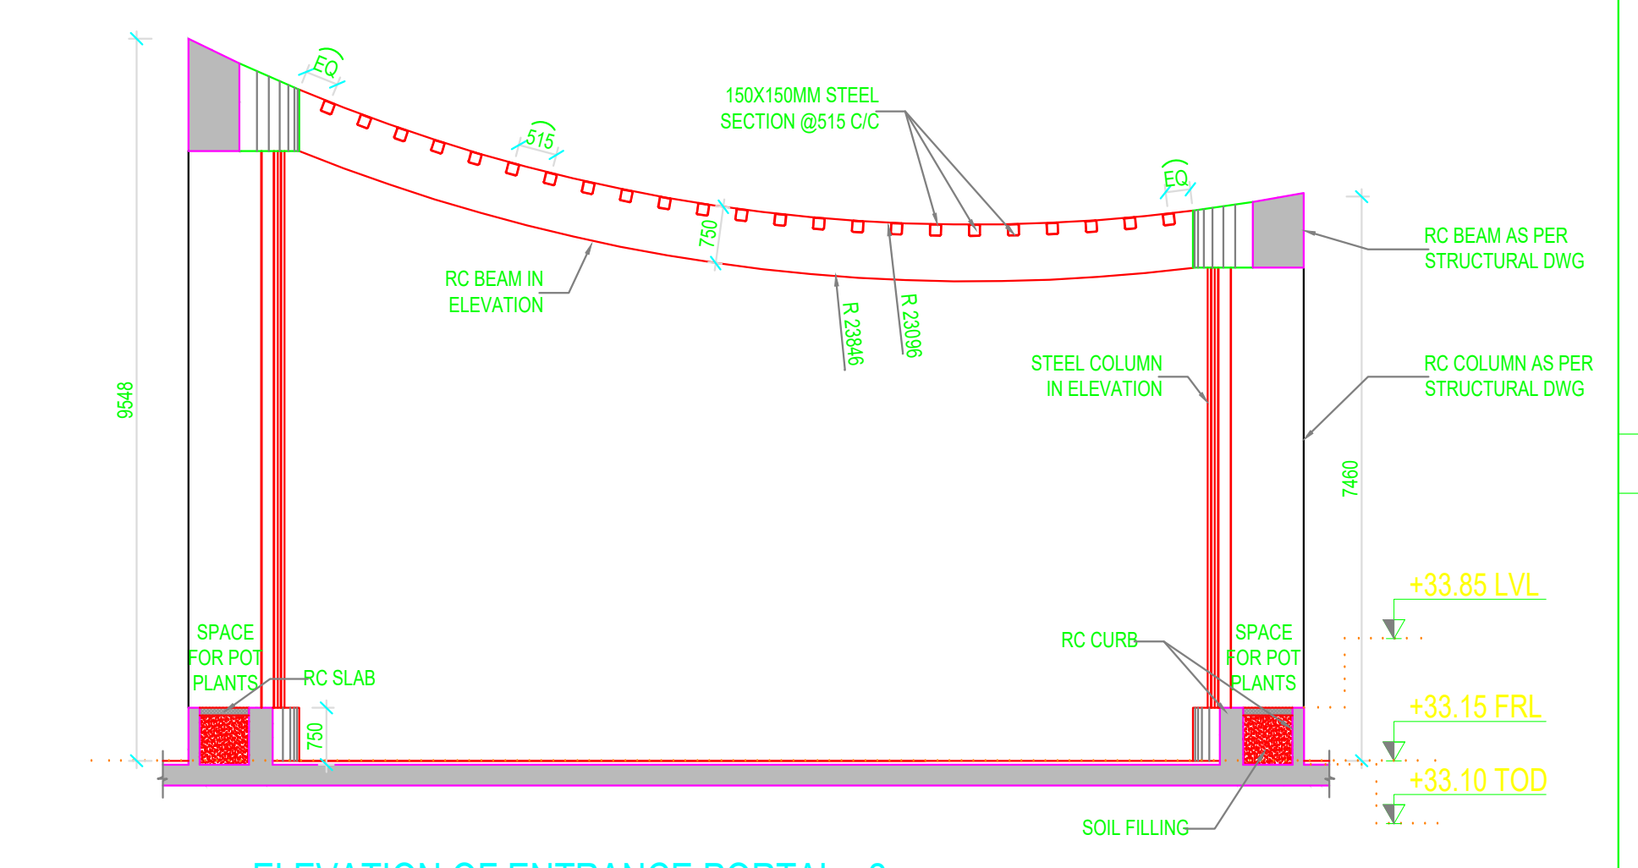
150X150MM STEEL SECTION @515 C/C
EQ
515
RC BEAM AS PER STRUCTURAL DWG
RC BEAM IN ELEVATION
750
R 23846
R 23096
STEEL COLUMN IN ELEVATION
RC COLUMN AS PER STRUCTURAL DWG
9548
7460
SPACE FOR POT PLANTS
RC SLAB
RC CURB
+33.85 LVL
+33.15 FRL
+33.10 TOD
SOIL FILLING

12 ELEVATION OF ENTRANCE PORTAL - 2
1:100

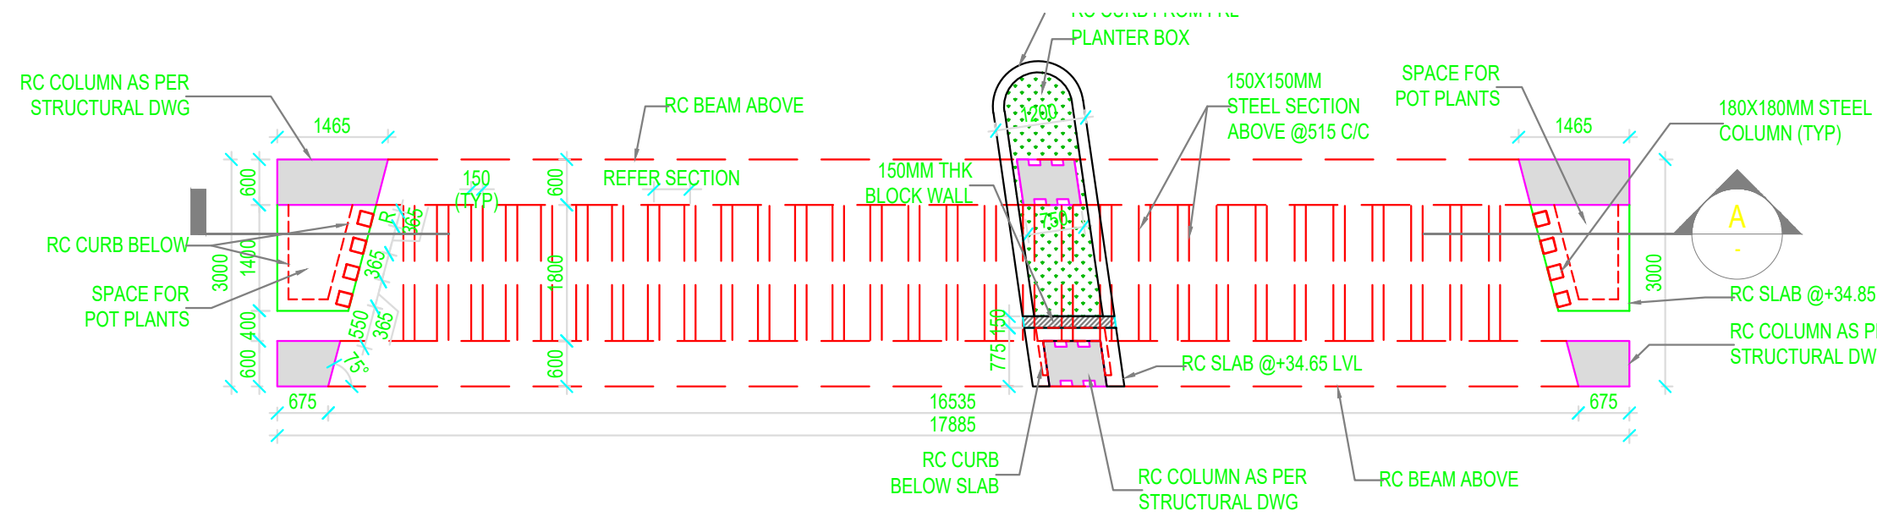
PLANTER BOX
RC COLUMN AS PER STRUCTURAL DWG
RC BEAM ABOVE
150X150MM STEEL SECTION ABOVE @515 C/C
SPACE FOR POT PLANTS
180X180MM STEEL COLUMN (TYP)
1465
150 (TYP)
REFER SECTION
150MM THK BLOCK WALL
RC CURB BELOW
SPACE FOR POT PLANTS
RC SLAB @+34.85 LVL
RC COLUMN AS PER STRUCTURAL DWG
RC SLAB @+34.65 LVL
A
675
16535
17885
RC CURB BELOW SLAB
RC COLUMN AS PER STRUCTURAL DWG
RC BEAM ABOVE

9 PLAN OF ENTRANCE PORTAL - 1
1:100

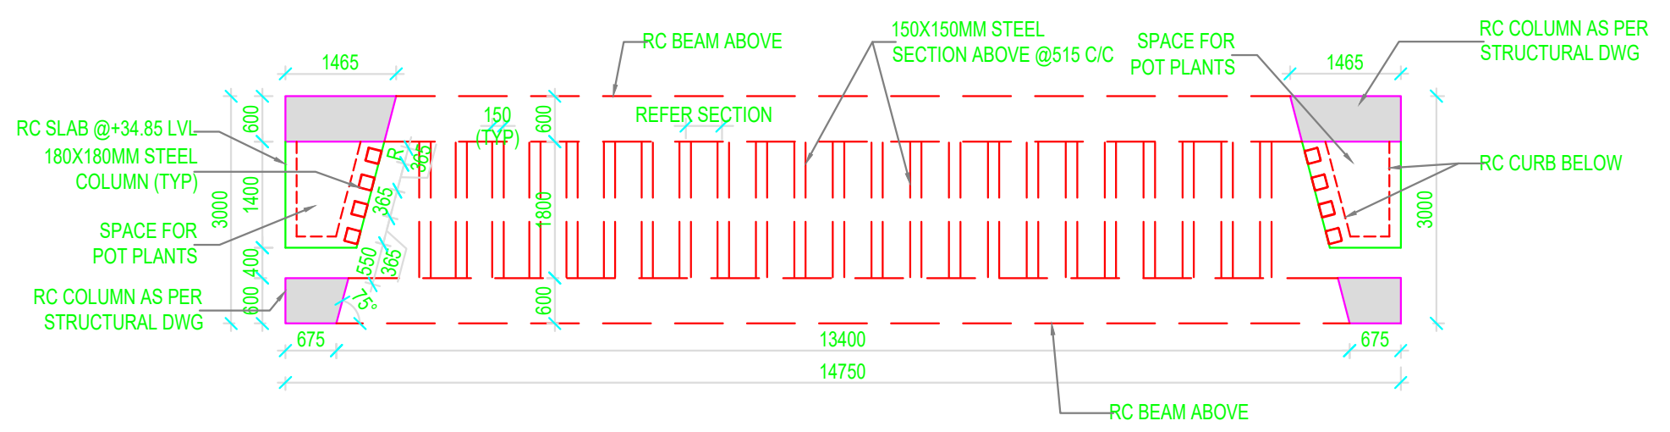
RC BEAM ABOVE
150X150MM STEEL SECTION ABOVE @515 C/C
SPACE FOR POT PLANTS
RC COLUMN AS PER STRUCTURAL DWG
1465
150 (TYP)
REFER SECTION
RC SLAB @+34.85 LVL
180X180MM STEEL COLUMN (TYP)
SPACE FOR POT PLANTS
RC COLUMN AS PER STRUCTURAL DWG
RC CURB BELOW
675
13400
14750
RC BEAM ABOVE

11 PLAN OF ENTRANCE PORTAL - 2
1:100

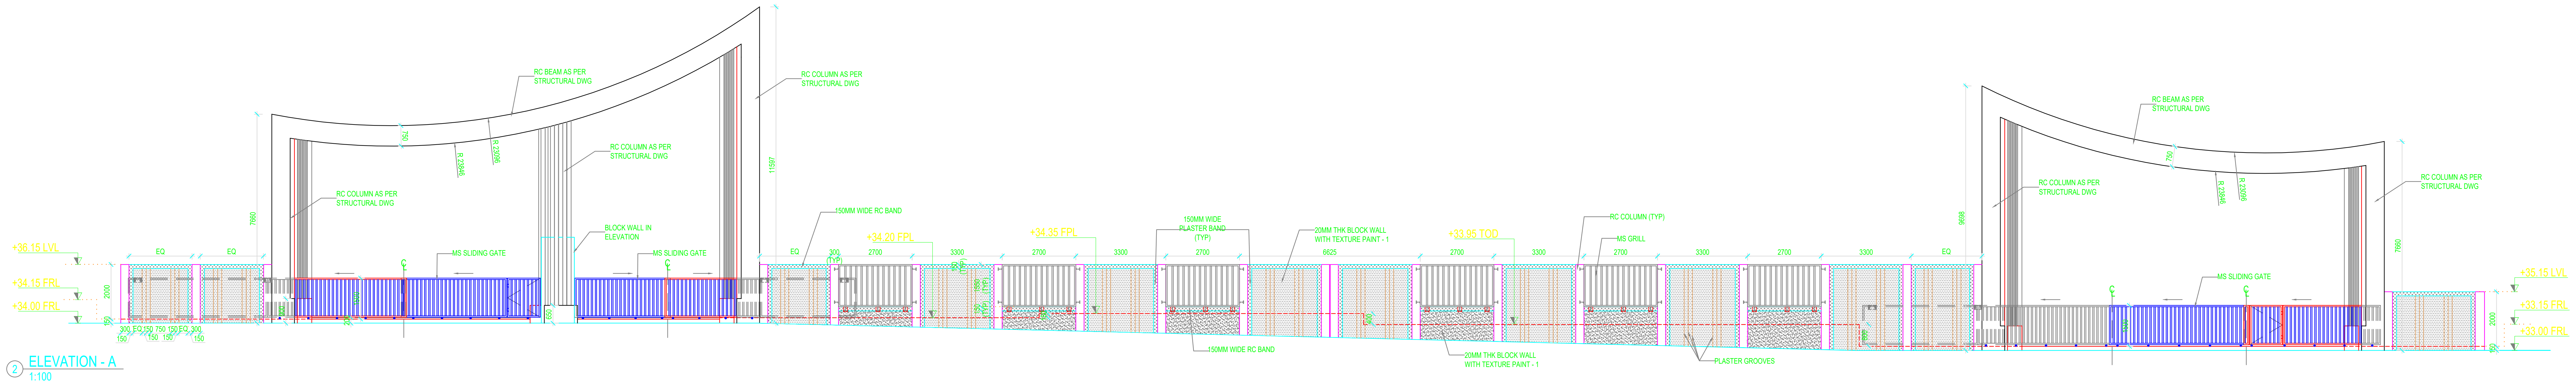
RC BEAM AS PER STRUCTURAL DWG
RC COLUMN AS PER STRUCTURAL DWG
RC COLUMN AS PER STRUCTURAL DWG
RC COLUMN AS PER STRUCTURAL DWG
BLOCK WALL IN ELEVATION
MS SLIDING GATE
MS SLIDING GATE
150MM WIDE RC BAND
+34.20 FRL
+34.35 FRL
150MM WIDE PLASTER BAND (TYP)
20MM THK BLOCK WALL WITH TEXTURE PAINT - 1
+33.95 TOD
RC COLUMN (TYP)
MS GRILL
+36.15 LVL
+34.15 FRL
+34.00 FRL
EQ
2700
3300
6625
MS SLIDING GATE
+35.15 LVL
+33.15 FRL
+33.00 FRL
150MM WIDE RC BAND
20MM THK BLOCK WALL WITH TEXTURE PAINT - 1
PLASTER GROOVES

2 ELEVATION - A
1:100

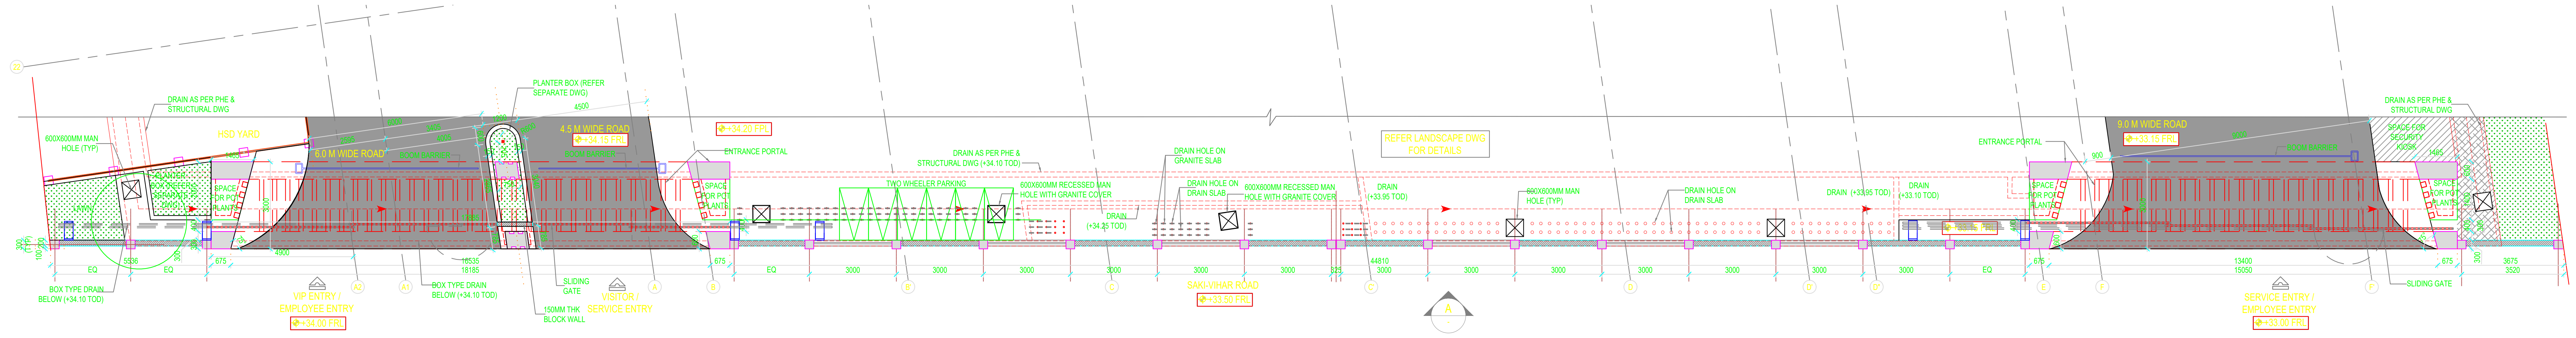
DRAIN AS PER PHE & STRUCTURAL DWG
600X600MM MAN HOLE (TYP)
HSD YARD
PLANTER BOX (REFER SEPARATE DWG)
6.0 M WIDE ROAD
4.5 M WIDE ROAD
ENTRANCE PORTAL
DRAIN AS PER PHE & STRUCTURAL DWG (+34.10 TOD)
TWO WHEELER PARKING
600X600MM RECESSED MAN HOLE WITH GRANITE COVER
DRAIN HOLE ON GRANITE SLAB
DRAIN HOLE ON DRAIN SLAB
REFER LANDSCAPE DWG FOR DETAILS
DRAIN (+33.95 TOD)
600X600MM MAN HOLE (TYP)
DRAIN HOLE ON DRAIN SLAB
DRAIN (+33.95 TOD)
DRAIN (+33.10 TOD)
9.0 M WIDE ROAD
ENTRANCE PORTAL
DRAIN AS PER PHE & STRUCTURAL DWG
SPACE FOR SECURITY KIOSK
BOX TYPE DRAIN BELOW (+34.10 TOD)
VIP ENTRY / EMPLOYEE ENTRY
BOX TYPE DRAIN BELOW (+34.10 TOD)
SLIDING GATE
150MM THK BLOCK WALL
VISITOR / SERVICE ENTRY
SAKI-VIHAR ROAD
SERVICE ENTRY / EMPLOYEE ENTRY
SLIDING GATE
EQ
3000
675
13400
15050
44810
A

1 PLAN - 1
1:100

This drawing is the property of L&T Construction ,B&F-EDRC and must not be passed on to any person or body not authorised by us to receive it nor be copied or otherwise made use either in full or in part by such person or body without our prior permission in writing.

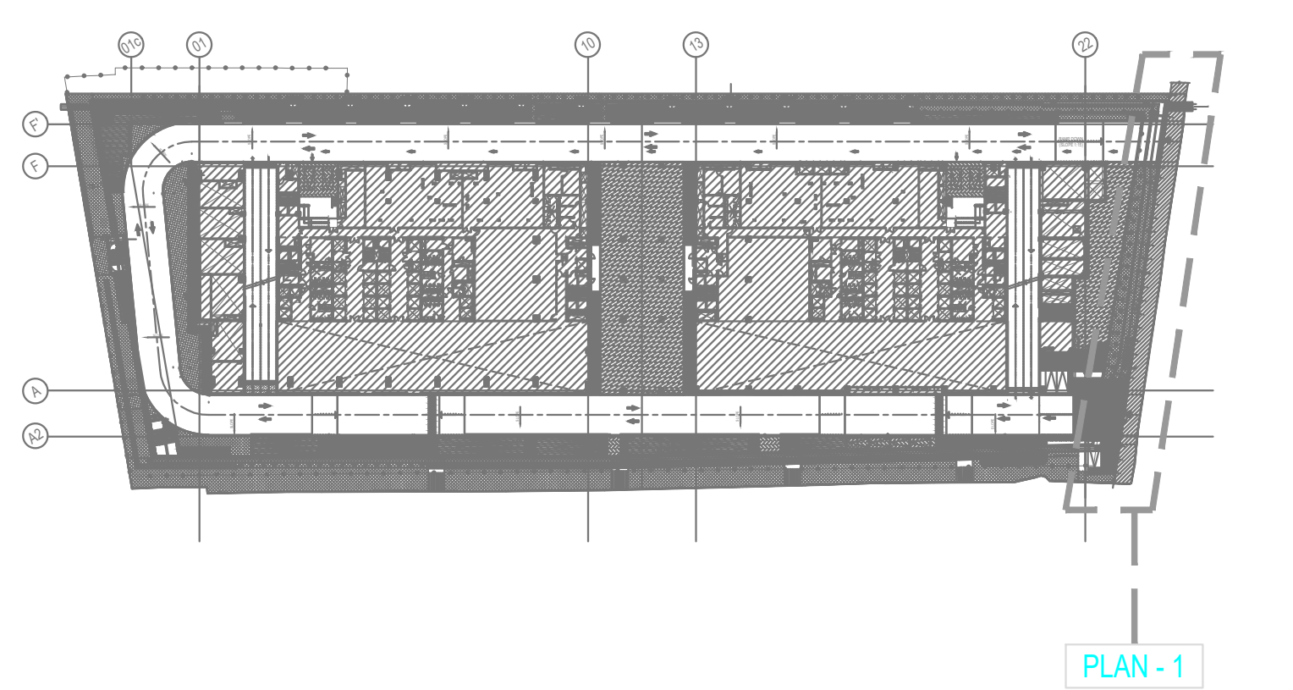

KEY PLAN
(NOT TO SCALE)

WALL INDEX

S.NO	PATTERN	DESCRIPTION
1	▨	200mm THK BLOCK WALL
2	▨ / ▨	R.C.C.
3	▨	DRAIN COVER SLAB
4	▨	LAWN / PLANTER BOX

ABBREVIATIONS

FRL : FINISHED ROAD LEVEL
FPL : FINISHED PAVEMENT LEVEL
FFL : FINISHED FLOOR LEVEL
TSL : TOP OF SOIL LEVEL
TOK : TOP OF KERB LEVEL
TOD : TOP OF DRAIN LEVEL
TOC : TOP OF CONCRETE
LVL : LEVEL

LEGEND

PATTERN	DESCRIPTION
▨	RC / PLASTER BAND
🟥	TEXTURE PAINT - TYPE-1
▨	TEXTURE PAINT - TYPE-2

COMPOUND WALL MEASUREMENTS AND LEVELS SHALL BE CONFIRMED AS PER SITE CONDITION BEFORE EXECUTION

INDICATES DIMENSIONS AS PER VENDOR REQUIREMENT

PRIOR TO INSTALLATION OF SLIDING / WICKET GATE VENDOR TO SUBMIT SHOP DRAWING FOR THE SAME AND OBTAIN APPROVAL FROM EDRC.

NOTES

01. ALL DIMENSIONS ARE IN MILLIMETER & LEVELS IN METER.
02. THE FINISHED GROUND FLOOR LEVEL HAS BEEN CONSIDERED AS ±0.000 LVL CORRESPONDS TO +34.20 MSL AT SITE
03. FOR SITE SETTING OUT PLAN REFER DWG NO.O23023-A-OB-00-WD-0001
04. FOR MASTER PLAN REFER DWG NO.O23023-A-OB-00-WD-0002
05.THIS DRAWING SHALL BE READ IN CONJUNCTION WITH ALL RELEVANT ARCHITECTURAL STRUCTURAL AND OTHER RELATED SERVICE DRAWINGS
06.ALL DIMENSIONS SHALL BE VERIFIED ON SITE PRIOR TO START OF WORK ANY DISCREPANCY SHALL BE BROUGHT TO THE NOTICE OF THE EDRC ARCHITECT.
07. THIS DRAWING IS TO BE READ AND NOT TO BE SCALED.

REV.NO.	DESCRIPTION	DESIGNED		DRAWN		CHECKED		APPROVED	
0	ISSUED FOR CONSTRUCTION	BSC	27.02.2025	PJ	28.02.2025	ECM	01.03.2025	JVP	03.03.2025

REVISIONS

CHECKED BY	SIGN	DATE	CHECKED BY	SIGN	DATE	CHECKED BY	SIGN	DATE
ARCHITECTURE			HVAC			GIS		
CIVIL & STRUCTURAL			FPS			GEOTECH.		
ELECTRICAL			PIPING					
ELV SYSTEM			PHE					

CLIENT : L&T Realty L&T Realty

O23023,O23023-A-C

L&T Construction
Buildings & Factories

PROJECT: L&T Commercial Tower (LTCT) at Powai, Mumbai

PRINCIPAL CONSULTANT : Engineering Design and Research Center (EDRC), L&T Construction - Buildings & Factories

MEP CONSULTANT : M/s. CHETTIAR CONSULTING ENGINEERS.
SHRI SAI CORPORATE PARK, 304, THIRD FLOOR, NEW LINK ROAD
MAHAKALI TEMPLE ROAD, NEAR VASANT GALAXY &
LAXMI NAGAR, GOREGAON (WEST), MUMBAI-400 062.

SUPPLIER/ CONTRACTOR : Larsen & Toubro Limited, Construction, Buildings & Factories

JOB No : O23023

	NAME	SIGN	DATE
DSGN	BSC		27.02.2025
DRWN	PJ		28.02.2025
CHKD	ECM		01.03.2025
APPD	JVP		03.03.2025

TITLE:
OFFICE BUILDING
COMPOUND WALL DETAILS

SECTION/ ELEVATION MARKING
DRAWING NUMBER

SCALE
AS INDICATED

DRAWING No. O23023-A-OB-00-WD-0000

PROJECTION
FIRST ANGLE

SIZE A0
REV 0

RELEASED FOR ☐ PRELIMINARY ☐ TENDER ☐ INFORMATION ☐ APPROVAL ☑ CONSTRUCTION