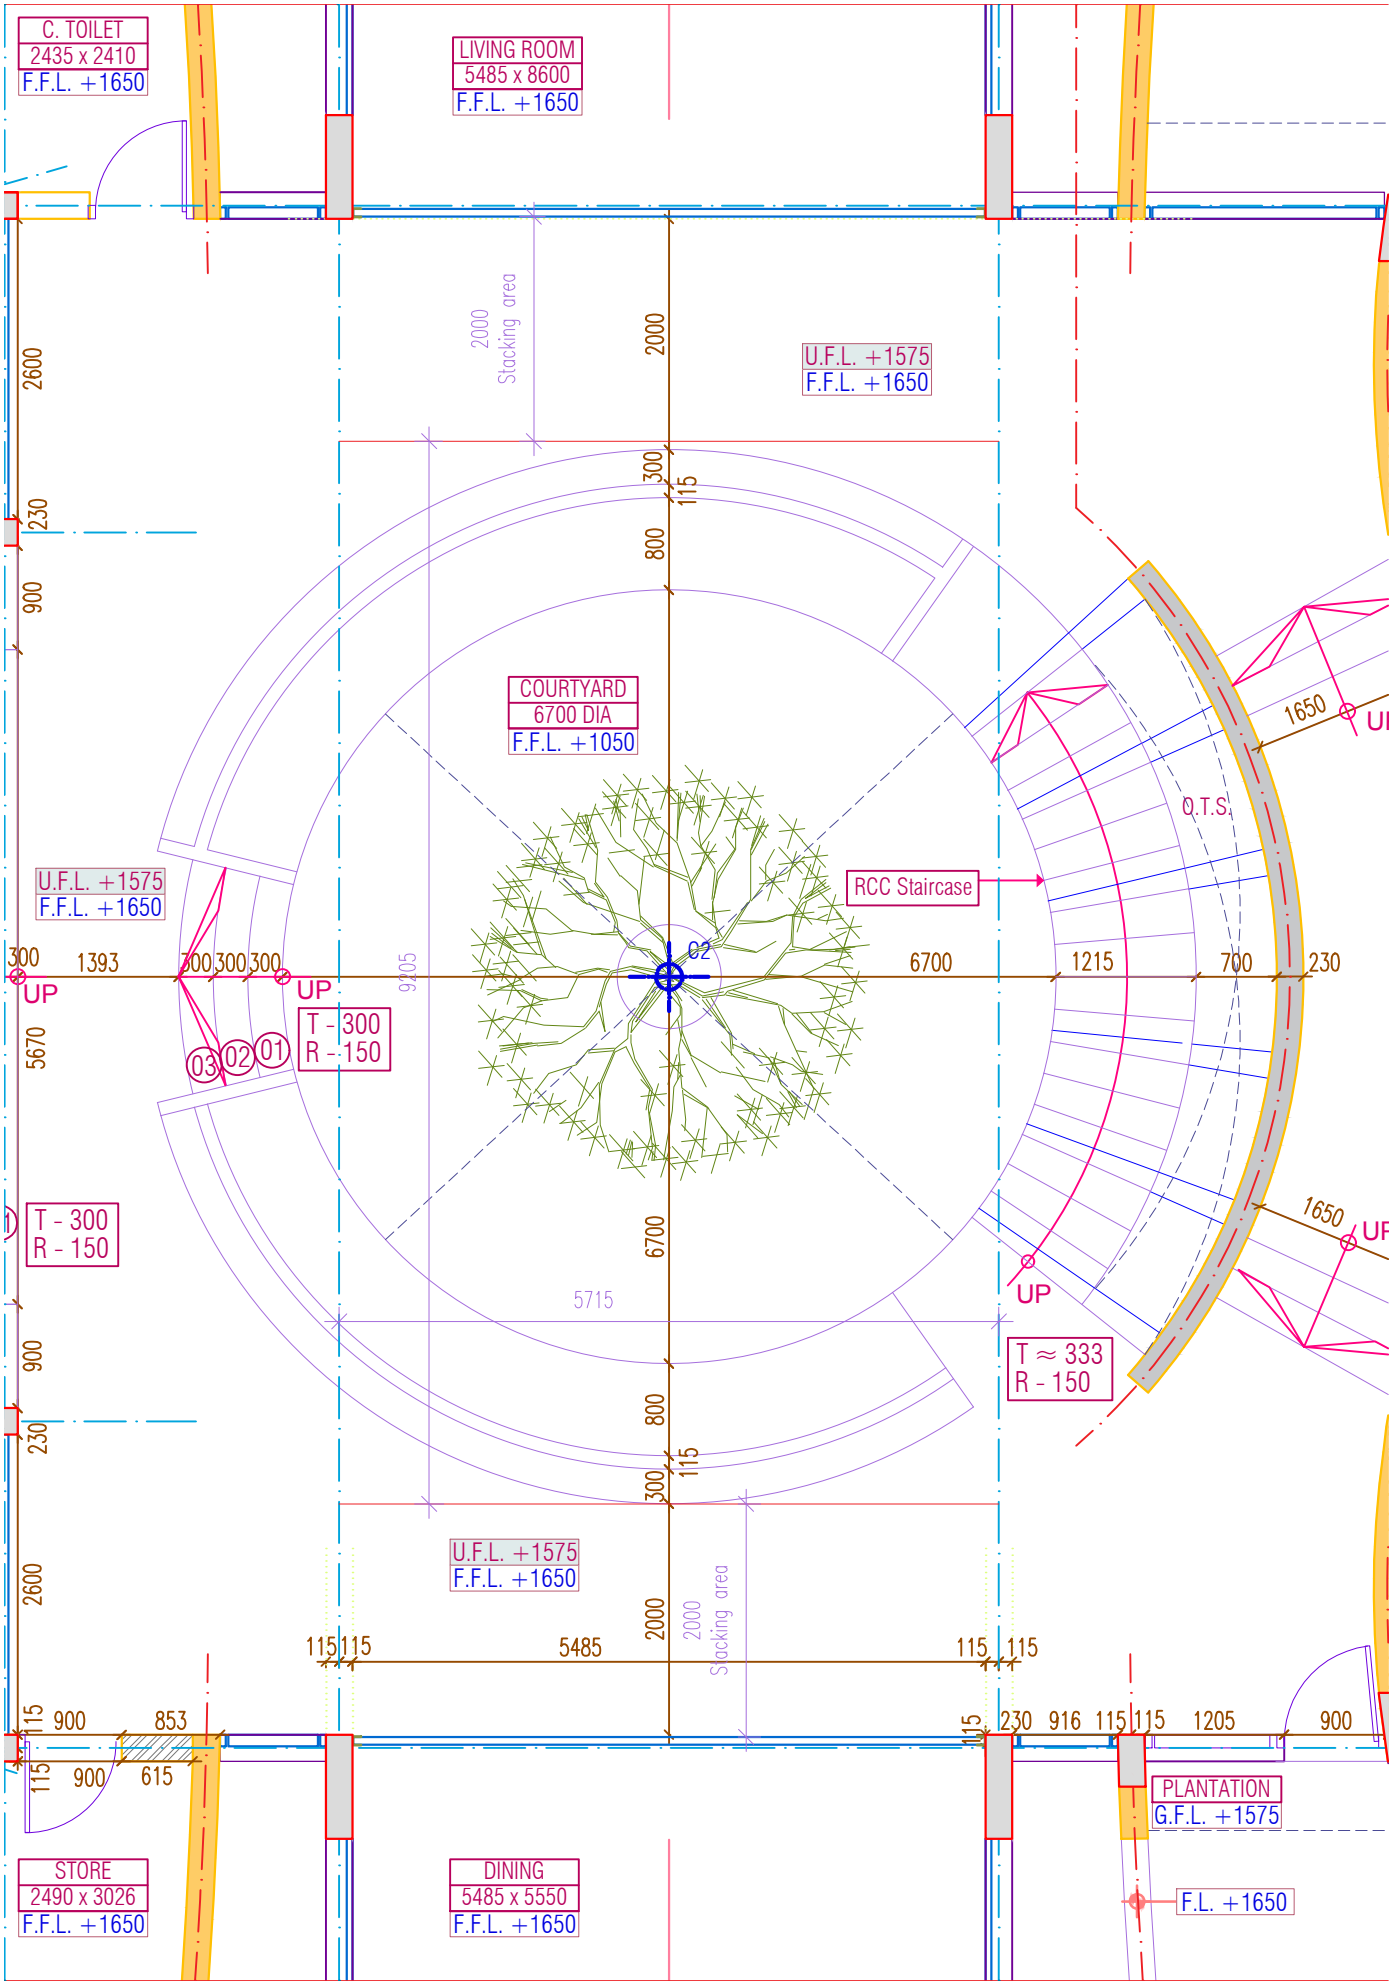

C. TOILET
2435 x 2410
F.F.L. +1650
LIVING ROOM
5485 x 8600
F.F.L. +1650
U.F.L. +1575
F.F.L. +1650
COURTYARD
6700 DIA
F.F.L. +1050
RCC Staircase
O.T.S.
C2
UP
T - 300
R - 150
T ≈ 333
R - 150
STORE
2490 x 3026
F.F.L. +1650
DINING
5485 x 5550
F.F.L. +1650
PLANTATION
G.F.L. +1575
F.L. +1650
Stacking area
2000
5715
5485
6700
9205