

DWG.NO: SALT_1714_STR_01_R1

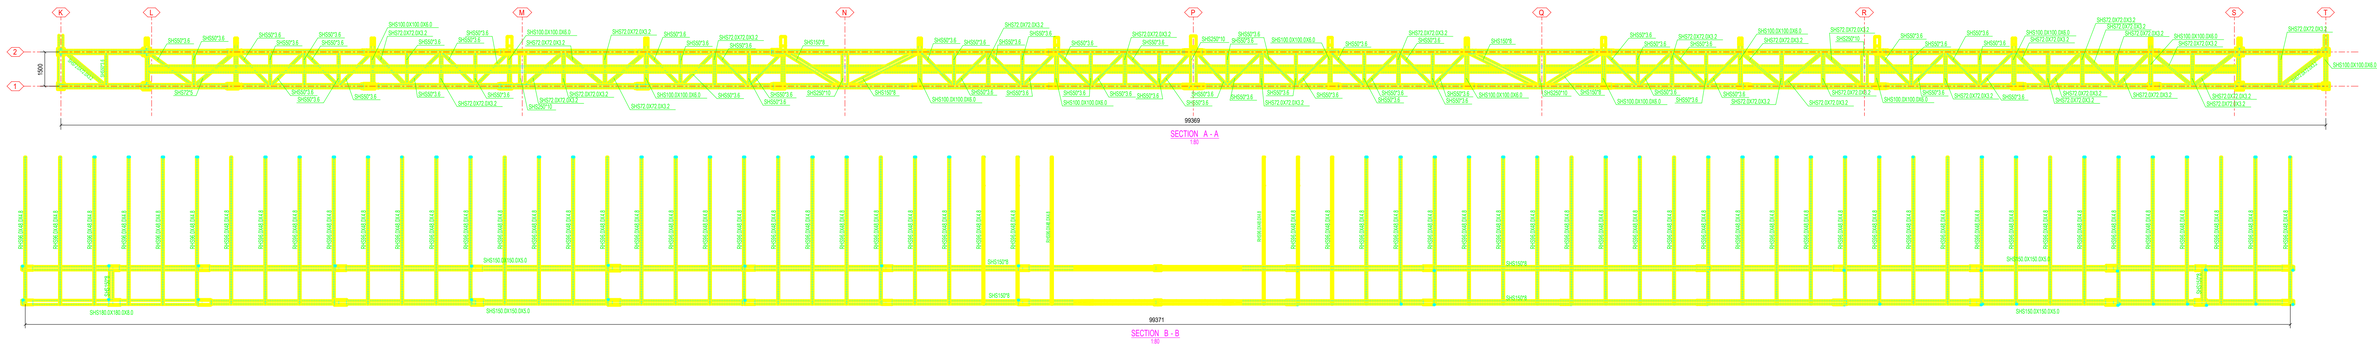

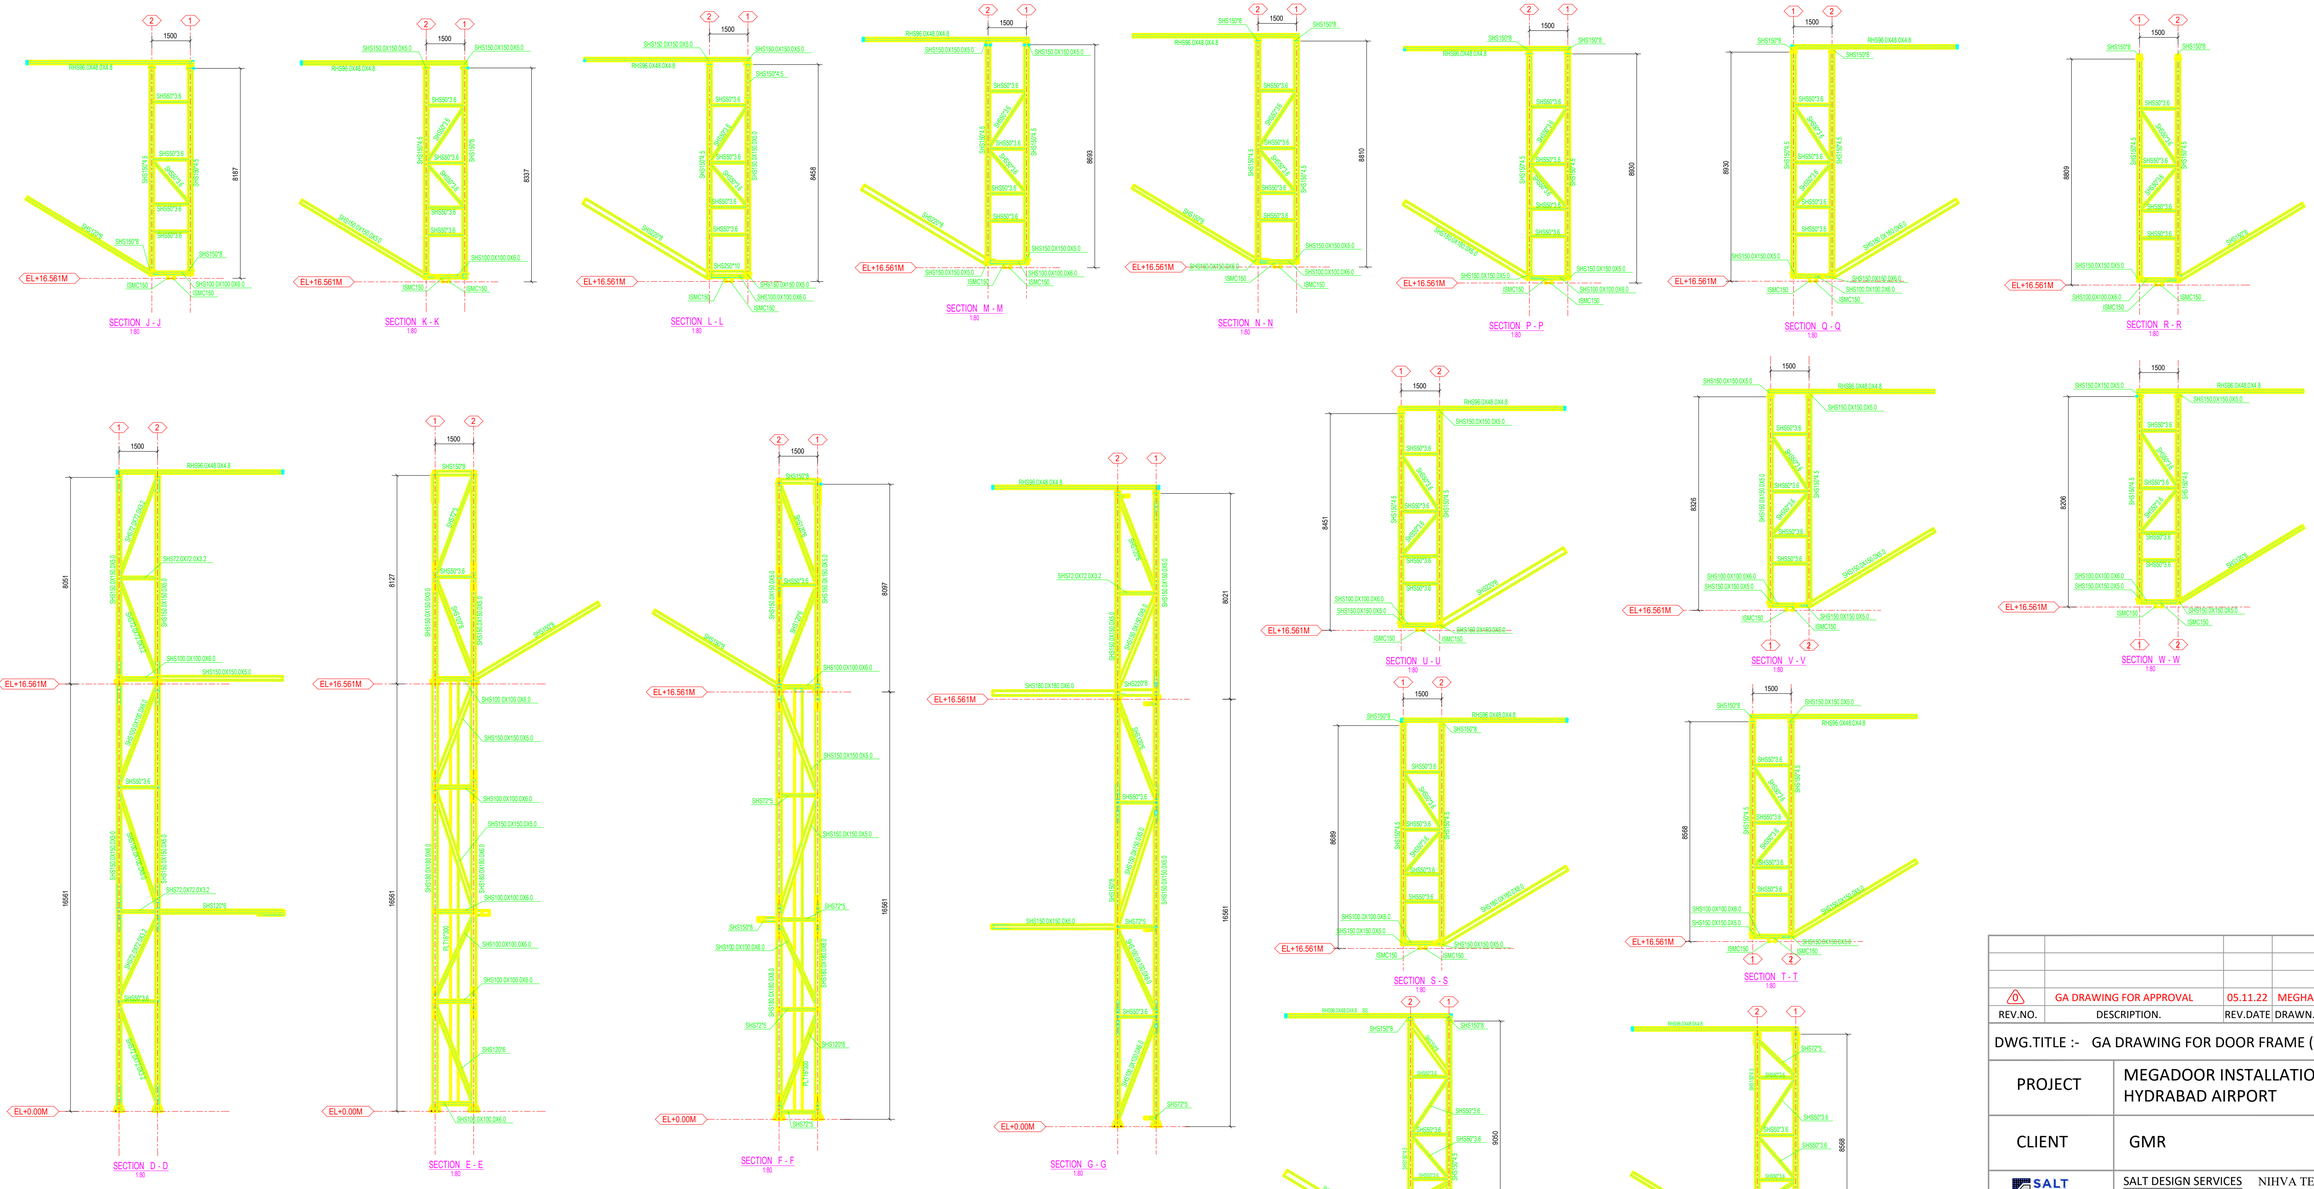

0	GA DRAWING FOR APPROVAL	05.11.22	MEGHA	HAB	HAB
REV.NO.	DESCRIPTION.	REV.DATE	DRAWN.	CHKD.	APPD.

DWG.TITLE :- GA DRAWING FOR DOOR FRAME (99M)

PROJECT	MEGADOOR INSTALLATION AT HYDRABAD AIRPORT
CLIENT	GMR
SALT DESIGN SERVICES / NIHVA TECHNOLOGIES PVT. LTD.	SALT DESIGN SERVICES — NIHVA TECHNOLOGIES PVT. LTD. PUNE Tel : 020 66304033 Email:- info@nihva.com Website:- www.nihva.com

DRAWN :RRK	CHECKED : HAB	SCALE: 1:100
APPROVED : HAB	JOB CODE. : 1729	DATE: 05.11.2022
DWG.NO: SALT_1729_GA_01_R0	(SH-2OF2)	REV. - R0 SIZE. - A0

A1 (841 x 594)