

PRODUCED BY AN AUTODESK EDUCATIONAL PRODUCT

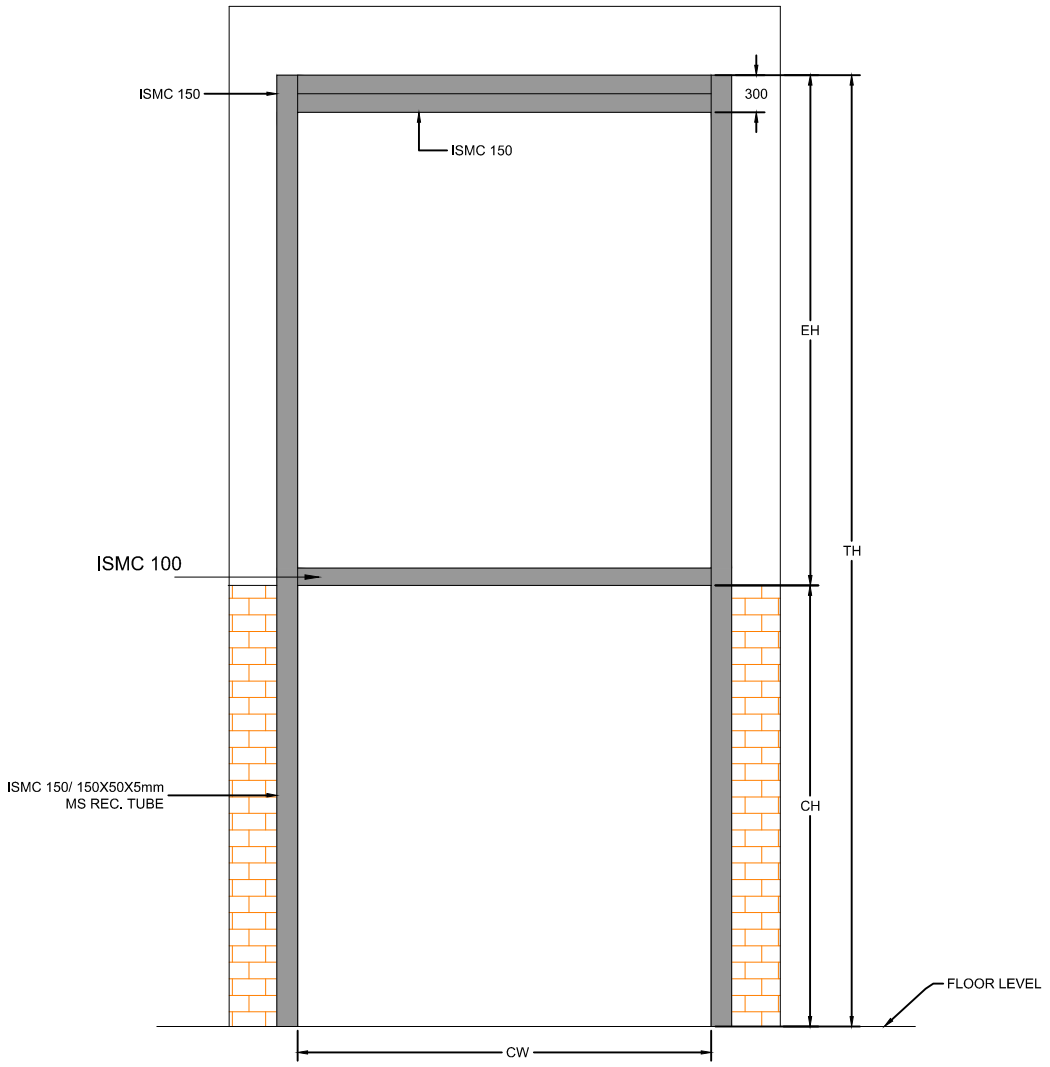


INSIDE ELEVATION

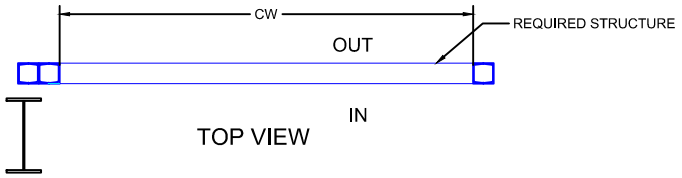


TOP VIEW

NOTE- STRUCTURE FOR SECTIONAL DOOR WILL BE IN CLIENTS SCOPE.

| SR NO | CLEAR WIDTH | CLEAR HEIGHT | QTY | TH | EH | LOCATION (w.r.t PEB A01-R1) | MOTOR POSITION |
|---|---|---|---|---|---|---|---|
| 12 | 5350mm | 6500mm | 1 | 13350 | 6850 | 19-B1 & B2 | RIGHT |

This drawing & design is the property of NIHVA TECHNOLOGIES. Not to be sold or copied to any other concern.

TITLE

STRUCTURE FOR SECTIONAL DOOR

CLIENT APPROVAL

ALL DIMENSION ARE IN mm

NIHVA TECHNOLOGIES PVT. LTD.

NIHVA TECHNOLOGIES PVT. LTD. PUNE
Tel : 020 66304033
Email:- info@nihva.com
Website:- www.nihva.com

| | SIGN | DATE |
|---|---|---|
| DRAWN | OMKAR | 12/05/17 |
| CHECK | SAGAR P. | 12/05/17 |
| REV. | | |
| APPRD. | | |
| MFG | | |
| Ref. No. | | |

CLIENT - TATA PROJECTS

PROJECT - MADHEPURA ELECTRIC LOCOMOTIVE PVT. LTD.

SITE - MADHEPURA,BIHAR

DWG. NO. - NIHVA/17-18/0075

SCALE: NTS | WT: | SHEET: 01 OF 01

If any queries contact : projects@nihva.com

PRODUCED BY AN AUTODESK EDUCATIONAL PRODUCT