


PRODUCED BY AN AUTODESK EDUCATIONAL PRODUCT

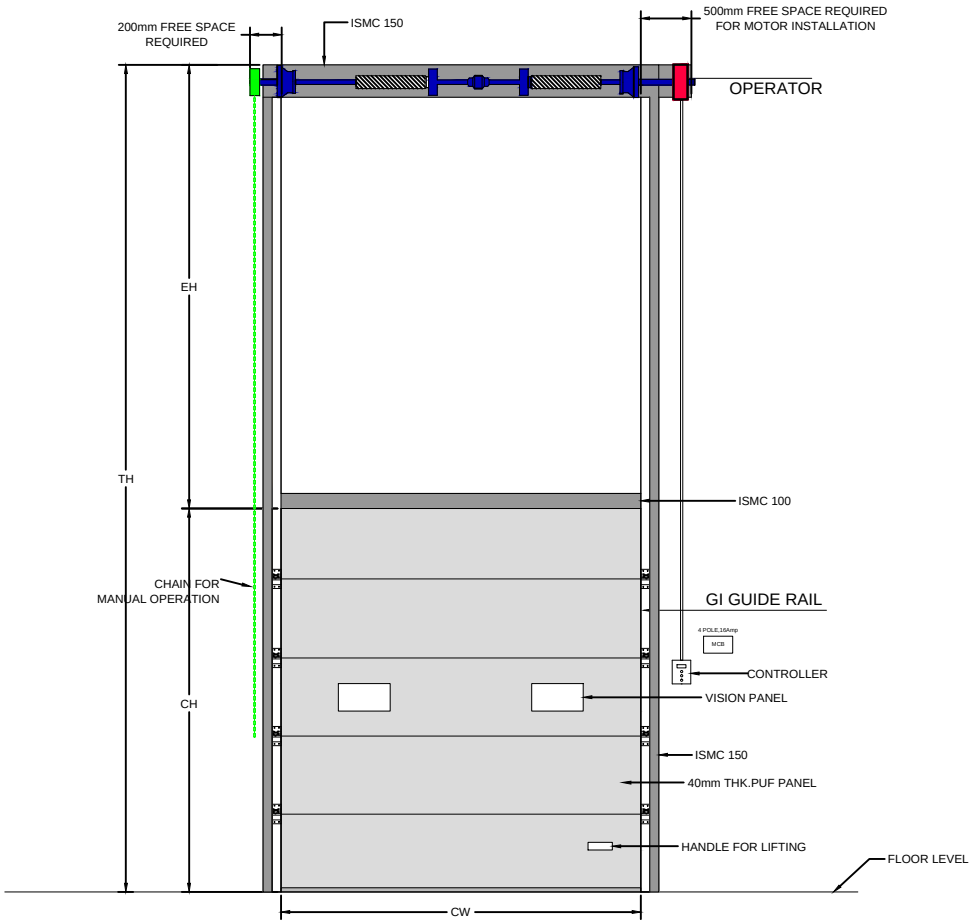


INSIDE VIEW

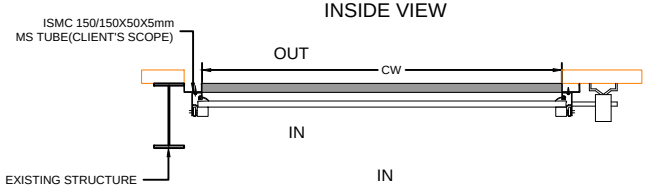

TOP VIEW

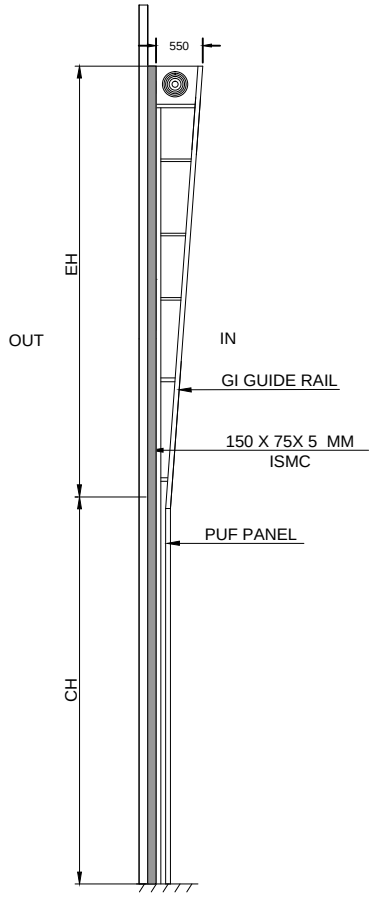

CROSS VIEW

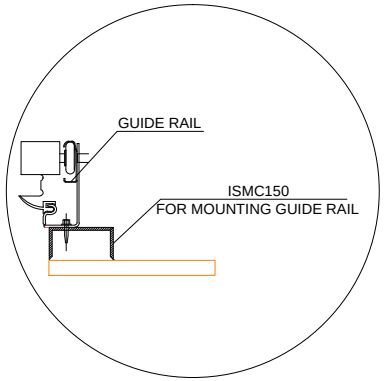

SR NO	CLEAR WIDTH	CLEAR HEIGHT	QTY	TH	EH	LOCATION (w.r.t PDF TPL-3452-X9100-EC-AC-6200_R1)	MOTOR POSITION
1	4000mm	6000mm	1	12300	6300	7-B	RIGHT SIDE
2	4000mm	6000mm	1	12300	6300	5-B	
3	4000mm	6000mm	1	12300	6300	8-Q	

This drawing & design is the property of NIHVA TECHNOLOGIES. Not to be sold or copied to any other concern.

TITLE: SECTIONAL DOOR

NIHVA TECHNOLOGIES PVT. LTD. PUNE
Tel : 020 66304033
Email:- info@nihva.com
Website:- www.nihva.com

	SIGN	DATE
DRAWN	OMKAR	27/04/17
CHECK	SAGAR P.	27/04/17
REV.		
APPROVAL		

If any queries contact : projects@nihva.com

ALL DIMENSION ARE IN mm

CLIENT - TATA PROJECTS

PROJECT - MADHEPURA ELECTRIC LOCOMOTIVE PVT. LTD.

SITE - MADHEPURA,BIHAR

DWG. NO. : NIHVA/17-18/0035

SCALE: NTS | WT: | SHEET: 01 OF 01

PRODUCED BY AN AUTODESK EDUCATIONAL PRODUCT