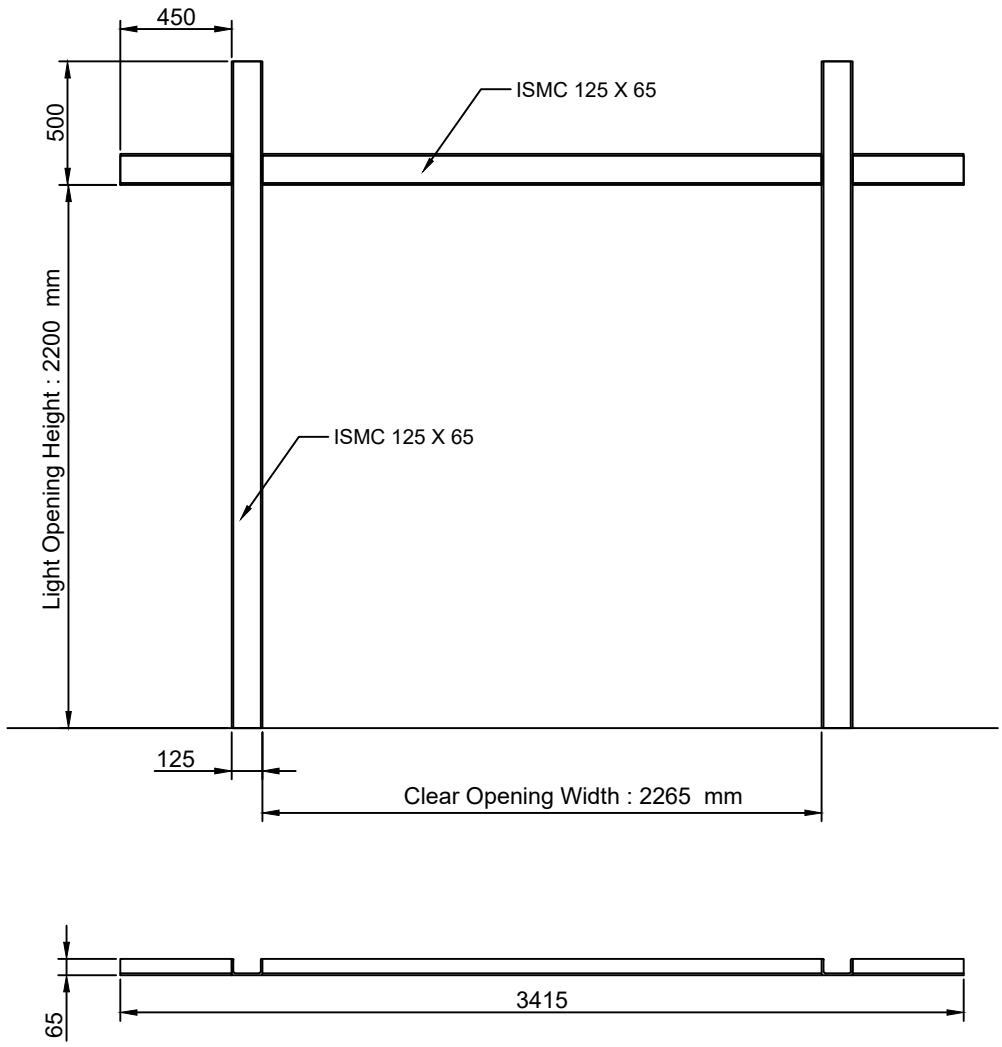


CLEAR WIDTH	CLEAR HEIGHT	QTY
2265 mm	2200mm	3 NOS

Note:-

1.All dimension are in MM

2.All civil work is in client scope

3.Given GA drawing is only for the client unerstanding purpose

4.If strucuture required, will be in client scope(ISMC 125X65)

Rev No.	Revision	Date	Revised By

This drawing & design is the property of NIHVA TECHNOLOGIES. Not to be sold or copied to any other concern.

TITLE:-MACHINE PROTECTION DOOR STRUCTURE

	NAME	DATE	SIGN
DRAWN	NIRMALA	20/10/2023	
CHECK	A.K.	20/10/2023	
APPRD.	V.T.	20/10/2023	

If any queries contact - design@nihva.com

ALL DIMENSION ARE IN mm

NIHVA TECHNOLOGIES PVT. LTD.

NIHVA TECHNOLOGIES PVT. LTD. PUNE
Tel : 020 66304033
Email:- info@nihva.com
Website:- www.nihva.com

CLIENT - HIROTEC

LOCATION -

PRODUCT - Machine Protection Door

DWG NO:-NIHVA/23-24/CLT/083 | REV- 0

SCALE: NTS | SCALE:-- 1:1 | SHEET: 01 OF 01