


SLIDING DIRECTION

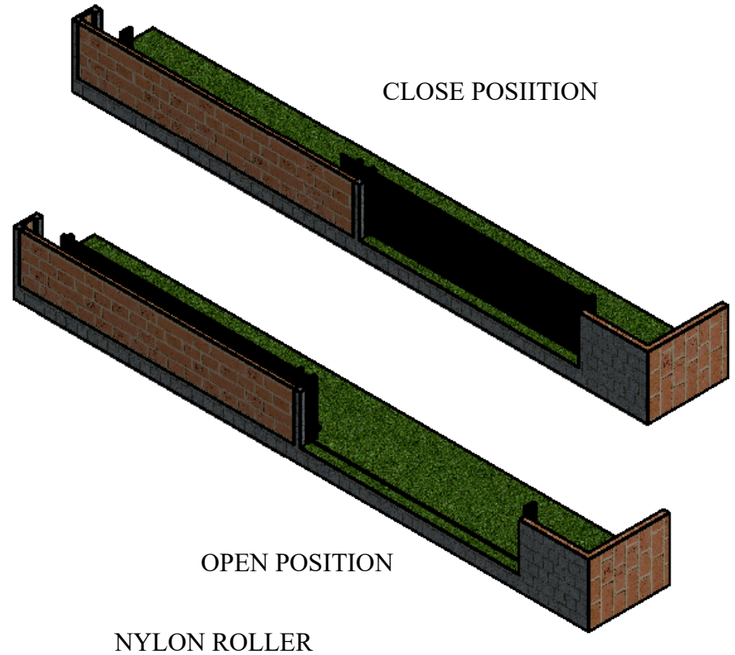


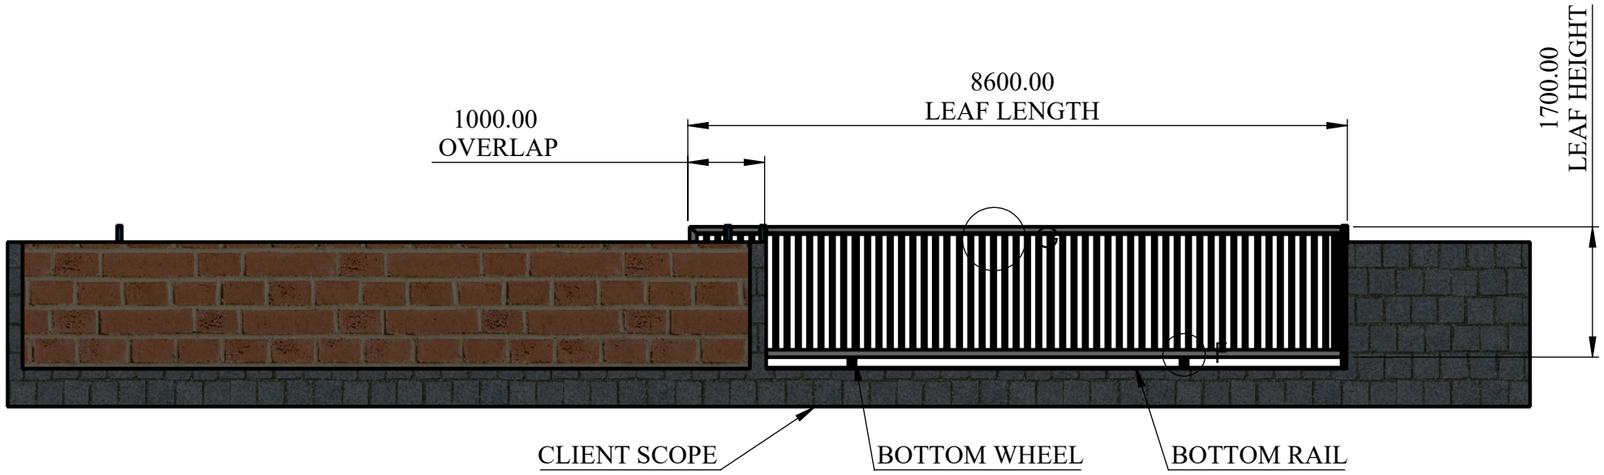

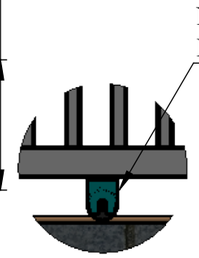




DETAIL F
SCALE 1 : 20

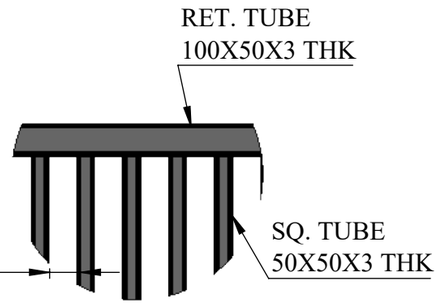


DETAIL G
SCALE 1 : 20

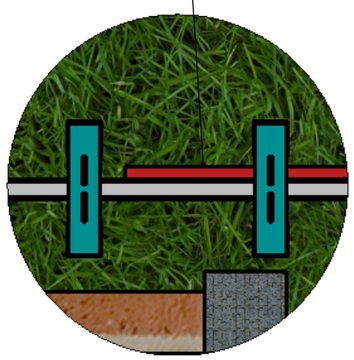


DETAIL A
SCALE 1 : 15

POST 1 NYLON
BEARING ASM

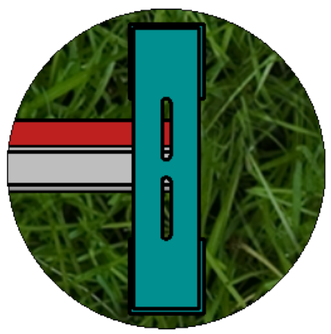

DETAIL B
SCALE 1 : 7


POST 2 NYLON
BEARING ASM

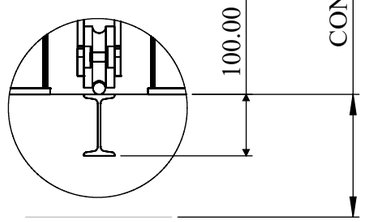



DETAIL E
SCALE 1 : 10


SLIDING GATE
8600L X 1700 H
(OVELAPPING +MOTOR MOUNTING
DISTANCE CONSIDER)
PARKING AREA IS 8.6M

TITLE - GATE				NIHVA TECHNOLOGIES PVT.LTD.PUNE
DWG NO - NTPL			QTY - 1	Website - www.nihva.com
	NAME	SIGNATURE	DATE	PROJECT NO - NTPL
DRAWN	V.B.		31-05-25	PRODUCT - SLIDING GATE
CHK'D	S.W.		31-05-25	SITE LOCATION - LUCKNOW
APPV'D	V.T.		31-05-25	
if any queries contact - supportautomation@nihva.com				REVISION -
ALL DIMENSION ARE IN mm			A3	SCALE - SHEET 1 OF 2

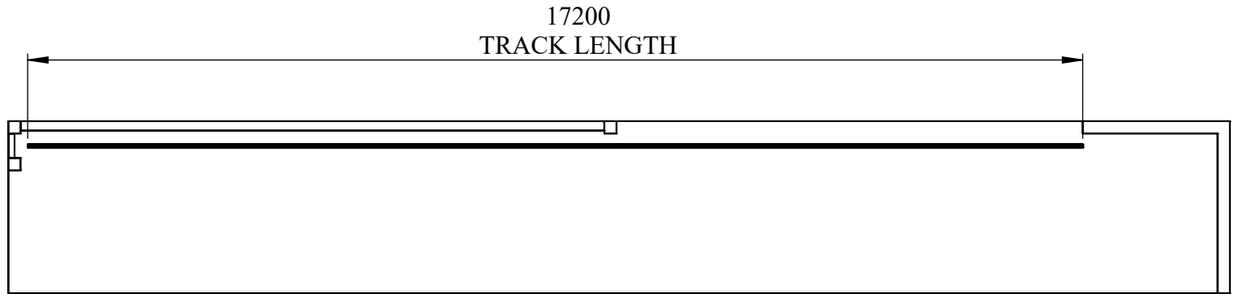

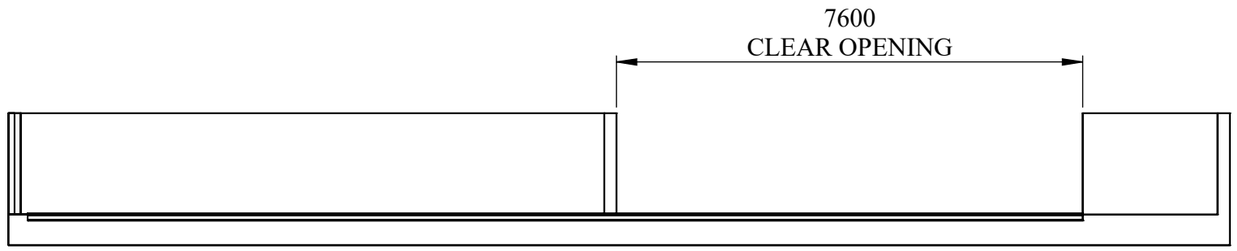

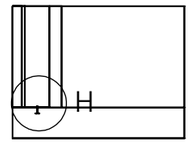

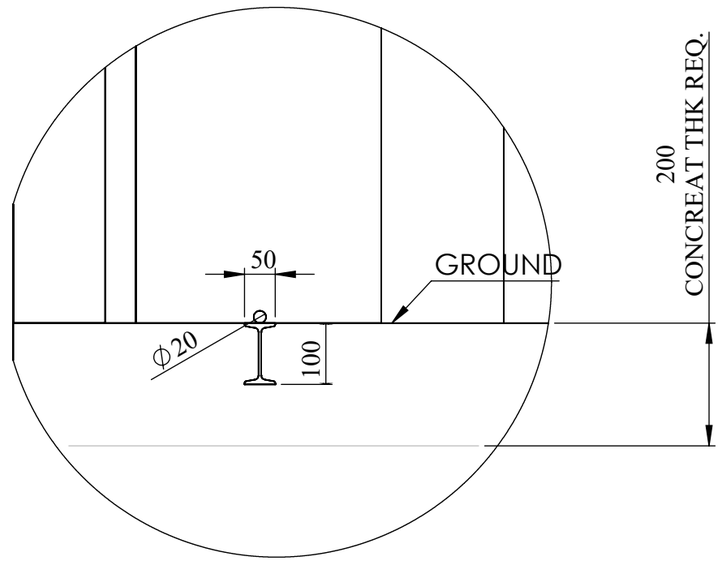

DETAIL H
SCALE 1 : 10

SLIDING GATE
PARKING AREA IS 8.6M

TITLE - GATE				NIHVA TECHNOLOGIES PVT.LTD.PUNE
DWG NO - NTPL			QTY - 1	Website - www.nihva.com
	NAME	SIGNATURE	DATE	PROJECT NO - NTPL
DRAWN	V.B.		31-05-25	PRODUCT - SLIDING GATE
CHK'D	S.W.		31-05-25	SITE LOCATION - LUCKNOW
APPV'D	V.T.		31-05-25	
if any queries contact - supportautomation@nihva.com				REVISION -
ALL DIMENSION ARE IN mm			A3	SCALE - SHEET 2 OF 2