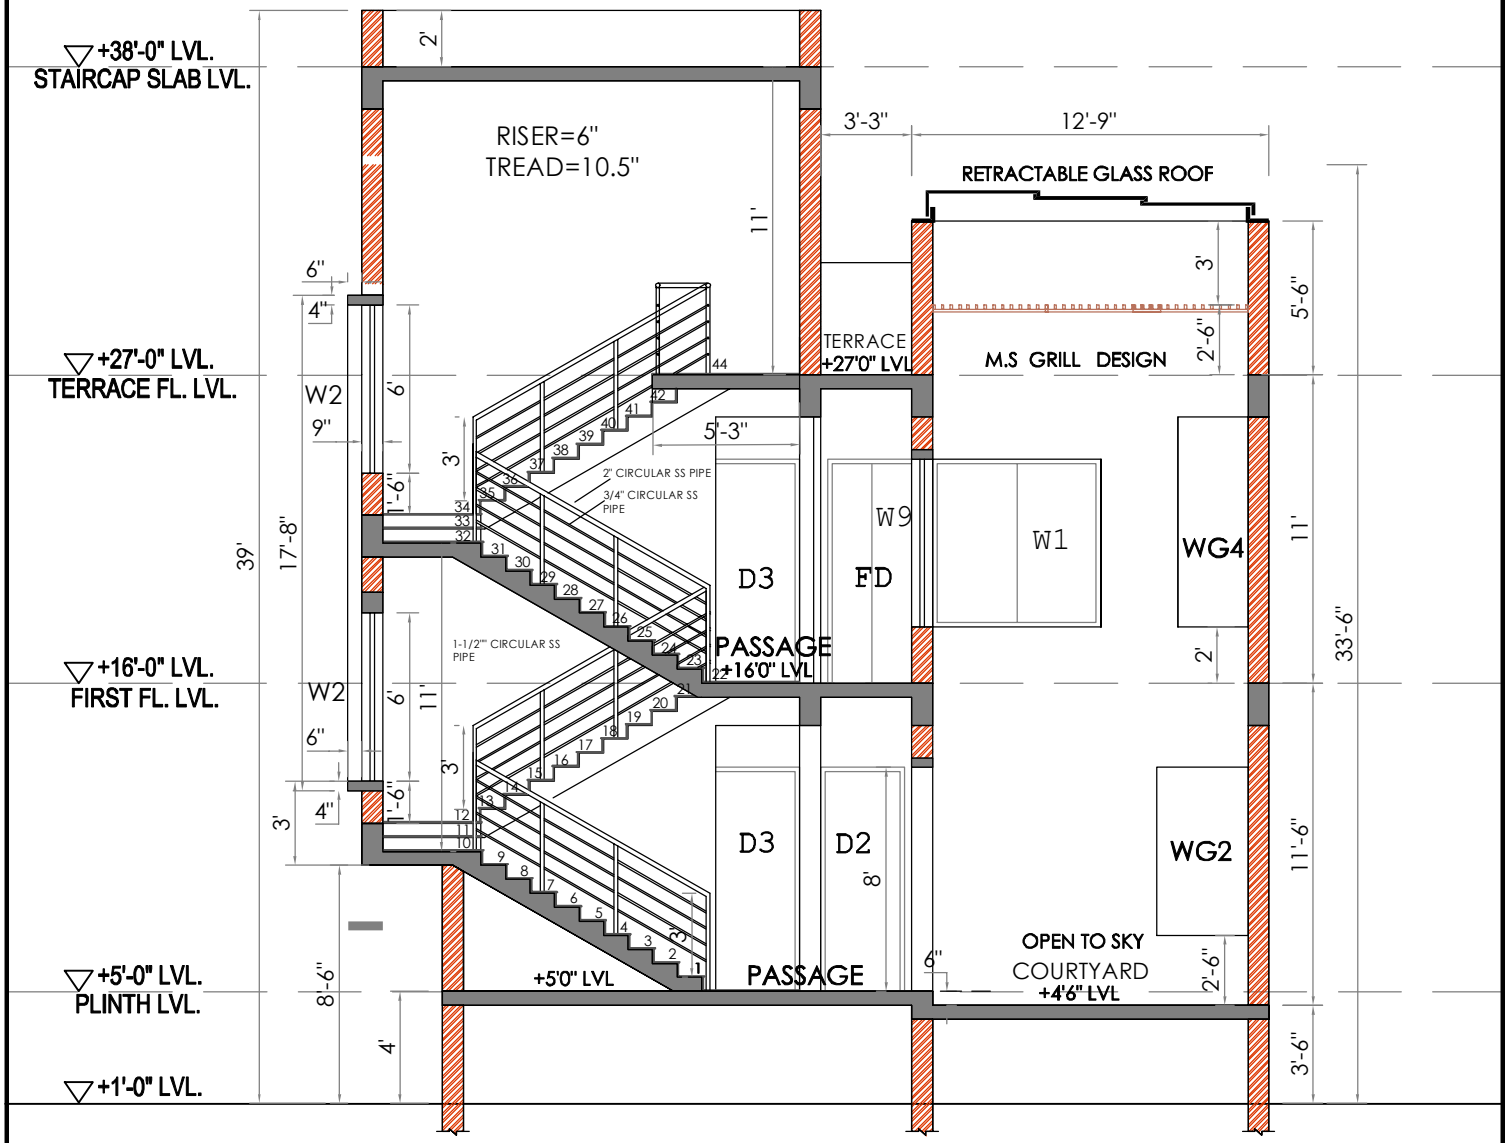


SECTION A-A'

SECTION A-A' WORKING DWG. NO. - 9		M V ASSOCIATES ARCHITECTS, CIVIL ENGINEERS & CONSULTANTS 13,GAJANAN NAGARI,GORAKHPUR,PIRWADI, SATARA - 415003. CELL: +91-9422039623,9822039823 E-mail : mvassociatessat@gmail.com
PROPOSED BUNGALOW AT-MAYANI, DIST.-SATARA FOR DR. DESHMUKH	SCALE:1"=6'0" DATE- 02-03-2023	