
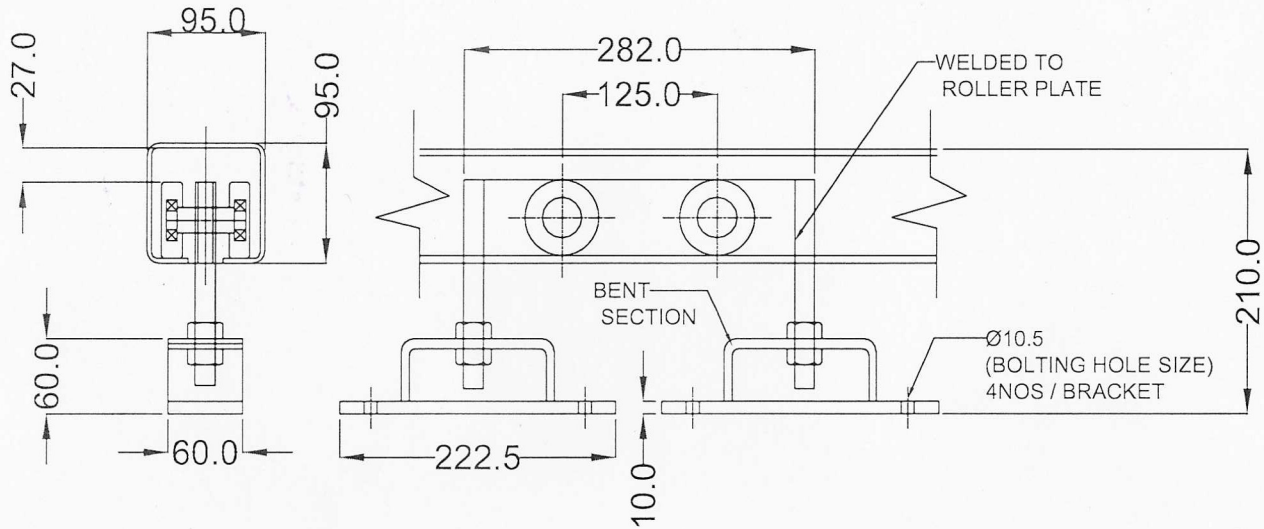


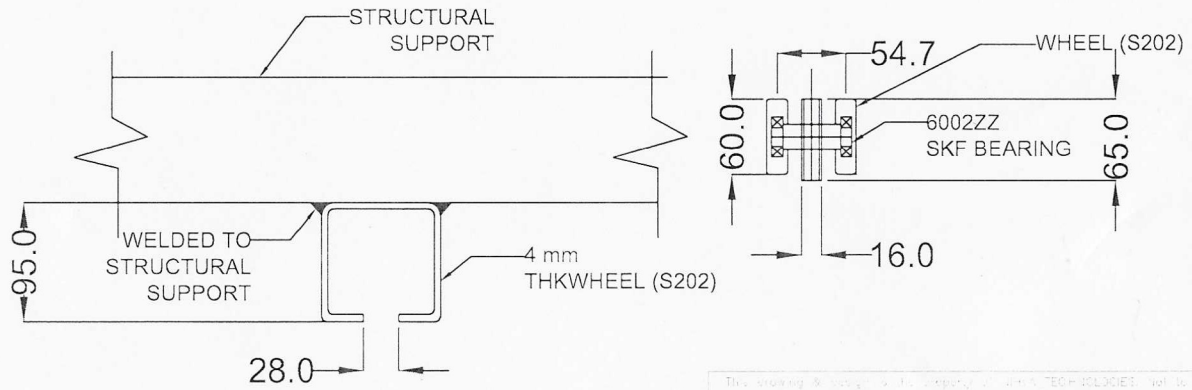

Approved
02-05-2022

NOTE:
END STOPPERS AT BOTH SIDES FOR EACH TRACK SHOULD BE PROVIDED WITH TRACK

TITLE : TOP TRACK AND BRACKET ASM			NIHVA TECHNOLOGIES PVT. LTD. PUNE Tel : 020 66304033 Email:- info@nihva.com Website:- www.nihva.com
	NAME	SIGN	DATE
DRAWN	M.SUTAR		02.05.2022
CHECK	M.SUTAR		02.05.2022
APPRD.			
CLIENT - NIHVA TECHNOLOGIES PVT LTD			
PROJECT - DOOR			
SITE LOCATION - PUNE			
If any queries contact : design@nihva.com	DWG. NO. :NIHVA/22-23/VDR/014		REV- 0
ALL DIMENSION ARE IN mm	SCALE: NTS	WT:	SHEET: 01 OF 01