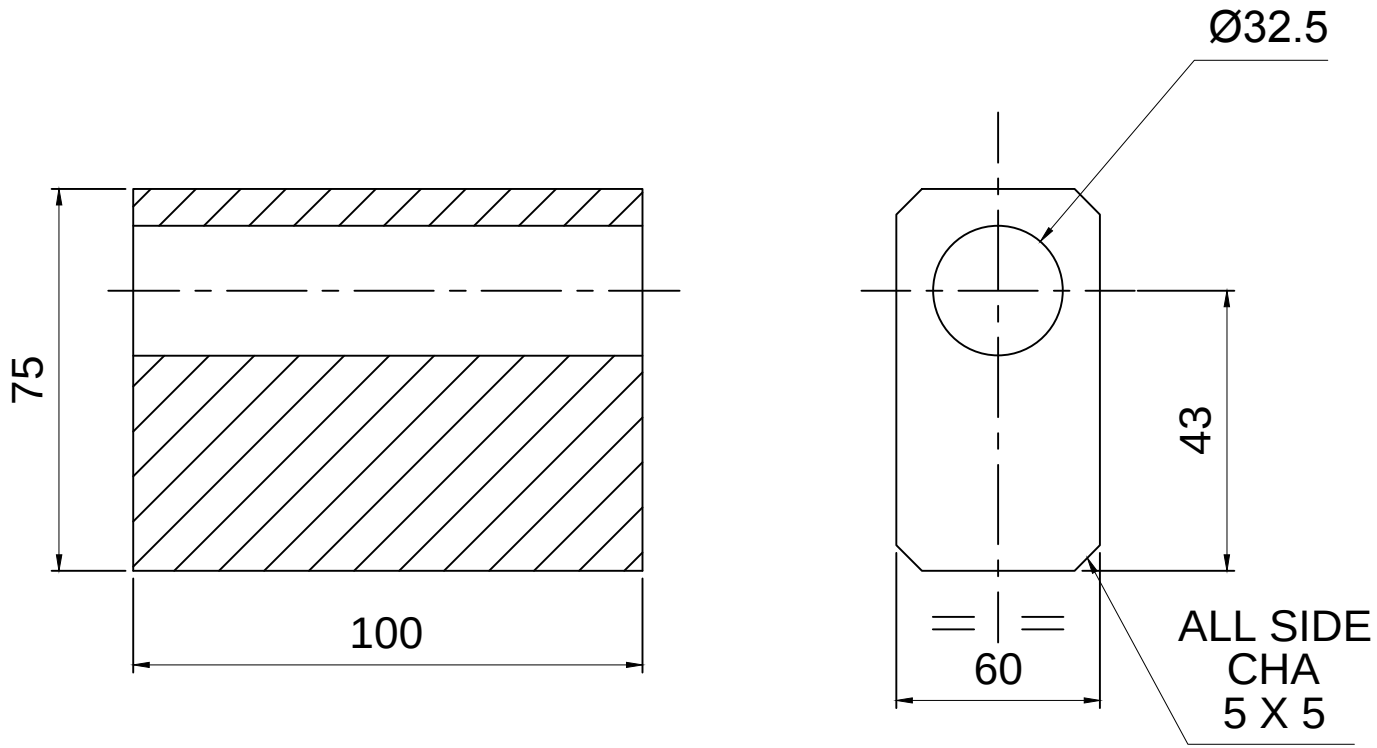


BACK SIDE HINGE BLOCK = 5 NOS
MTL = M.S
75 X 60 THK X 100L = 15 NOS

This drawing & design is the property of NIHVA TECHNOLOGIES. Not to be sold or copied to any other concern.

TITLE
BACK SIDE HINGE BLOCK

NIHVA TECHNOLOGIES PVT. LTD.

NIHVA TECHNOLOGIES PVT. LTD. PUNE
Tel : 020 66304033
Email:- info@nihva.com
Website:- www.nihva.com

	NAME	SIGN	DATE
DRAWN	P.V.A		20.06.2019
CHECK	V.M.T		20.06.2019
APPRD.			

CLIENT -
PROJECT - NDL451
SITE LOCATION -
If any queries contact : design@nihva.com
DWG. NO. : NIHVA/19-20/VDR/064
ALL DIMENSION ARE IN mm
SCALE: NTS
WT:
REV- 00